

ΛΕΠΤΟΜΕΡΕΙΑ ΜΕΛΕΤΗΤΗ
πλάκα στη στάθμη +17,36

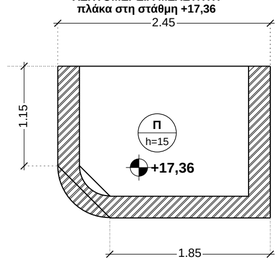

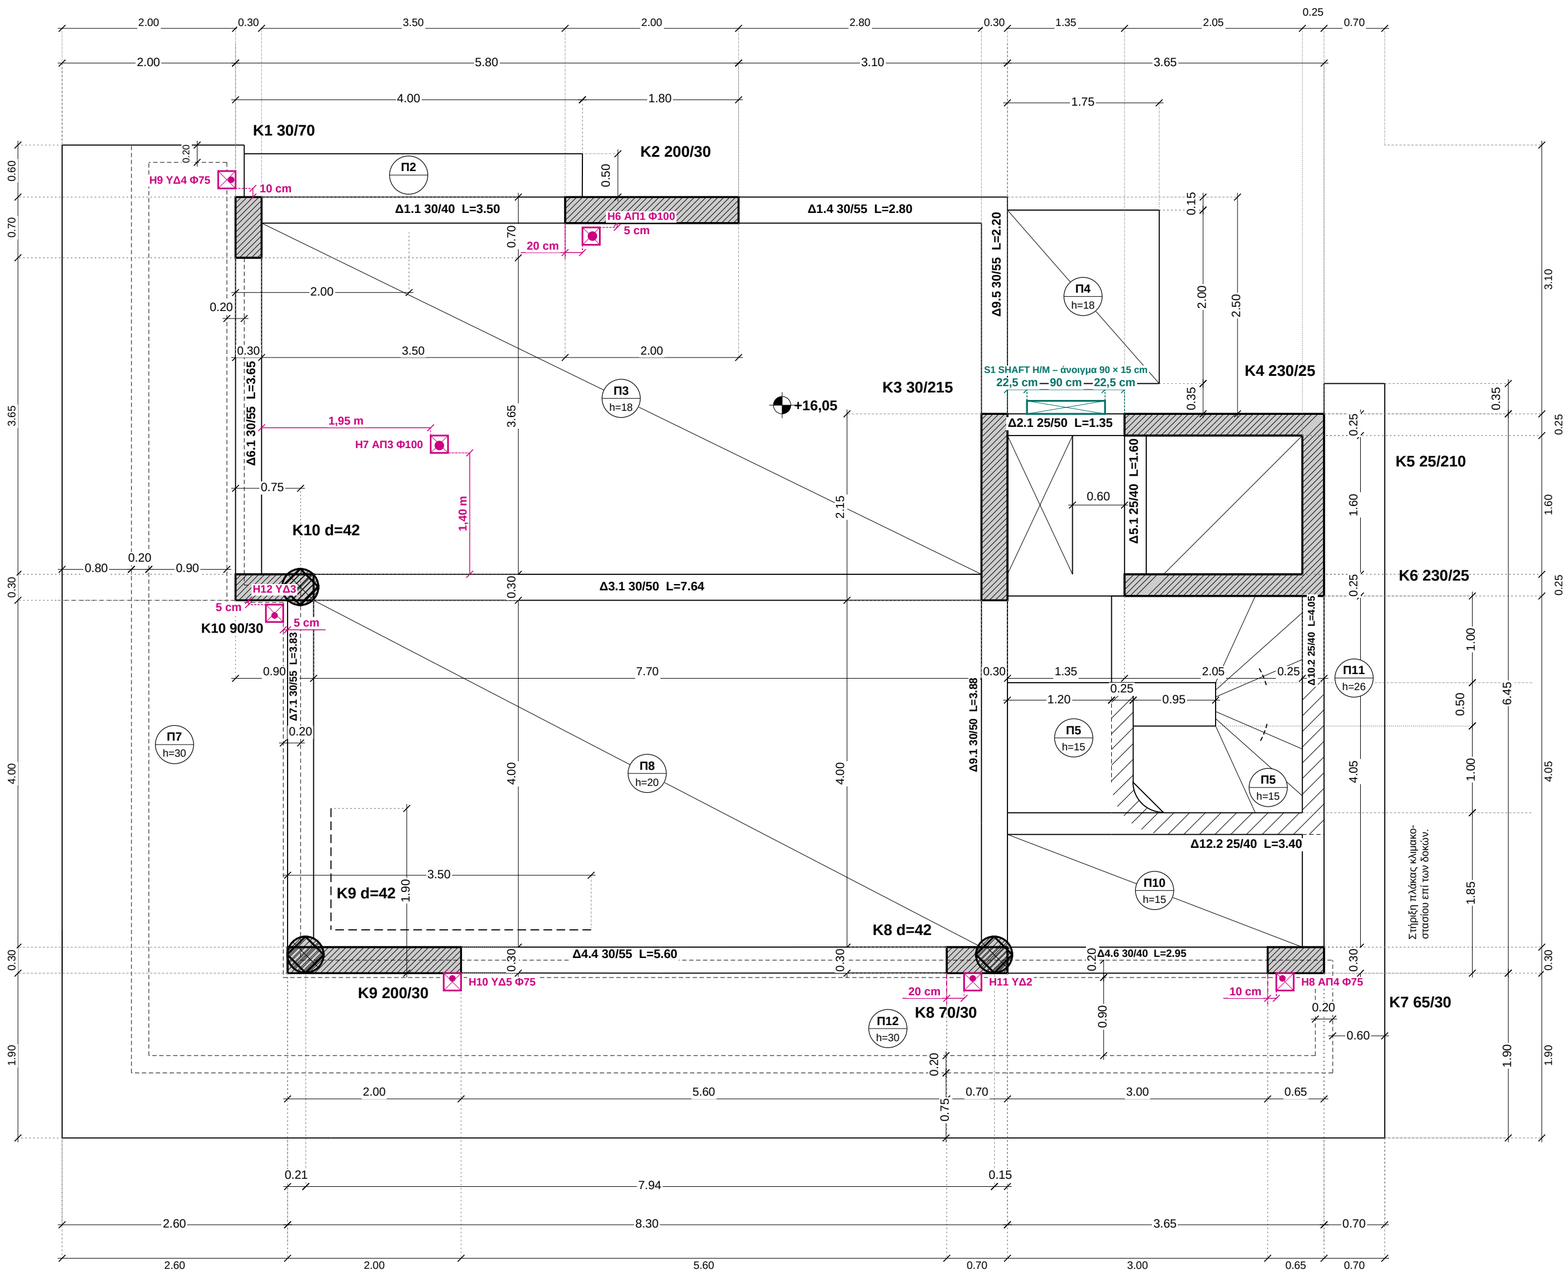

Σ7	ΞΥΛΟΤΥΠΟΣ ΕΡΓΟΤΑΞΙΟΥ	ΣΤΑΘΜΗ ΑΝΩ ΠΛΑΚΑΣ	ΚΛΙΜΑΚΑ	ΕΡΓΟ	
	ΞΥΛΟΤΥΠΟΣ ΟΡΟΦΗΣ Δ΄ ΟΡΟΦΟΥ	**+16,05**	**1:50** (0 1 2 m)	**ΚΩΝΣΤΑΝΤΙΝΟΥΠΟΛΕΩΣ 12 & ΑΓ. ΒΑΡΒΑΡΑΣ, ΑΡΓΥΡΟΥΠΟΛΗ**	A2 – εκτύπωση 100 %
					R06 · 12/11/2026