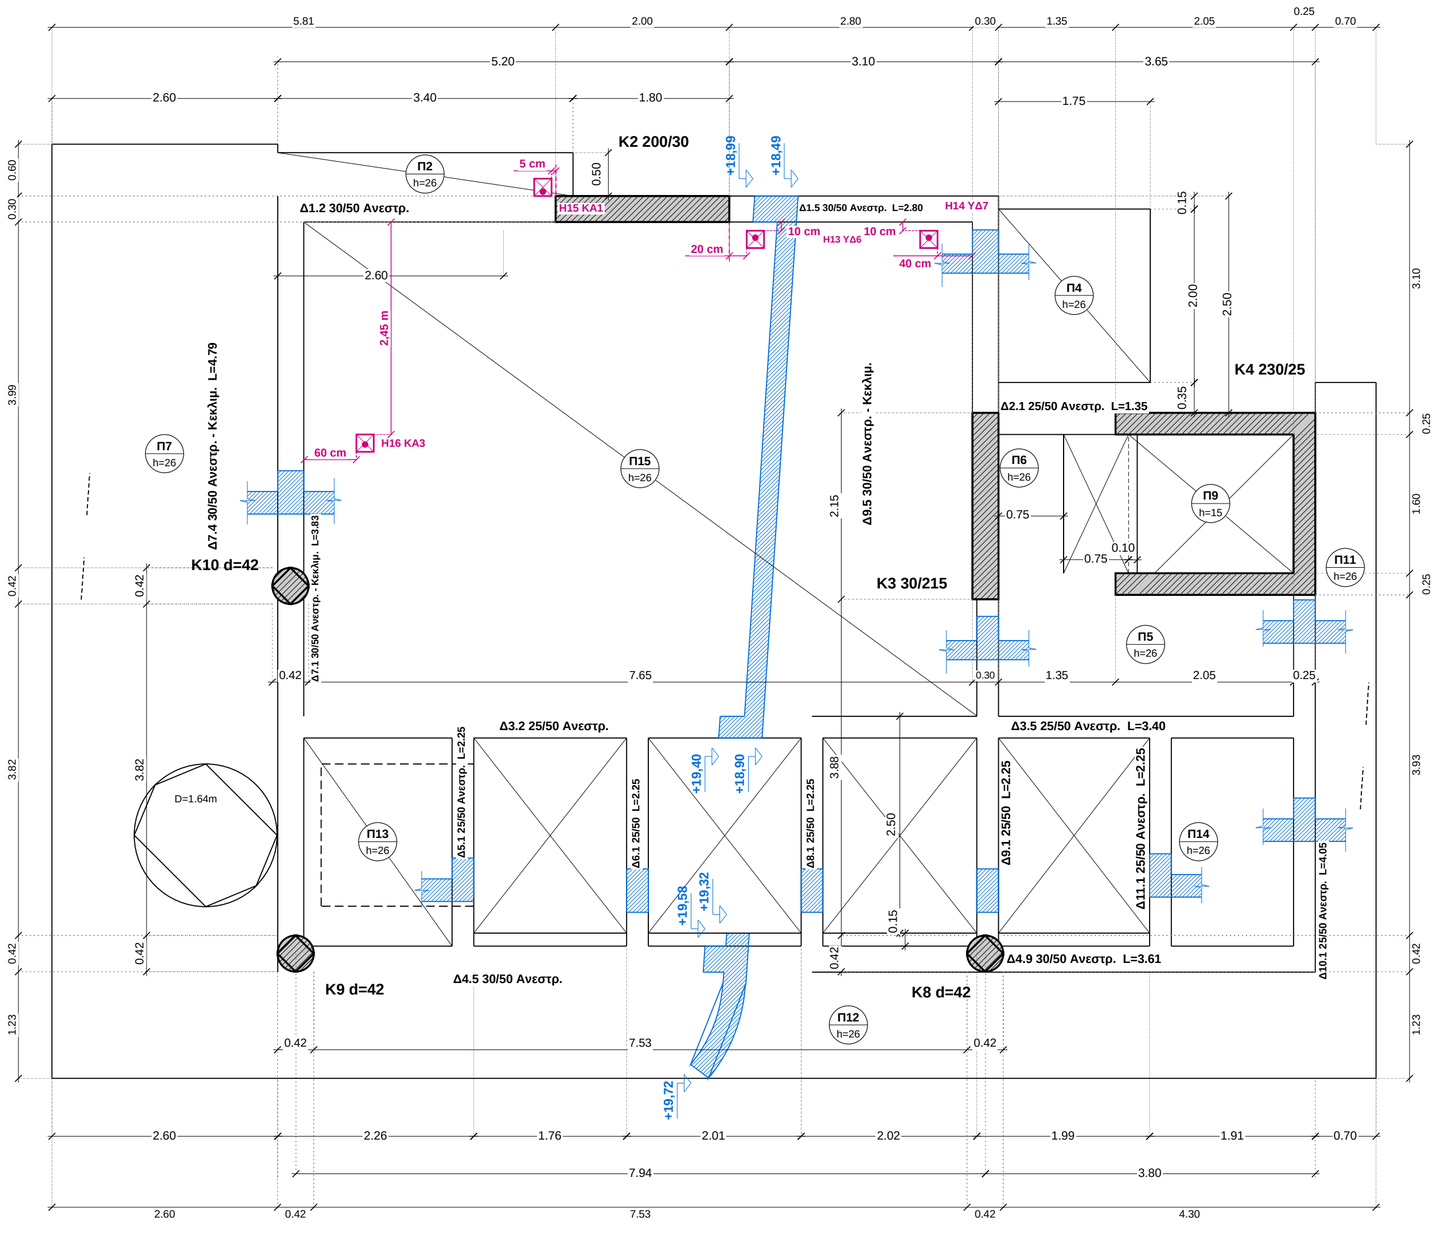


Σ8	ΞΥΛΟΤΥΠΟΣ ΕΡΓΟΤΑΞΙΟΥ **ΞΥΛΟΤΥΠΟΣ ΣΟΦΙΤΑΣ (ΣΤΕΓΗ)**	ΣΤΑΘΜΗ ΑΝΩ ΠΛΑΚΑΣ **+18,49 έως +19,72**	ΚΛΙΜΑΚΑ **1:50** 0 1 2 m	ΕΡΓΟ **ΚΩΝΣΤΑΝΤΙΝΟΥΠΟΛΕΩΣ 12 & ΑΓ. ΒΑΡΒΑΡΑΣ, ΑΡΓΥΡΟΥΠΟΛΗ**	A2 – εκτύπωση 100 % R06 · 12/11/2026