

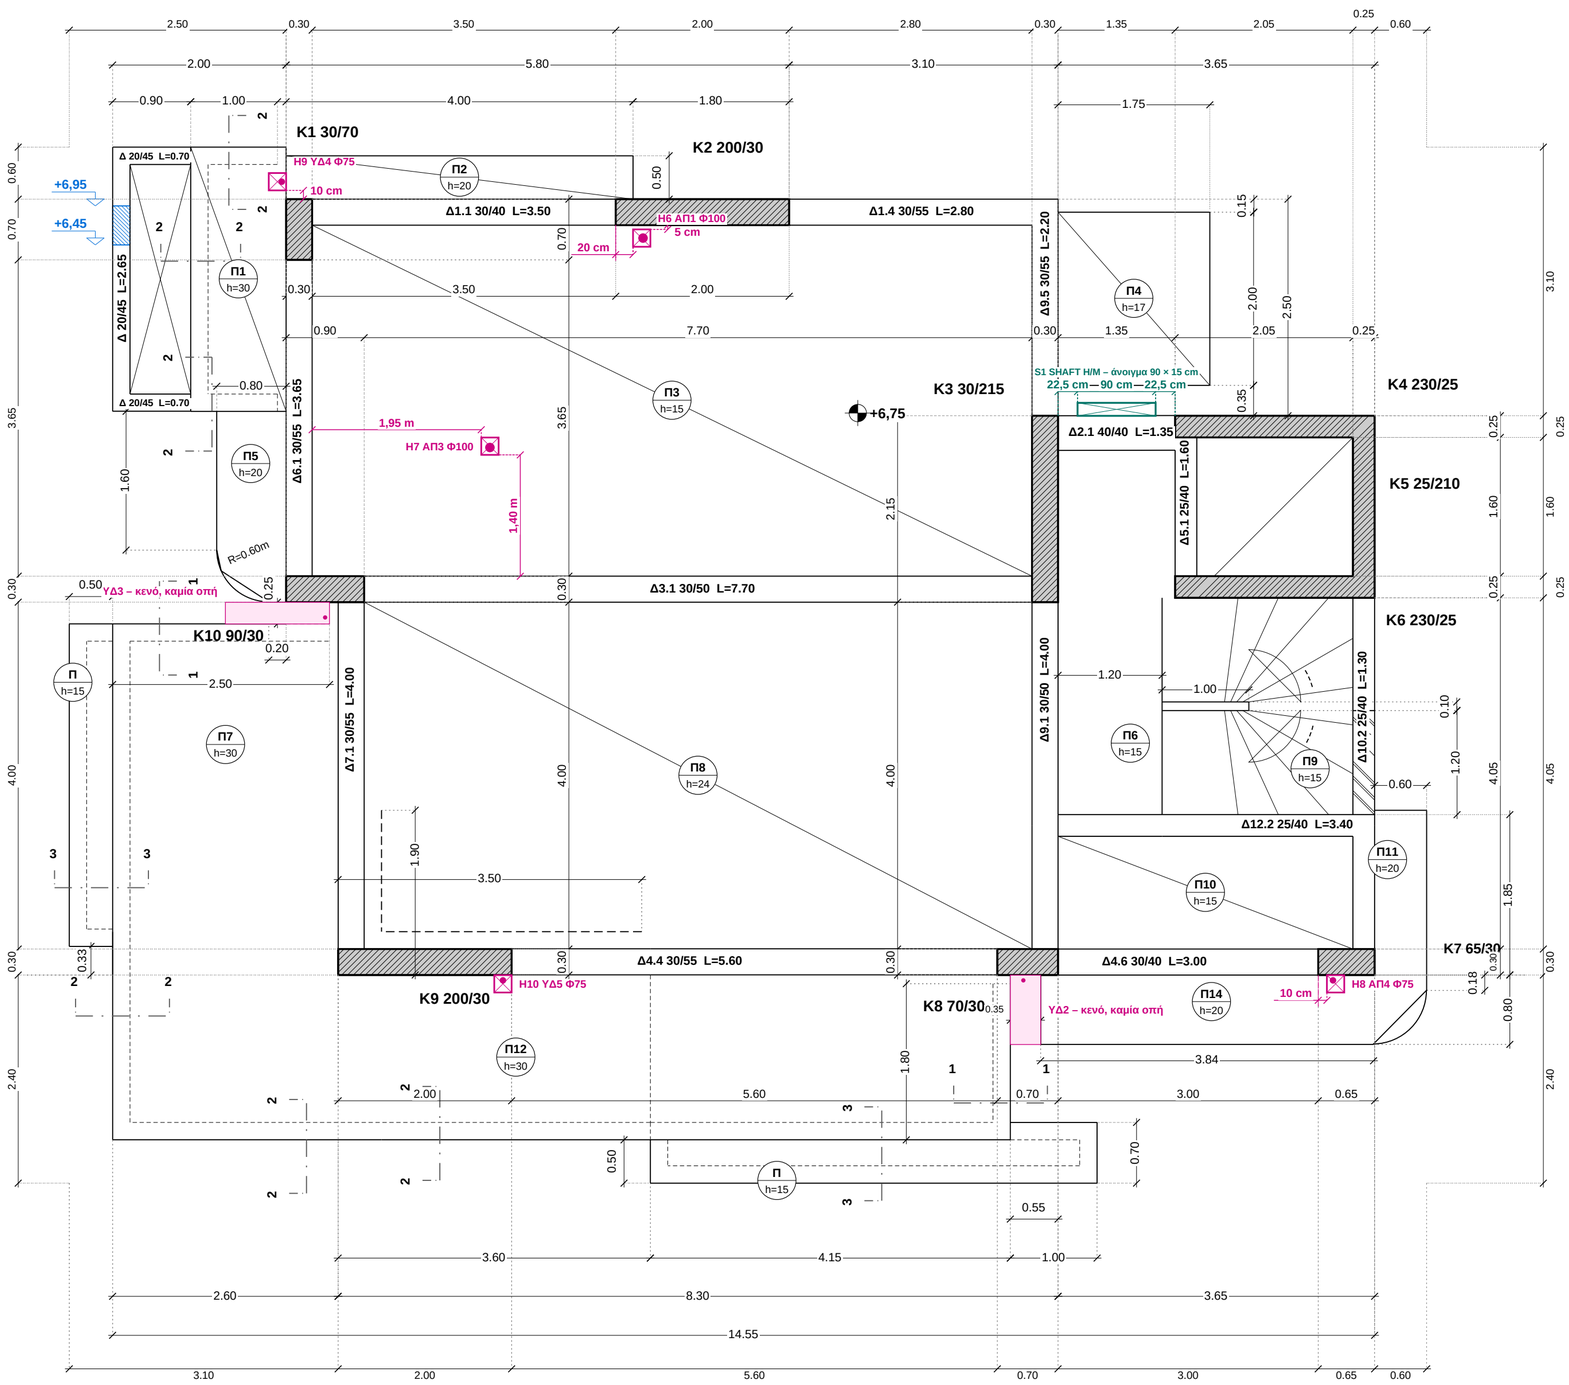


ΤΟΜΕΣ ΜΕΤΩΠΩΝ
(σκαρίφημα χωρίς κλίμακα)


ΤΟΜΗ 1-1

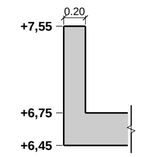

ΤΟΜΗ 2-2

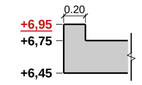

ΤΟΜΗ 3-3

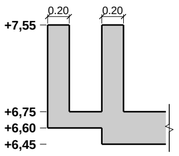

ΚΩΝΣΤΑΝΤΙΝΟΥΠΟΛΕΩΣ 12 & ΑΓ. ΒΑΡΒΑΡΑΣ, ΑΡΓΥΡΟΥΠΟΛΗ – ARKAD Ι.Κ.Ε.
Ξυλότυπος εργοταξίου – χωρίς οπλισμούς

ΞΥΛΟΤΥΠΟΣ ΟΡΟΦΗΣ Α΄ ΟΡΟΦΟΥ — Σ4

ΣΤΑΘΜΗ ΑΝΩ ΠΛΑΚΑΣ
+6,75
ΚΛΙΜΑΚΑ 1:50 — A2 · 100 %

0 1 2 m

K1 30/70	υποστύλωμα / τοιχείο (cm)
Δ1.1 30/40	δοκός: πλάτος / ύψος (το ύψος μαζί με την πλάκα)
L=3.50	καθαρό μήκος δοκού, παρειά με παρειά
Π3 h=15	πλάκα – πάχος (cm)
+0,30	στάθμη άνω μπετού (m)
μπλε	τομές επί τόπου / φυτευτά και οι στάθμες τους
☒	οπή πλάκας 20 × 20 (αποχέτευση / υδρορροή)
▭	άνοιγμα shaft H/M στην πλάκα

Διαστάσεις σε m, από γωνία / παρειά κολόνας σε γωνία κολόνας. Οι αλυσίδες παρειών μετρήθηκαν από τη γεωμετρία του σχεδίου, οι υπόλοιπες είναι του μελετητή.

ΠΑΤΟΙ ΚΑΛΟΥΠΙΩΝ	στάθμη	ύψος*
Πλάκα h=15	**+6,60**	**2,95**
Πλάκα h=17	**+6,58**	**2,93**
Πλάκα h=20	**+6,55**	**2,90**
Πλάκα h=24	**+6,51**	**2,86**
Πλάκα h=30	**+6,45**	**2,80**
Δοκός ύψους 40	**+6,35**	**2,70**
Δοκός ύψους 50	**+6,25**	**2,60**
Δοκός ύψους 55	**+6,20**	**2,55**

* από την πλάκα του κάτω ορόφου (+3,65). Υπολογισμένα (στάθμη − ύψος)· όχι για ανεστραμμένες δοκούς / φυτευτά.

ΟΠΕΣ ΠΛΑΚΑΣ – ΚΟΥΤΙ 20 × 20 · SHAFT
Θέση σε cm ως την ΑΚΜΗ του κουτιού, από παρειές σκυροδέματος.

H6 **ΑΠ1 Φ100**
20 ανατ. της Δ παρ. K2 · 5 νότια της N παρ. K2

H7 **ΑΠ3 Φ100**
1,95 m ανατ. της A παρ. Δ6.1 · 1,4 m βόρ. της B παρ. Δ3.1

H8 **ΑΠ4 Φ75**
10 ανατ. της Δ παρ. K7 · κολλητά στη N παρ. K7

H9 **ΥΔ4 Φ75**
ανατ. ακμή στην ευθεία της Δ παρ. K1 · 10 βόρ. της B παρ. K1

H10 **ΥΔ5 Φ75**
ανατ. ακμή στην ευθεία της A παρ. K9 · κολλητά στη N παρ. K9

ΥΔ2 κενό 35 cm νότια της K8 – ΚΑΜΙΑ οπή

ΥΔ3 κενό 25 cm δυτικά της K10 – ΚΑΜΙΑ οπή

S1 **SHAFT H/M**
άνοιγμα 90 × 15 στη μέση K3 – ανελκυστήρα: 22,5 cm από την A παρ. K3 και 22,5 cm από το τοιχείο K4 · κολλητά στη B παρ. Δ2.1 · βάθος 15 ως την εσωτ. παρειά του τοίχου T5-01

Τεύχος αποχετεύσεων R22, φύλλο ΑΠ-13.
Καμία οπή σε δοκό, καμία αναμονή σε στηθαίο.

ΣΗΜΕΙΩΣΕΙΣ

· ΤΟΜΗ 2-2: μετόπη +6,45 έως +6,95 (ύψος 0,50 όπως Σ5) – αλλαγή 10/11/2026· ο μελετητής είχε +6,90. Να ενημερωθεί ο στατικός.

· Πρόβολοι: υποδοχή σιφωνιού και υδρορροή ΠΡΙΝ το μπετό, να μην κοπεί οπλισμός (μελετητής).

· Διαγραμμισμένο τοιχείο δίπλα στη σκάλα (0,60): έως το ύψος της σκάλας (μελετητής).

Βάση: Σ4_ΕΦ.pdf – ξυλότυπος οροφής Α΄ ορόφου, Γ. Κόγιας (Drive 19/10/2026).
Οπλισμοί ΜΟΝΟ από το σχέδιο του μελετητή.

Έκδοση R05 – 11/11/2026