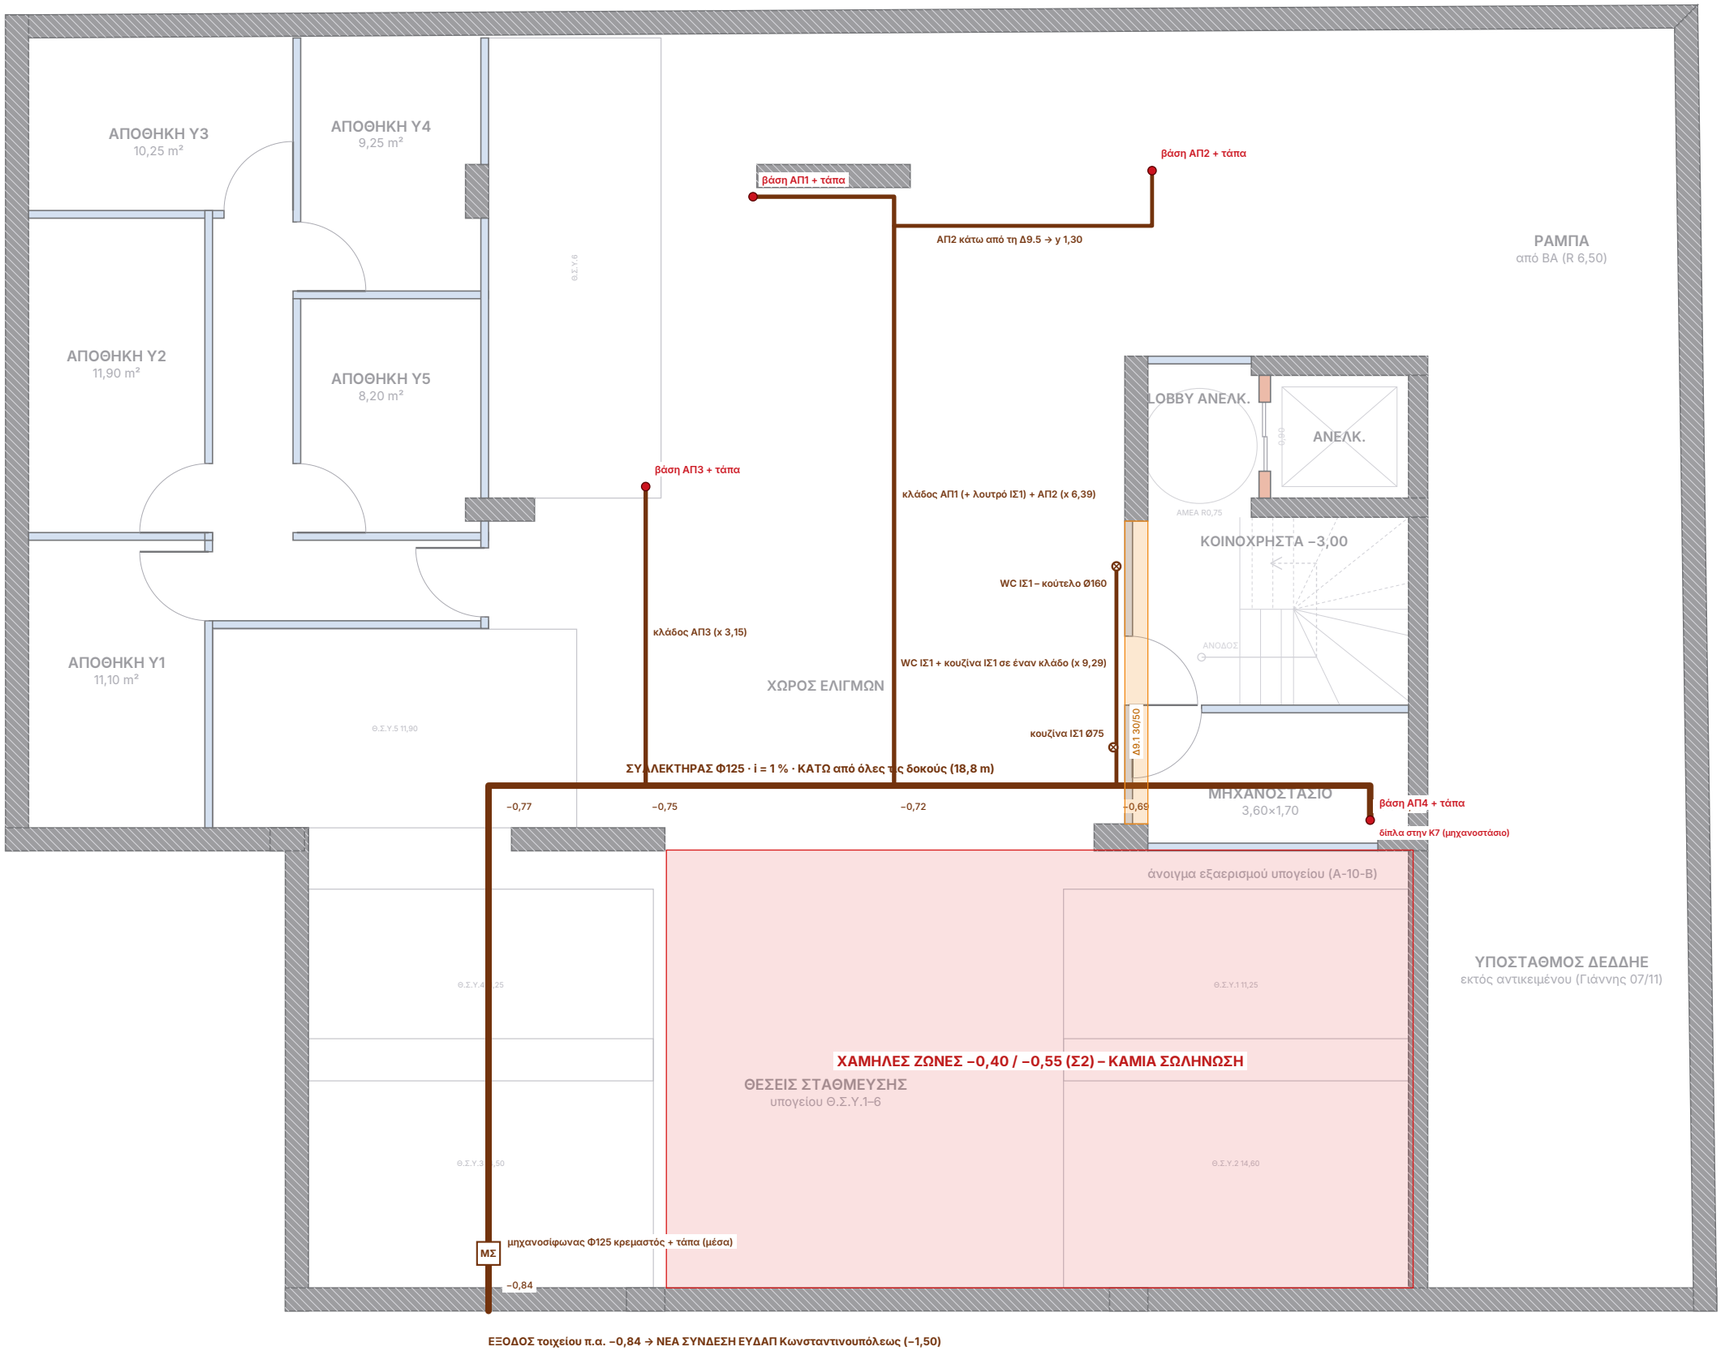


B


ΥΠΟΜΝΗΜΑ

- Στήλη λυμάτων ΑΠ (Φ100 / ΑΠ4 Φ75) · αερισμός συνεχίζει
- Θέση R14 όπου μετακινήθηκε (διακεκομμένη)
- Λεκάνη → στήλη Φ90 / Φ100
- Ποτισόφωνο / σιφώνι → στήλη Φ50–Φ75
- Ντους / πλυντήριο Φ50 · νιπτήρας Φ40 · νεροχύτης Φ50
- Ποτισόφωνο ΠΣ (σιφώνι δαπέδου)
- Υδρορροή ΥΔ Φ75 μέσα στη θερμοπρόσοψη (αναμονή Ø125)
- Σιφώνι ομβρίων εξώστη · διακεκ. = πλευρική έξοδος
- Δοκός (Σ4/Σ5) – καμία οπή
- Συλλεκτήρας Φ125 / κλάδοι – κρεμαστοί κάτω από δοκούς

ΣΗΜΕΙΩΣΕΙΣ ΥΠΟΓΕΙΟΥ – R15

1. Διαδρομή και στάθμες όπως R14: κεφαλή ΑΠ4 −0,65 → έξοδος ΝΔ −0,84, i = 1 %, κάτω από όλες τις δοκούς Σ2 – καμία διάτρηση.
2. R15: το λουτρό ΙΣ1 δεν έχει πια δική του πτώση – μπαίνει στην ΑΠ1 πάνω από την πλάκα.
3. R15: WC ΙΣ1 κατεβαίνει στο κούτελο 9,29 / 5,74 (πλάκα, 5 cm δυτικά της Δ9.1) και ενώνεται με τον νεροχύτη ΙΣ1 σε έναν κλάδο.
4. R15: βάση ΑΠ4 12,60 / 9,05 μέσα στο μηχανοστάσιο, κολλητά στην Κ7 (πλάκα Π10, βόρεια της δοκού Κ8–Κ7).
5. Χαμηλές ζώνες −0,40 / −0,55: τίποτα. Ο υποσταθμός ΔΕΔΔΗΕ δεν αγγίζεται.
6. ΑΝΟΙΚΤΑ: βάθος ΕΥΔΑΠ −1,50 · καθαρό ύψος 2,16 πάνω από Θ.Σ.Υ. 3/4 (< 2,20).

ΕΡΓΟ	ΘΕΜΑ ΣΧΕΔΙΟΥ	ΒΑΣΗ	ΑΡ. ΣΧΕΔΙΟΥ
ΠΕΝΤΑΟΡΟΦΟ ΚΤΗΡΙΟ ΚΑΤΟΙΚΙΩΝ – ΑΡΓΥΡΟΥΠΟΛΗ Κωνσταντινουπόλεως 12 & Αγ. Βαρβάρας · Ο.Τ. 103-15 Εργοδότης: INTERKAT Α.Ε. · Κατασκευή: ARKAD Ι.Κ.Ε.	**ΟΡΟΦΗ ΥΠΟΓΕΙΟΥ – ΣΥΛΛΕΚΤΗΡΑΣ** R15 · σχόλια 10/11/2026 · λύματα · αερισμοί · όμβρια ΥΠΟΓΕΙΟ – συλλεκτήρας κάτω από τις δοκούς · έξοδος −0,84	R14 · Σ2 εφαρμογής · τοιχοποιίες υπογείου R05	**ΑΠ-01** **Κλίμακα 1:80 · A3** 10/11/2026 · R15

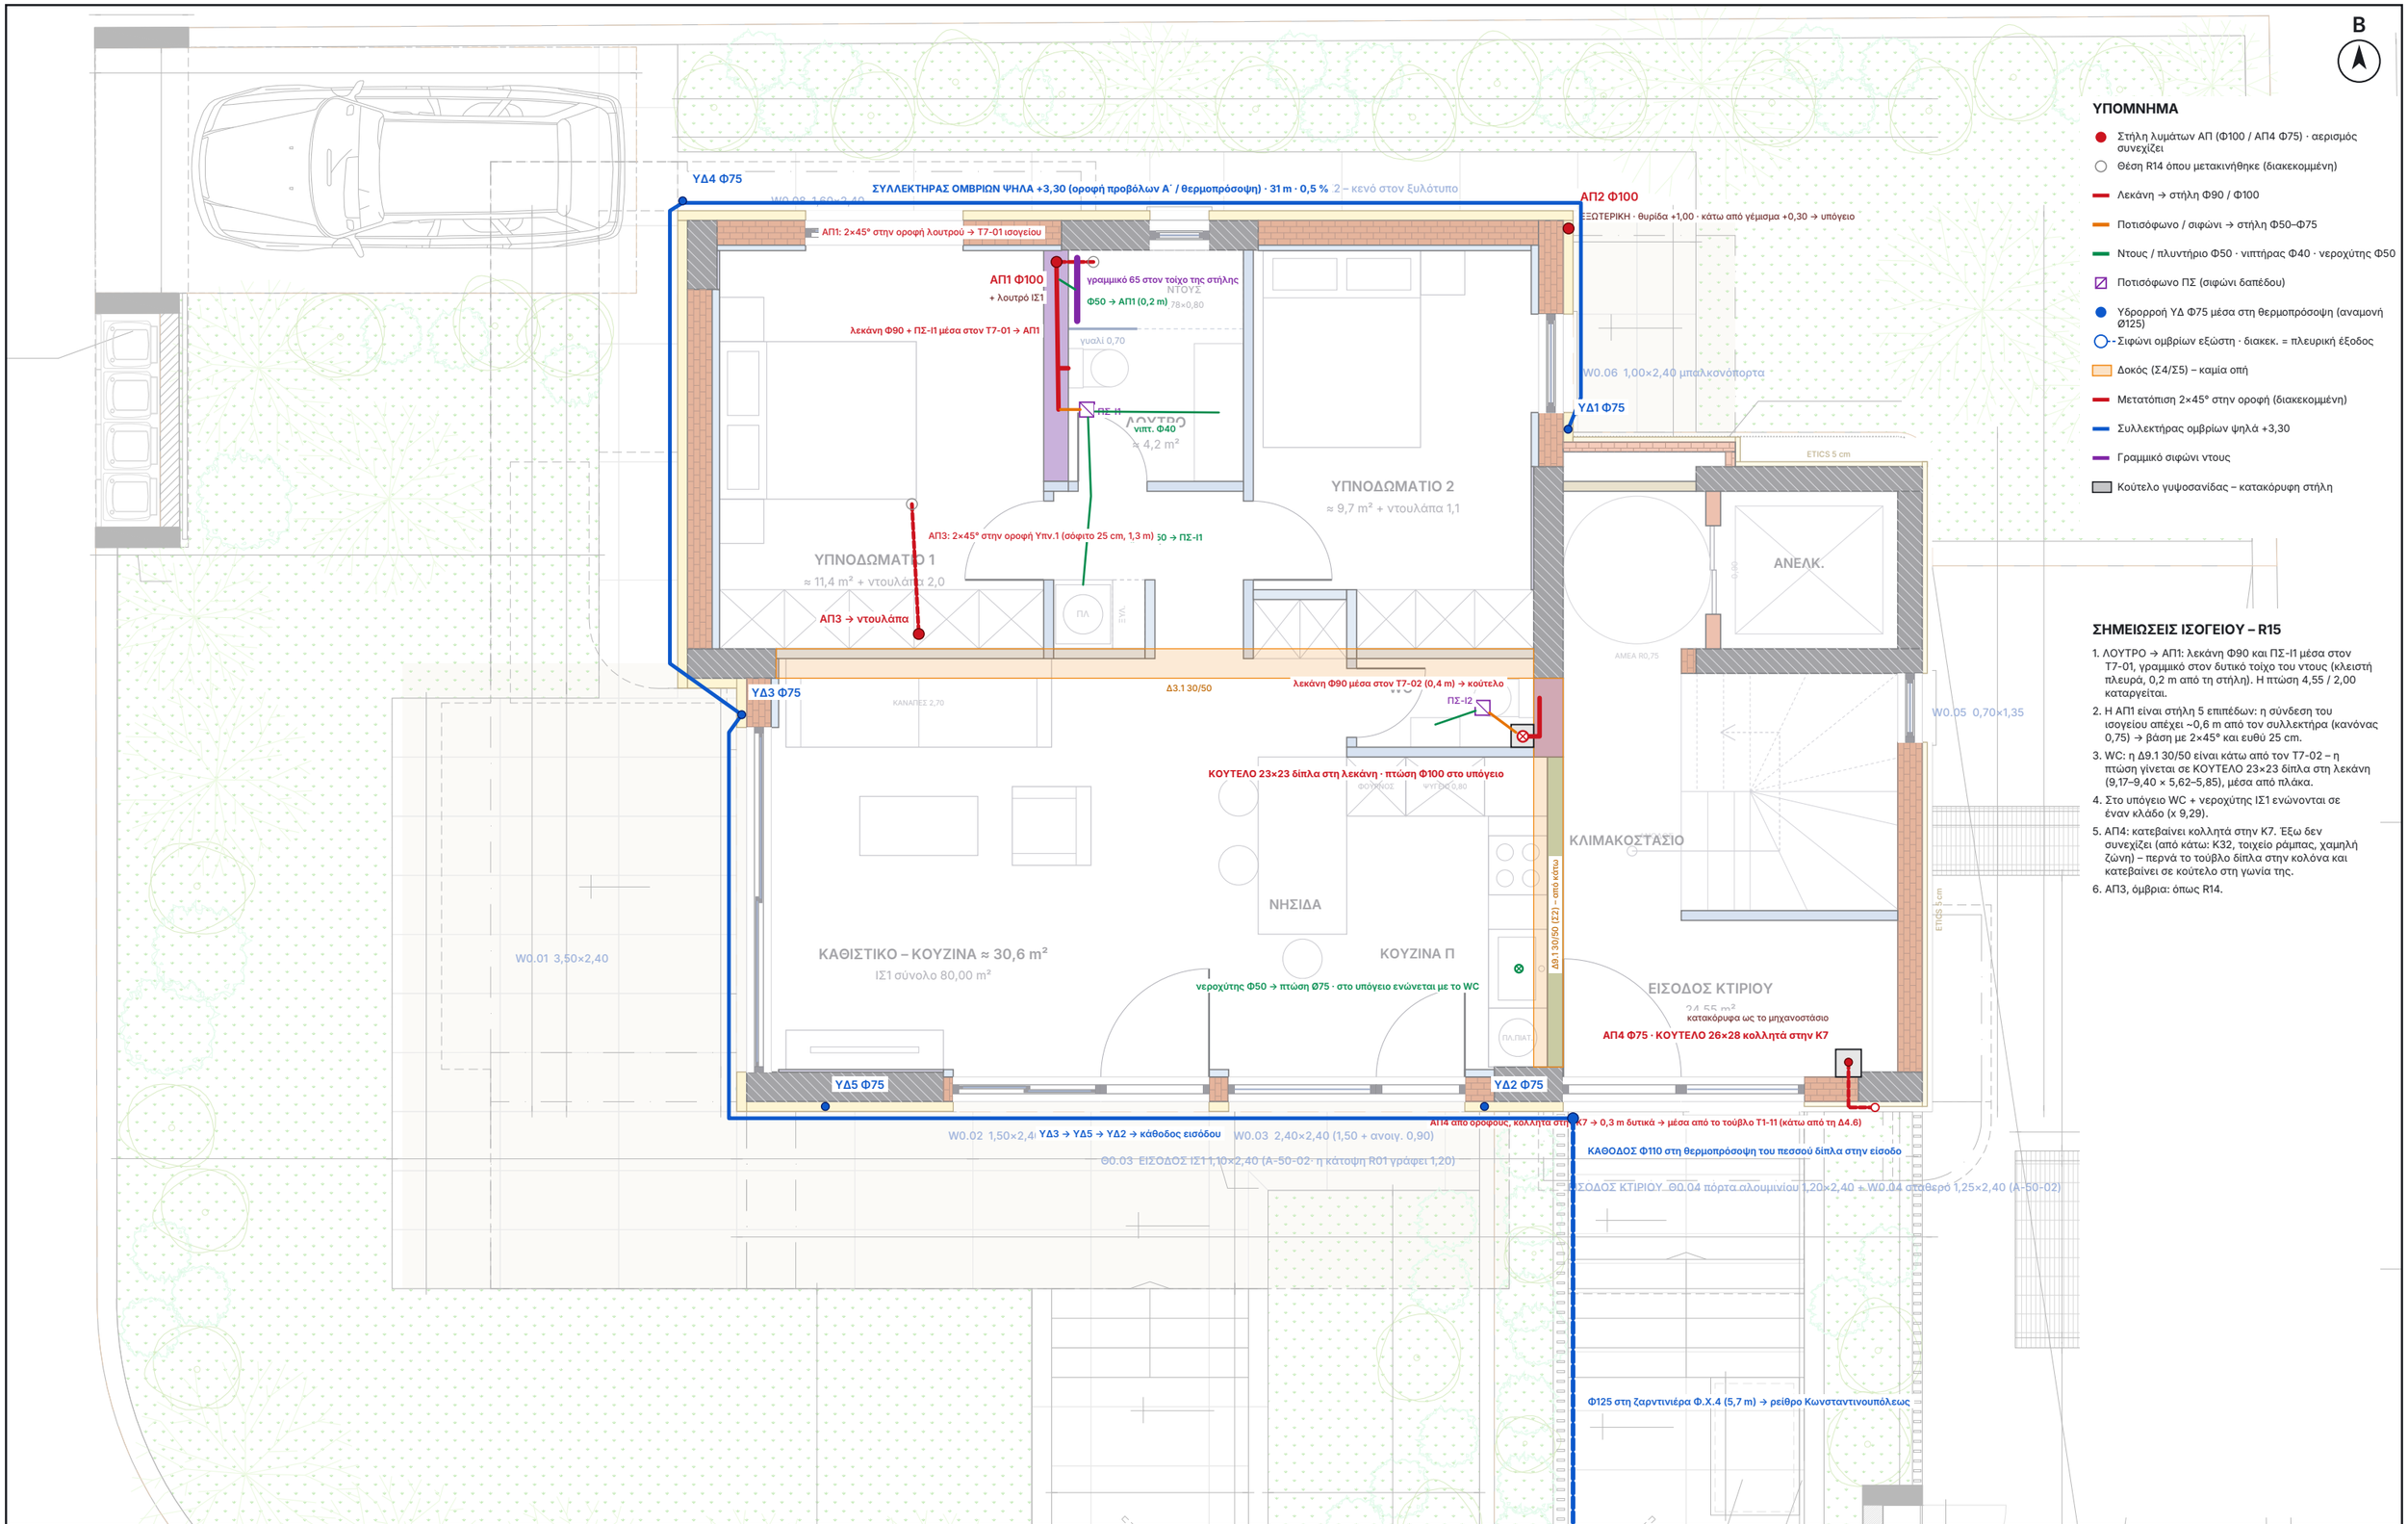

ΕΡΓΟ

ΠΕΝΤΑΟΡΟΦΟ ΚΤΗΡΙΟ ΚΑΤΟΙΚΙΩΝ – ΑΡΓΥΡΟΥΠΟΛΗ
Κωνσταντινουπόλεως 12 & Αγ. Βαρβάρας · Ο.Τ. 103-15
Εργοδότης: INTERKAT Α.Ε. · Κατασκευή: ARKAD Ι.Κ.Ε.

ΘΕΜΑ ΣΧΕΔΙΟΥ


ΙΣΟΓΕΙΟ – ΑΠΟΧΕΤΕΥΣΗ & ΟΜΒΡΙΑ
R15 · σχόλια 10/11/2026 · λύματα · αερισμοί · όμβρια
ΙΣΟΓΕΙΟ – λουτρό στην ΑΠ1 · κούτελα WC / ΑΠ4 · όμβρια ψηλά

ΒΑΣΗ

R14 · Σ2 / Σ3 εφαρμογής · τοιχοποιίες ισογείου R13

ΑΡ. ΣΧΕΔΙΟΥ

ΑΠ-02
Κλίμακα 1:60 · Α3
10/11/2026 · R15

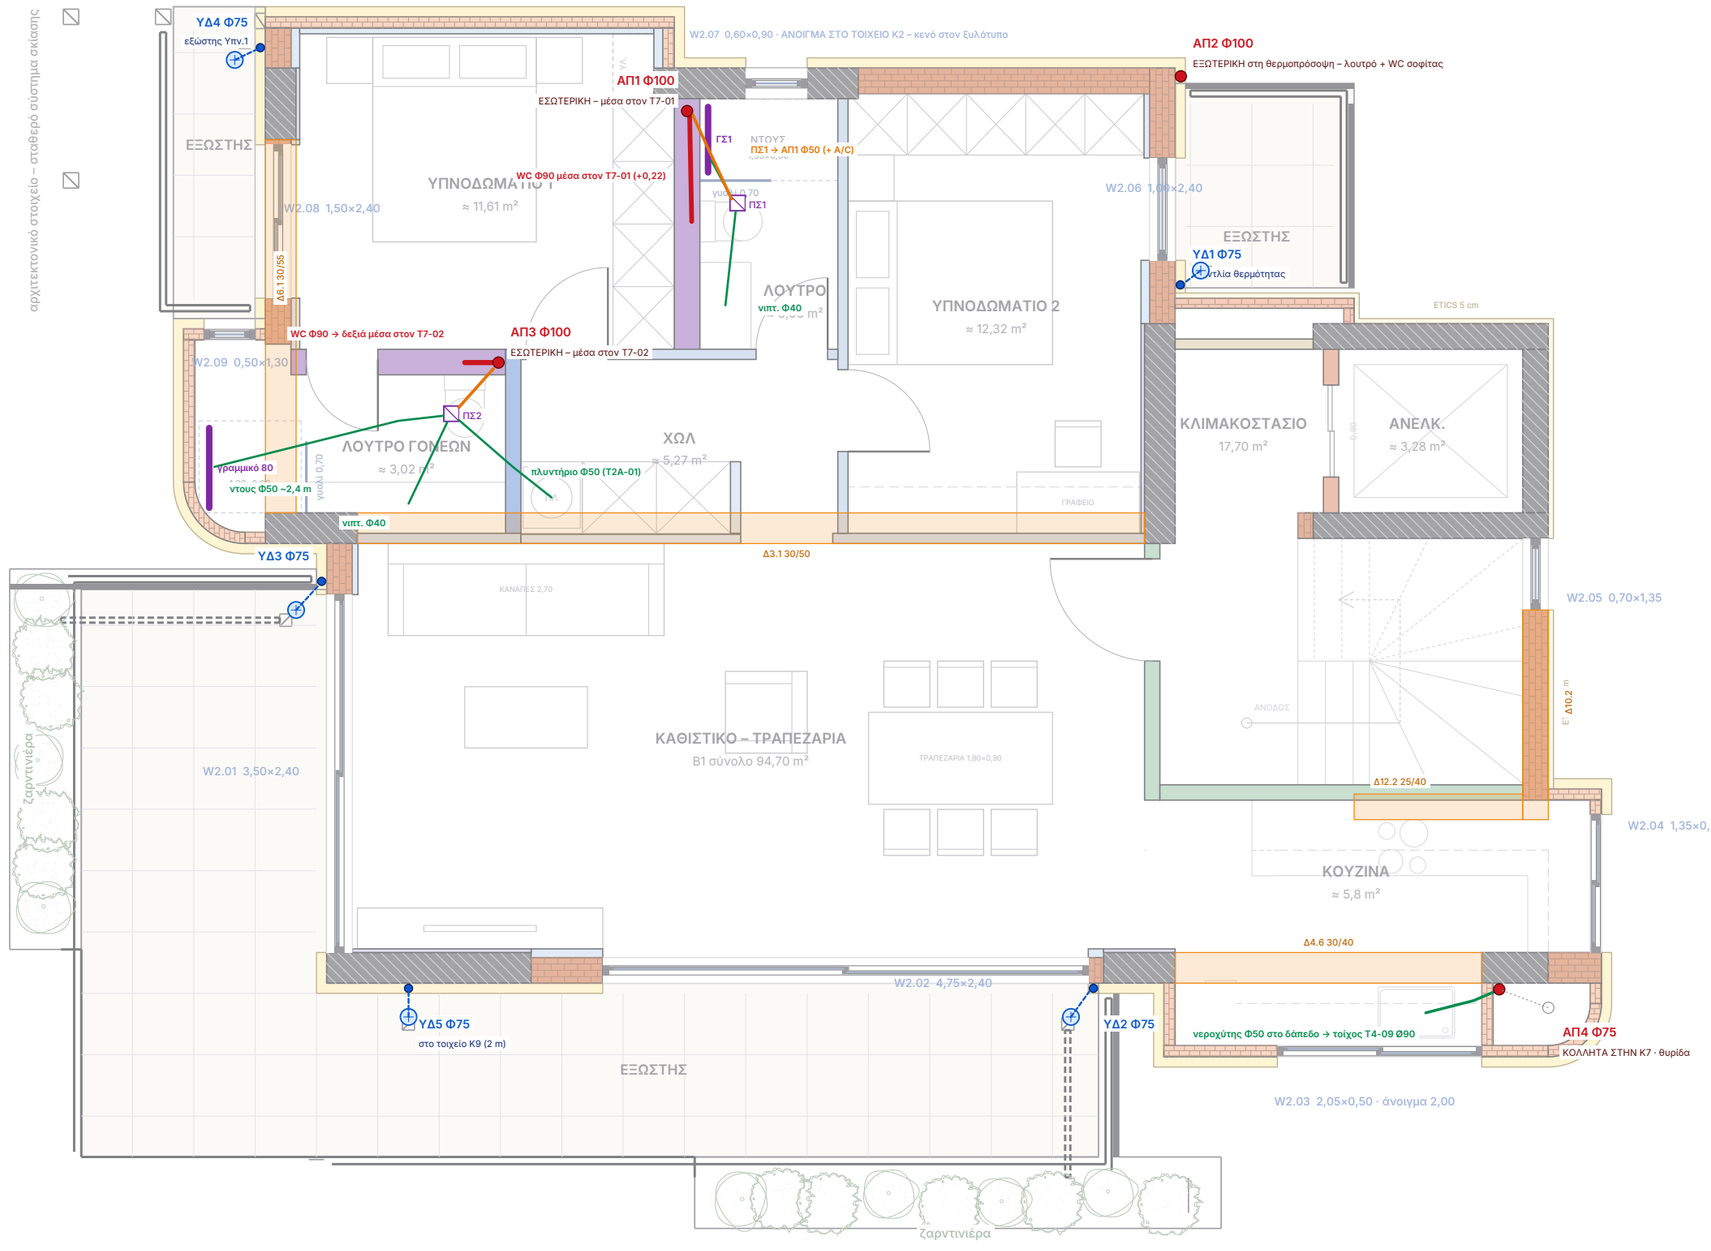

B


ΥΠΟΜΝΗΜΑ

- Στήλη λυμάτων ΑΠ (Φ100 / ΑΠ4 Φ75) · αερισμός συνεχίζει
- Θέση R14 όπου μετακινήθηκε (διακεκομμένη)
- Λεκάνη → στήλη Φ90 / Φ100
- Ποτισόφωνο / σιφώνι → στήλη Φ50–Φ75
- Ντους / πλυντήριο Φ50 · νιπτήρας Φ40 · νεροχύτης Φ50
- Ποτισόφωνο ΠΣ (σιφώνι δαπέδου)
- Υδρορροή ΥΔ Φ75 μέσα στη θερμοπρόσοψη (αναμονή Ø125)
- Σιφώνι ομβρίων εξώστη · διακεκ. = πλευρική έξοδος
- Δοκός (Σ4/Σ5) – καμία οπή
- Γραμμικό σιφώνι ντους

ΣΗΜΕΙΩΣΕΙΣ – R15

1. R15: η ΑΠ4 Φ75 πήγε ΚΟΛΛΗΤΑ στη νότια παρειά της κολόνας Κ7 (12,87 / 9,51, από 13,35 / 9,69) – κατεβαίνει από την προβλεπόμενη οπή δίπλα στην κολόνα, στερεωμένη πάνω της.
2. Νεροχύτης: Φ50 στο δάπεδο → μέσα από τον Τ4-09 → ΑΠ4 (0,8 m).
3. ΑΠ1 μέσα στον Τ7-01 (4,925 / 0,92), ΑΠ3 μέσα στον Τ7-02 (3,08 / 3,38) – όπως R14.
4. ΑΠ2 εξωτερική στη ΒΑ γωνία: R15 παίρνει λουτρό + WC σοφίτας (όχι μόνο το WC).
5. Λεκάνες κρεμαστές, Φ90 μέσα στους τοίχους λεκάνης (+0,22). Ποτισόφωνα δίπλα στις λεκάνες.
6. Πλυντήριο → ΠΣ2 μέσα από τον Τ2Α-01. Υδρορροές όπως R14.

ΕΡΓΟ	ΘΕΜΑ ΣΧΕΔΙΟΥ	ΒΑΣΗ	ΑΡ. ΣΧΕΔΙΟΥ
ΠΕΝΤΑΟΡΟΦΟ ΚΤΗΡΙΟ ΚΑΤΟΙΚΙΩΝ – ΑΡΓΥΡΟΥΠΟΛΗ Κωνσταντινουπόλεως 12 & Αγ. Βαρβάρας · Ο.Τ. 103-15 Εργοδότης: INTERKAT Α.Ε. · Κατασκευή: ARKAD Ι.Κ.Ε.	**Α΄·Β΄·Γ΄ ΟΡΟΦΟΣ – ΣΤΗΛΕΣ & ΣΥΝΔΕΣΕΙΣ** R15 · σχόλια 10/11/2026 · λύματα · αερισμοί · όμβρια Α΄ · Β΄ · Γ΄ ΟΡΟΦΟΣ – τυπικός (Β1)	R14 · Σ4 / Σ5 · τοιχοποιίες τυπικού R25	**ΑΠ-03** **Κλίμακα 1:60 · Α3** 10/11/2026 · R15

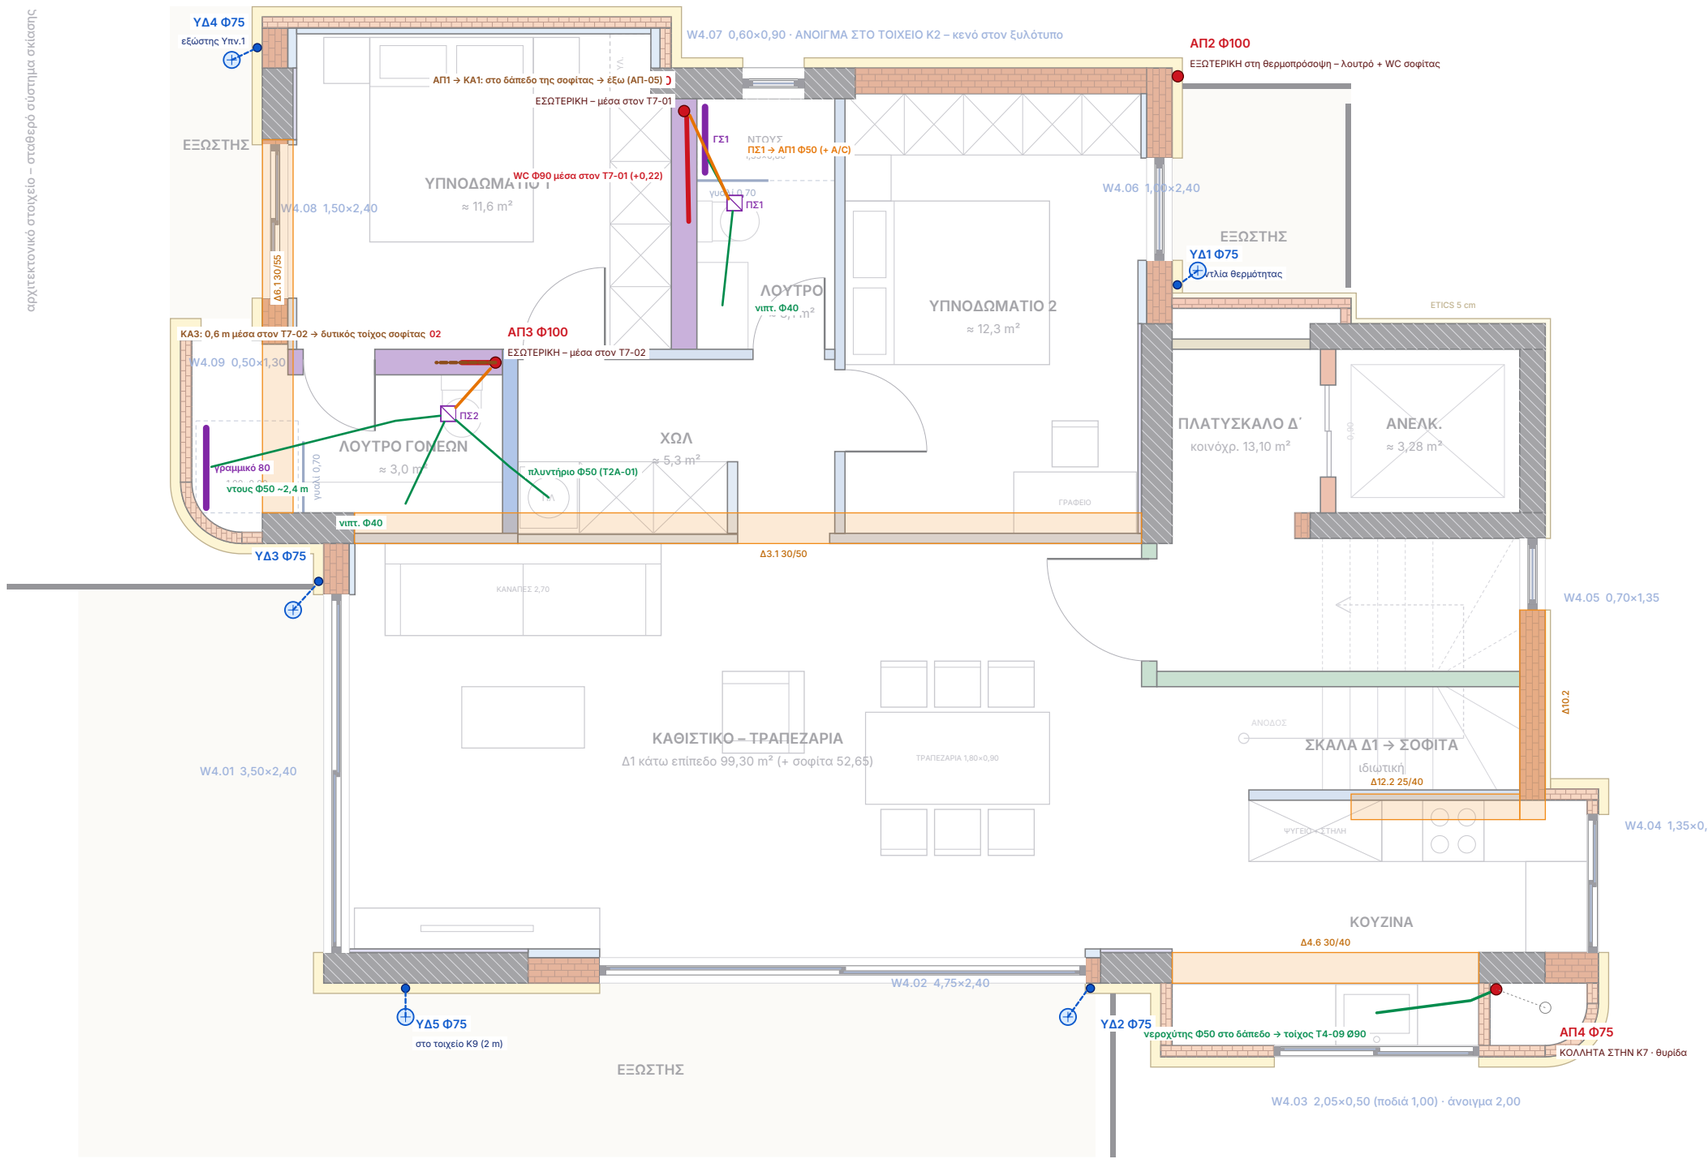


ΥΠΟΜΝΗΜΑ

- Στήλη λυμάτων ΑΠ (Φ100 / ΑΠ4 Φ75) · αερισμός συνεχίζει
- Θέση R14 όπου μετακινήθηκε (διακεκομμένη)
- Λεκάνη → στήλη Φ90 / Φ100
- Ποτισόφωνο / σιφώνι → στήλη Φ50–Φ75
- Ντους / πλυντήριο Φ50 · νιπτήρας Φ40 · νεροχύτης Φ50
- Ποτισόφωνο ΠΣ (σιφώνι δαπέδου)
- Υδρορροή ΥΔ Φ75 μέσα στη θερμοπρόσοψη (αναμονή Ø125)
- Σιφώνι ομβρίων εξώστη · διακεκ. = πλευρική έξοδος
- Δοκός (Σ4/Σ5) – καμία οπή
- Γραμμικό σιφώνι ντους

ΣΗΜΕΙΩΣΕΙΣ – R15

1. R15: η ΑΠ4 Φ75 πήγε ΚΟΛΛΗΤΑ στη νότια παρειά της κολόνας Κ7 (12,87 / 9,51, από 13,35 / 9,69) – κατεβαίνει από την προβλεπόμενη οπή δίπλα στην κολόνα, στερεωμένη πάνω της.
2. Νεροχύτης: Φ50 στο δάπεδο → μέσα από τον Τ4-09 → ΑΠ4 (0,8 m).
3. ΑΠ1 μέσα στον Τ7-01 (4,925 / 0,92), ΑΠ3 μέσα στον Τ7-02 (3,08 / 3,38) – όπως R14.
4. ΑΠ2 εξωτερική στη ΒΑ γωνία: R15 παίρνει λουτρό + WC σοφίτας (όχι μόνο το WC).
5. Λεκάνες κρεμαστές, Φ90 μέσα στους τοίχους λεκάνης (+0,22). Ποτισόφωνα δίπλα στις λεκάνες.
6. Πλυντήριο → ΠΣ2 μέσα από τον Τ2Α-01. Υδρορροές όπως R14.

ΕΡΓΟ	ΘΕΜΑ ΣΧΕΔΙΟΥ	ΒΑΣΗ	ΑΡ. ΣΧΕΔΙΟΥ
ΠΕΝΤΑΟΡΟΦΟ ΚΤΗΡΙΟ ΚΑΤΟΙΚΙΩΝ – ΑΡΓΥΡΟΥΠΟΛΗ Κωνσταντινουπόλεως 12 & Αγ. Βαρβάρας · Ο.Τ. 103-15 Εργοδότης: INTERKAT Α.Ε. · Κατασκευή: ARKAD Ι.Κ.Ε.	**Δ΄ ΟΡΟΦΟΣ – ΣΤΗΛΕΣ & ΣΥΝΔΕΣΕΙΣ** R15 · σχόλια 10/11/2026 · λύματα · αερισμοί · όμβρια Δ΄ ΟΡΟΦΟΣ – Δ1 κάτω επίπεδο	R14 · Σ7 · τοιχοποιίες Δ΄ R04	**ΑΠ-04** **Κλίμακα 1:60 · Α3** 10/11/2026 · R15

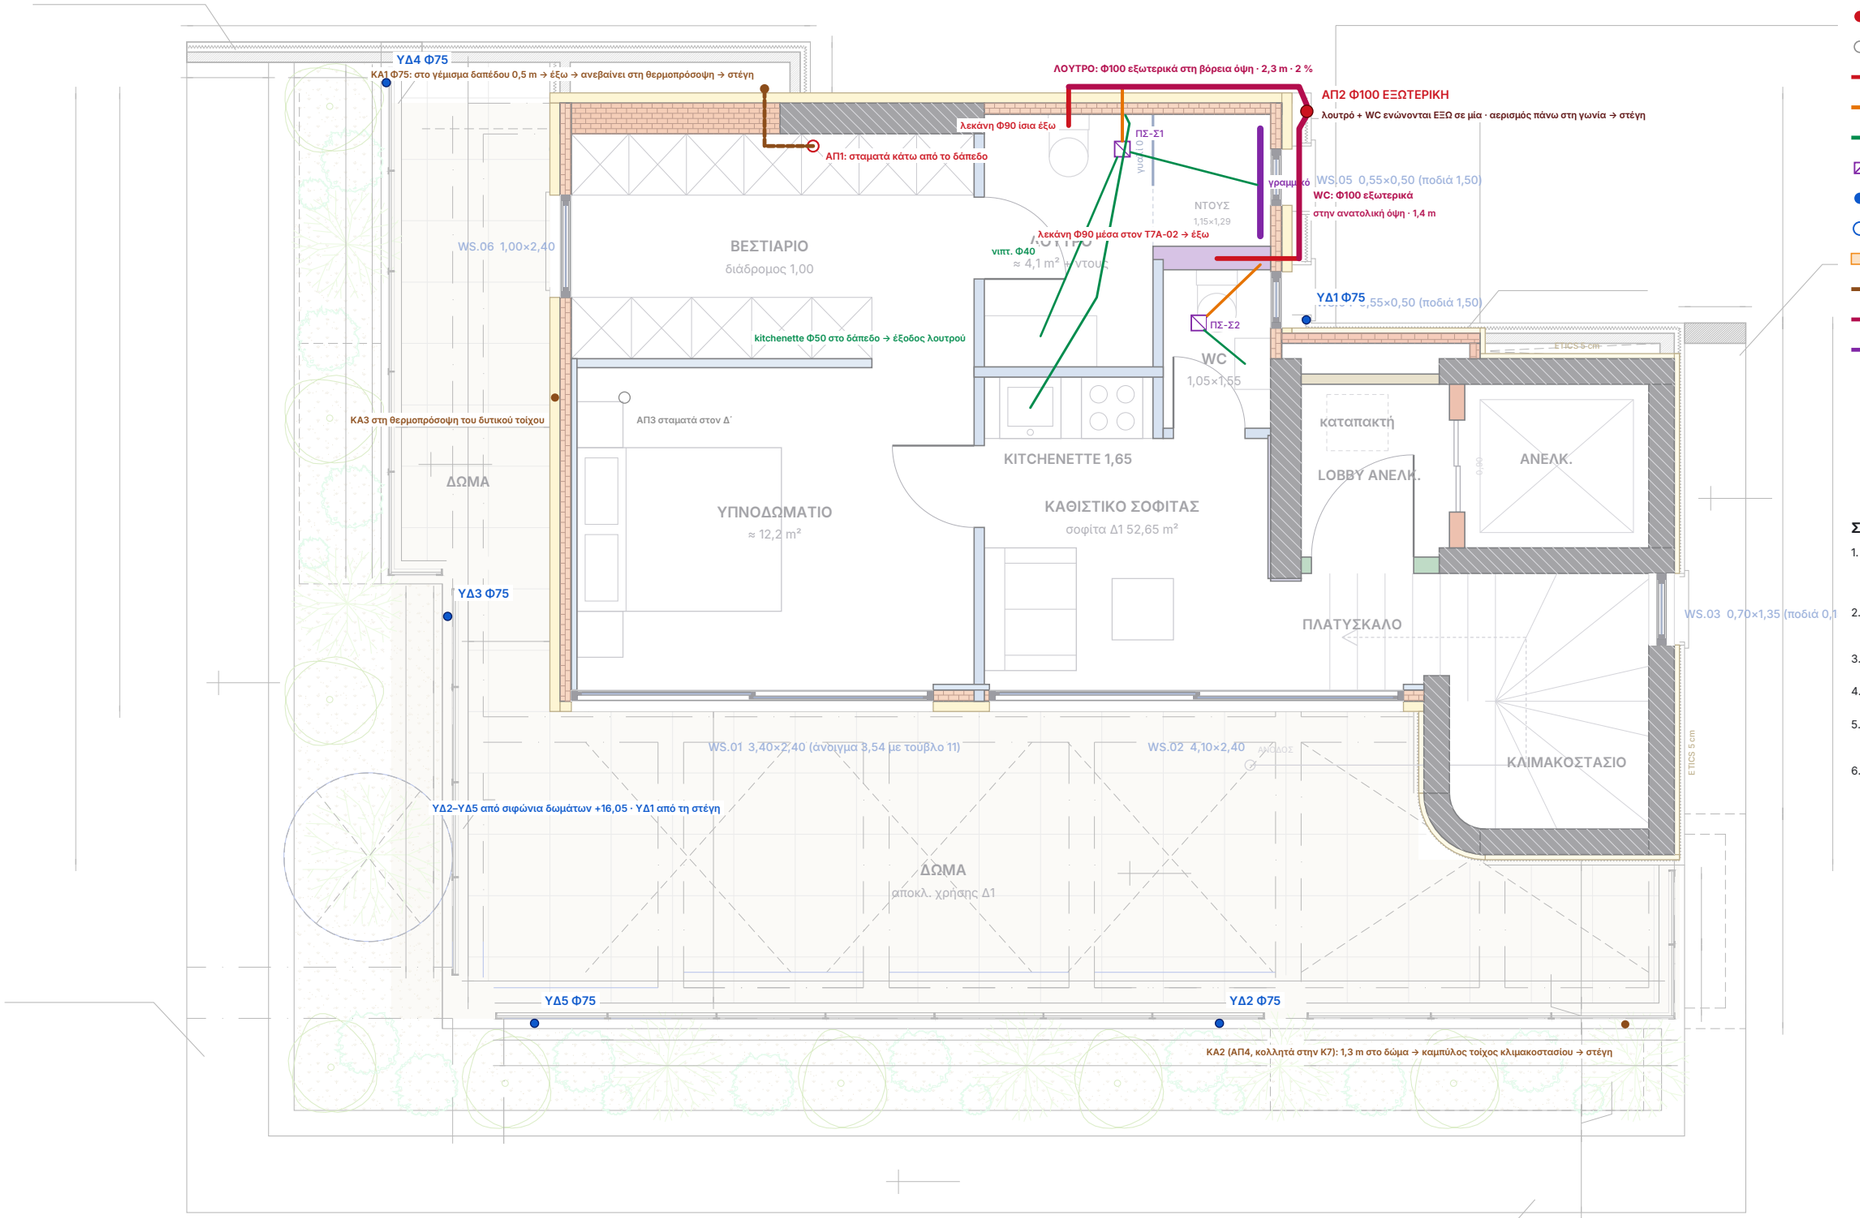

ΥΠΟΜΝΗΜΑ

- Στήλη λυμάτων ΑΠ (Φ100 / ΑΠ4 Φ75) · αερισμός συνεχίζει
- Θέση R14 όπου μετακινήθηκε (διακεκομμένη)
- Λεκάνη → στήλη Φ90 / Φ100
- Ποτισόφωνο / σιφώνι → στήλη Φ50–Φ75
- Ντους / πλυντήριο Φ50 · νιπτήρας Φ40 · νεροχύτης Φ50
- Ποτισόφωνο ΠΣ (σιφώνι δαπέδου)
- Υδρορροή ΥΔ Φ75 μέσα στη θερμοπρόσοψη (αναμονή Φ125)
- Σιφώνι ομβρίων εξώστη · διακεκ. = πλευρική έξοδος
- Δοκός (Σ4/Σ5) – καμία οπή
- Αερισμός ΚΑ – βγαίνει έξω, ανεβαίνει στη θερμοπρόσοψη
- Εξωτερικός αγωγός Φ100 σοφίτας (σε κούτελο θερμοπρόσοψης)
- Γραμμικό σιφώνι ντους

ΣΗΜΕΙΩΣΕΙΣ ΣΟΦΙΤΑΣ – R15

1. ΑΠ1: δεν ανεβαίνει στη σοφίτα. Ο αερισμός ΚΑ1 φεύγει μέσα στο γέμισμα του δαπέδου, βγαίνει έξω δυτικά του Κ2 και ανεβαίνει στη θερμοπρόσοψη – όπως η ΑΠ3 (ΚΑ3).
2. ΛΟΥΤΡΟ: δική του έξοδος από τον βόρειο τοίχο (λεκάνη Φ90 + ΠΣ-Σ1 Φ75). Η kitchenette μπαίνει στην ίδια έξοδο.
3. WC: δική του έξοδος από τον ανατολικό τοίχο (λεκάνη Φ90 μέσα στον Τ7Α-02 + ΠΣ-Σ2).
4. Οι δύο έξοδοι ενώνονται ΕΞΩ από το κτίριο στη ΒΑ γωνία → ΑΠ2 Φ100 εξωτερική ως το υπόγειο.
5. Οι εξωτερικοί αγωγοί τρέχουν στη στάθμη της πλάκας +16,05 και κλείνονται με κούτελο θερμοπρόσοψης.
6. Όλοι οι αερισμοί έξω (ΚΑ1, ΑΠ2, ΚΑ2, ΚΑ3) – κανένας σε οροφή.

ΕΡΓΟ	ΘΕΜΑ ΣΧΕΔΙΟΥ	ΒΑΣΗ	ΑΡ. ΣΧΕΔΙΟΥ
ΠΕΝΤΑΟΡΟΦΟ ΚΤΗΡΙΟ ΚΑΤΟΙΚΙΩΝ – ΑΡΓΥΡΟΥΠΟΛΗ Κωνσταντινουπόλεως 12 & Αγ. Βαρβάρας · Ο.Τ. 103-15 Εργοδότης: INTERKAT Α.Ε. · Κατασκευή: ARKAD Ι.Κ.Ε.	**ΣΟΦΙΤΑ – ΑΠΟΧΕΤΕΥΣΗ & ΑΕΡΙΣΜΟΙ** R15 · σχόλια 10/11/2026 · λύματα · αερισμοί · όμβρια ΣΟΦΙΤΑ – Δ1 πάνω επίπεδο	R14 · Σ7 / Σ8 · τοιχοποιίες σοφίτας R04	**ΑΠ-05** **Κλίμακα 1:60 · Α3** 10/11/2026 · R15

ΑΛΛΑΓΕΣ R14 → R15 (σχόλια Γιάννη 10/11/2026)

Στοιχείο	R14	R15	Λόγος / έλεγχος
Λουτρό ισογείου	δική του πτώση 4,55 / 2,00 στο υπόγειο	ενώνεται με την ΑΠ1: λεκάνη Φ90 + ΠΣ-Ι1 μέσα στον Τ7-01	«το λουτρό να το ενώσουμε με την ΑΠ1»
Γραμμικό ντους ισογείου	στην είσοδο του ντους (y 1,55)	στον δυτικό τοίχο του ντους, 0,2 m από την ΑΠ1 (όπως οι όροφοι)	«βάλε το γραμμικό σωστά» – κλειστή πλευρά, μία κλίση
WC ισογείου	πτώση 9,27 / 5,35 στην παρειά του Τ7-02	κούτελο 23×23 δίπλα στη λεκάνη, πτώση 9,29 / 5,74	κάτω από τον Τ7-02 είναι η Δ9.1 30/50 (Σ2) – καμία οπή σε δοκό
WC + κουζίνα ΙΣ1	κλάδος x 9,27	ένας κοινός κλάδος x 9,29 στο υπόγειο	«να ενωθούν με της κουζίνας»
ΑΠ4 όροφοι	13,35 / 9,69 στη μέση του κενού	12,87 / 9,51 κολλητά στη νότια παρειά της Κ7	«κολλητά με την κολόνα, όχι στον αέρα»
ΑΠ4 ισόγειο	σόφιτο +3,20 γύρω από την κολόνα → κουτί 35×35	κολλητά στην Κ7 → τούβλο Τ1-11 δίπλα της → κούτελο 26×28 στη γωνία της Κ7	έξω δεν κατεβαίνει: από κάτω Κ32 25/50, τοιχείο ράμπας και χαμηλή ζώνη (Σ2)
Βάση ΑΠ4 υπόγειο	12,92 / 8,97	12,60 / 9,05 (μηχανοστάσιο, πλάκα Π10)	ακολουθεί το νέο κούτελο
Αερισμός ΑΠ1 (ΚΑ1)	μέσα στη ντουλάπα βεστιαρίου ως +1,10	μέσα στο γέμισμα δαπέδου σοφίτας → έξω → ανεβαίνει	«βγαίνει μέσα από το δάπεδο έξω, όπως η ΑΠ3»
Λουτρό σοφίτας	→ ΑΠ1 (Φ90 2,5 m σε προτοίχο)	δική του έξοδος από τον βόρειο τοίχο	«το λουτρό και το WC θα έχουν δικές τους»
WC σοφίτας	→ ΑΠ2	δική του έξοδος από τον ανατολικό τοίχο	ίδιο
ΑΠ2	μόνο WC σοφίτας	λουτρό + WC σοφίτας ενώνονται έξω σε μία	«θα ενωθούν σε μία έξω από το κτίριο»

ΑΝΟΙΚΤΑ – απάντησε με τον αριθμό (π.χ. «1 κουτί, 3 ΟΚ, 9 ναι»)

Νο	Θέμα	Πρόταση	Ερώτηση
1	ΑΠ3 στο ισόγειο	Αντί για σόφιτο 1,3 m στο Υπν.1, κουτί 20×20 στη θέση 3,08 / 3,38 μέσα στη γωνία ντουλάπας–τοίχου ισογείου.	Σόφιτο ή κουτί;
3	Ντους γονέων	Το ΠΣ2 πάει δίπλα στο γυαλί (1,25 / 4,30): ντους Φ50 0,9 m αντί 2,4 m, και ΠΣ2 → ΑΠ3 Φ75 μέσα στον Τ7-02.	ΟΚ;
4	Κλίση ομβρίων +3,30	31 m με 0,5 % είναι οριακό για φύλλα. Πρόταση 1 % (πτώση 0,31 m) ή δεύτερη κάθοδος στη ΒΔ γωνία.	Ποιο;
5	Ύψος υπογείου	Ο συλλεκτήρας δίνει 2,16 πάνω από Θ.Σ.Υ. 3/4. Πρόταση: ο νότιος κλάδος κολλητά στο δυτικό τοιχείο (x –1,10).	ΟΚ;
6	Ηχομόνωση στηλών	ΑΠ1 και ΑΠ3 περνούν δίπλα σε υπνοδωμάτια: ηχομονωτικός σωλήνας τύπου PP 3 στρώσεων αντί U-PVC.	ΟΚ;
7	Υδρορροές στη θερμοπρόσοψη	Φ75 σε ETICS 10 cm αφήνει 2,5 cm μόνωση: τοπικά ETICS 12 cm ή υδρορροή Φ63.	Ποιο;
8	ΑΠ4 κουζίνες	Φ75 επαρκεί για 4 κουζίνες. Πρόταση Φ90 για λίπη, ίδια θέση κολλητά στην Κ7.	Φ75 ή Φ90;
9	ΑΠ4 – θέση οπής	Την έβαλα στη ΔΥΤΙΚΗ άκρη της νότιας παρειάς της Κ7 (12,87 / 9,51), ώστε στο ισόγειο να περνά από το τούβλο δίπλα στην κολόνα. Ο Σ3 δεν δείχνει οπή στην πλάκα του έρκερ.	Εκεί είναι η οπή στο έργο;
10	ΚΑ1 στο δάπεδο σοφίτας	Φ75 μέσα σε γέμισμα 15 cm με ενδοδαπέδια είναι σφιχτό. Πρόταση: εγκοπή στη θερμομόνωση του δαπέδου ή Φ63.	Φ75 ή Φ63;
11	Εξωτερικοί αγωγοί σοφίτας	Το Φ100 του λουτρού φαίνεται 2,3 m στη βόρεια όψη στη στάθμη +16,05. Πρόταση: ζώνη-κούτελο θερμοπρόσοψης 20×20 σε όλο το μήκος.	ΟΚ το κούτελο;