
ΟΡΟΦΗ ΥΠΟΓΕΙΟΥ – ΣΥΛΛΕΚΤΗΡΑΣ ΛΥΜΑΤΩΝ

Κλίμακα 1:80

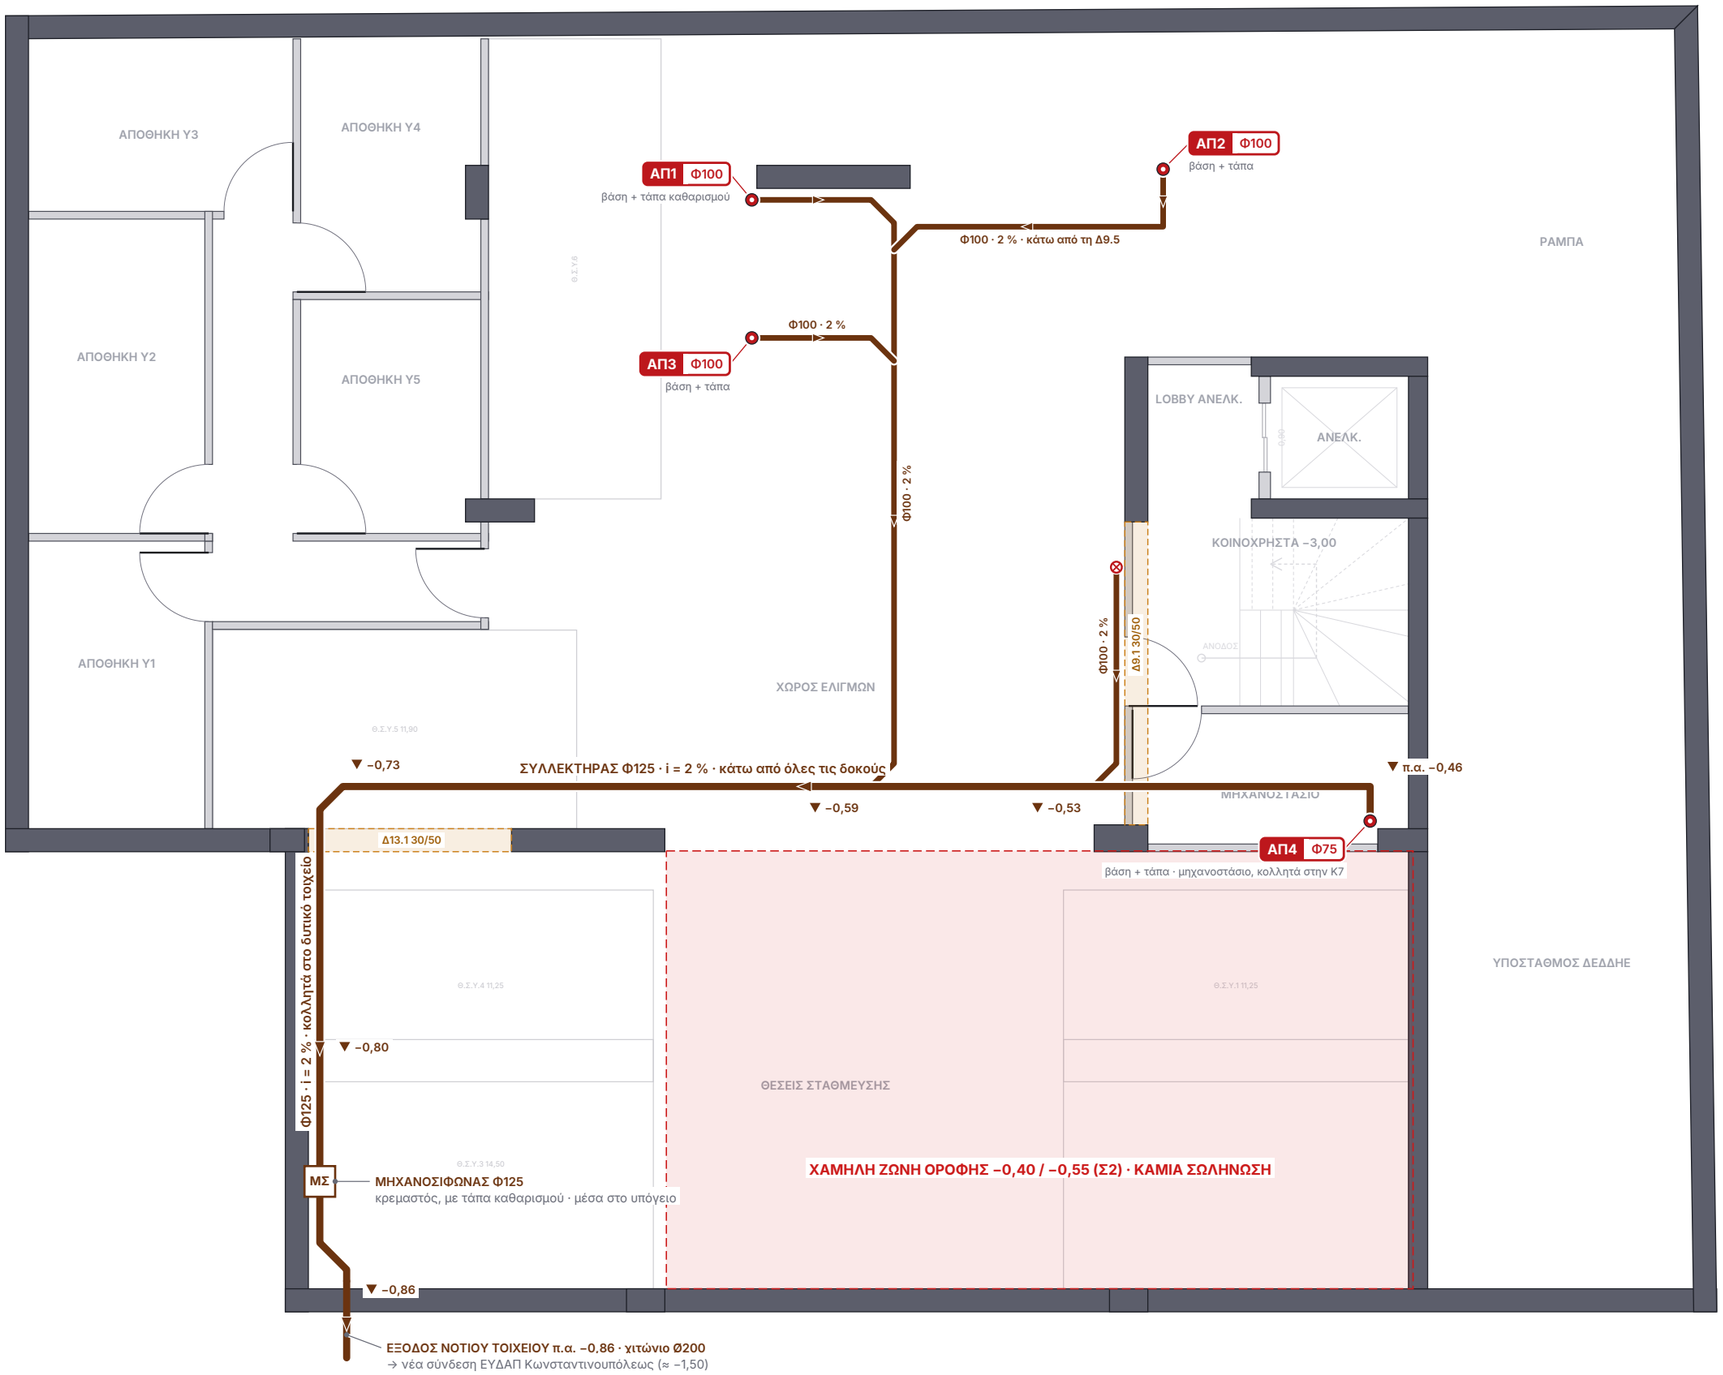


ΥΠΟΜΝΗΜΑ

- Συλλεκτήρας / κλάδοι υπογείου, κρεμαστοί κάτω από τις δοκούς
- Κατακόρυφη στήλη λυμάτων ΑΠ
- Πτώση στον κάτω όροφο
- Δοκός (ξυλότυποι Σ2–Σ7) – ΚΑΜΙΑ οπή
- Χαμηλή ζώνη οροφής υπογείου – καμία σωλήνωση

ΕΡΓΟ	ΘΕΜΑ ΣΧΕΔΙΟΥ	ΒΑΣΗ	ΑΡ. ΣΧΕΔΙΟΥ
ΠΕΝΤΑΟΡΟΦΟ ΚΤΗΡΙΟ ΚΑΤΟΙΚΙΩΝ – ΑΡΓΥΡΟΥΠΟΛΗ Κωνσταντινουπόλεως 12 & Αγ. Βαρβάρας · Ο.Τ. 103-15 Εργοδότης: INTERKAT Α.Ε. · Κατασκευή: ARKAD Ι.Κ.Ε.	**ΥΠΟΓΕΙΟ – ΣΥΛΛΕΚΤΗΡΑΣ ΛΥΜΑΤΩΝ** R18 · λύματα · ακάθαρτα · αερισμοί · όμβρια · οπές πλακών Οροφή υπογείου · συλλεκτήρας στο δυτικό τοιχείο · έξοδος −0,86	Σ2 εφαρμογής · τοιχοποιίες υπογείου R05	**ΑΠ-01** **Κλίμακα 1:80 · Α3** 10/11/2026 · R18

ΚΑΤΟΨΗ ΙΣΟΓΕΙΟΥ – ΑΠΟΧΕΤΕΥΣΗ & ΟΜΒΡΙΑ

Κλίμακα 1:60

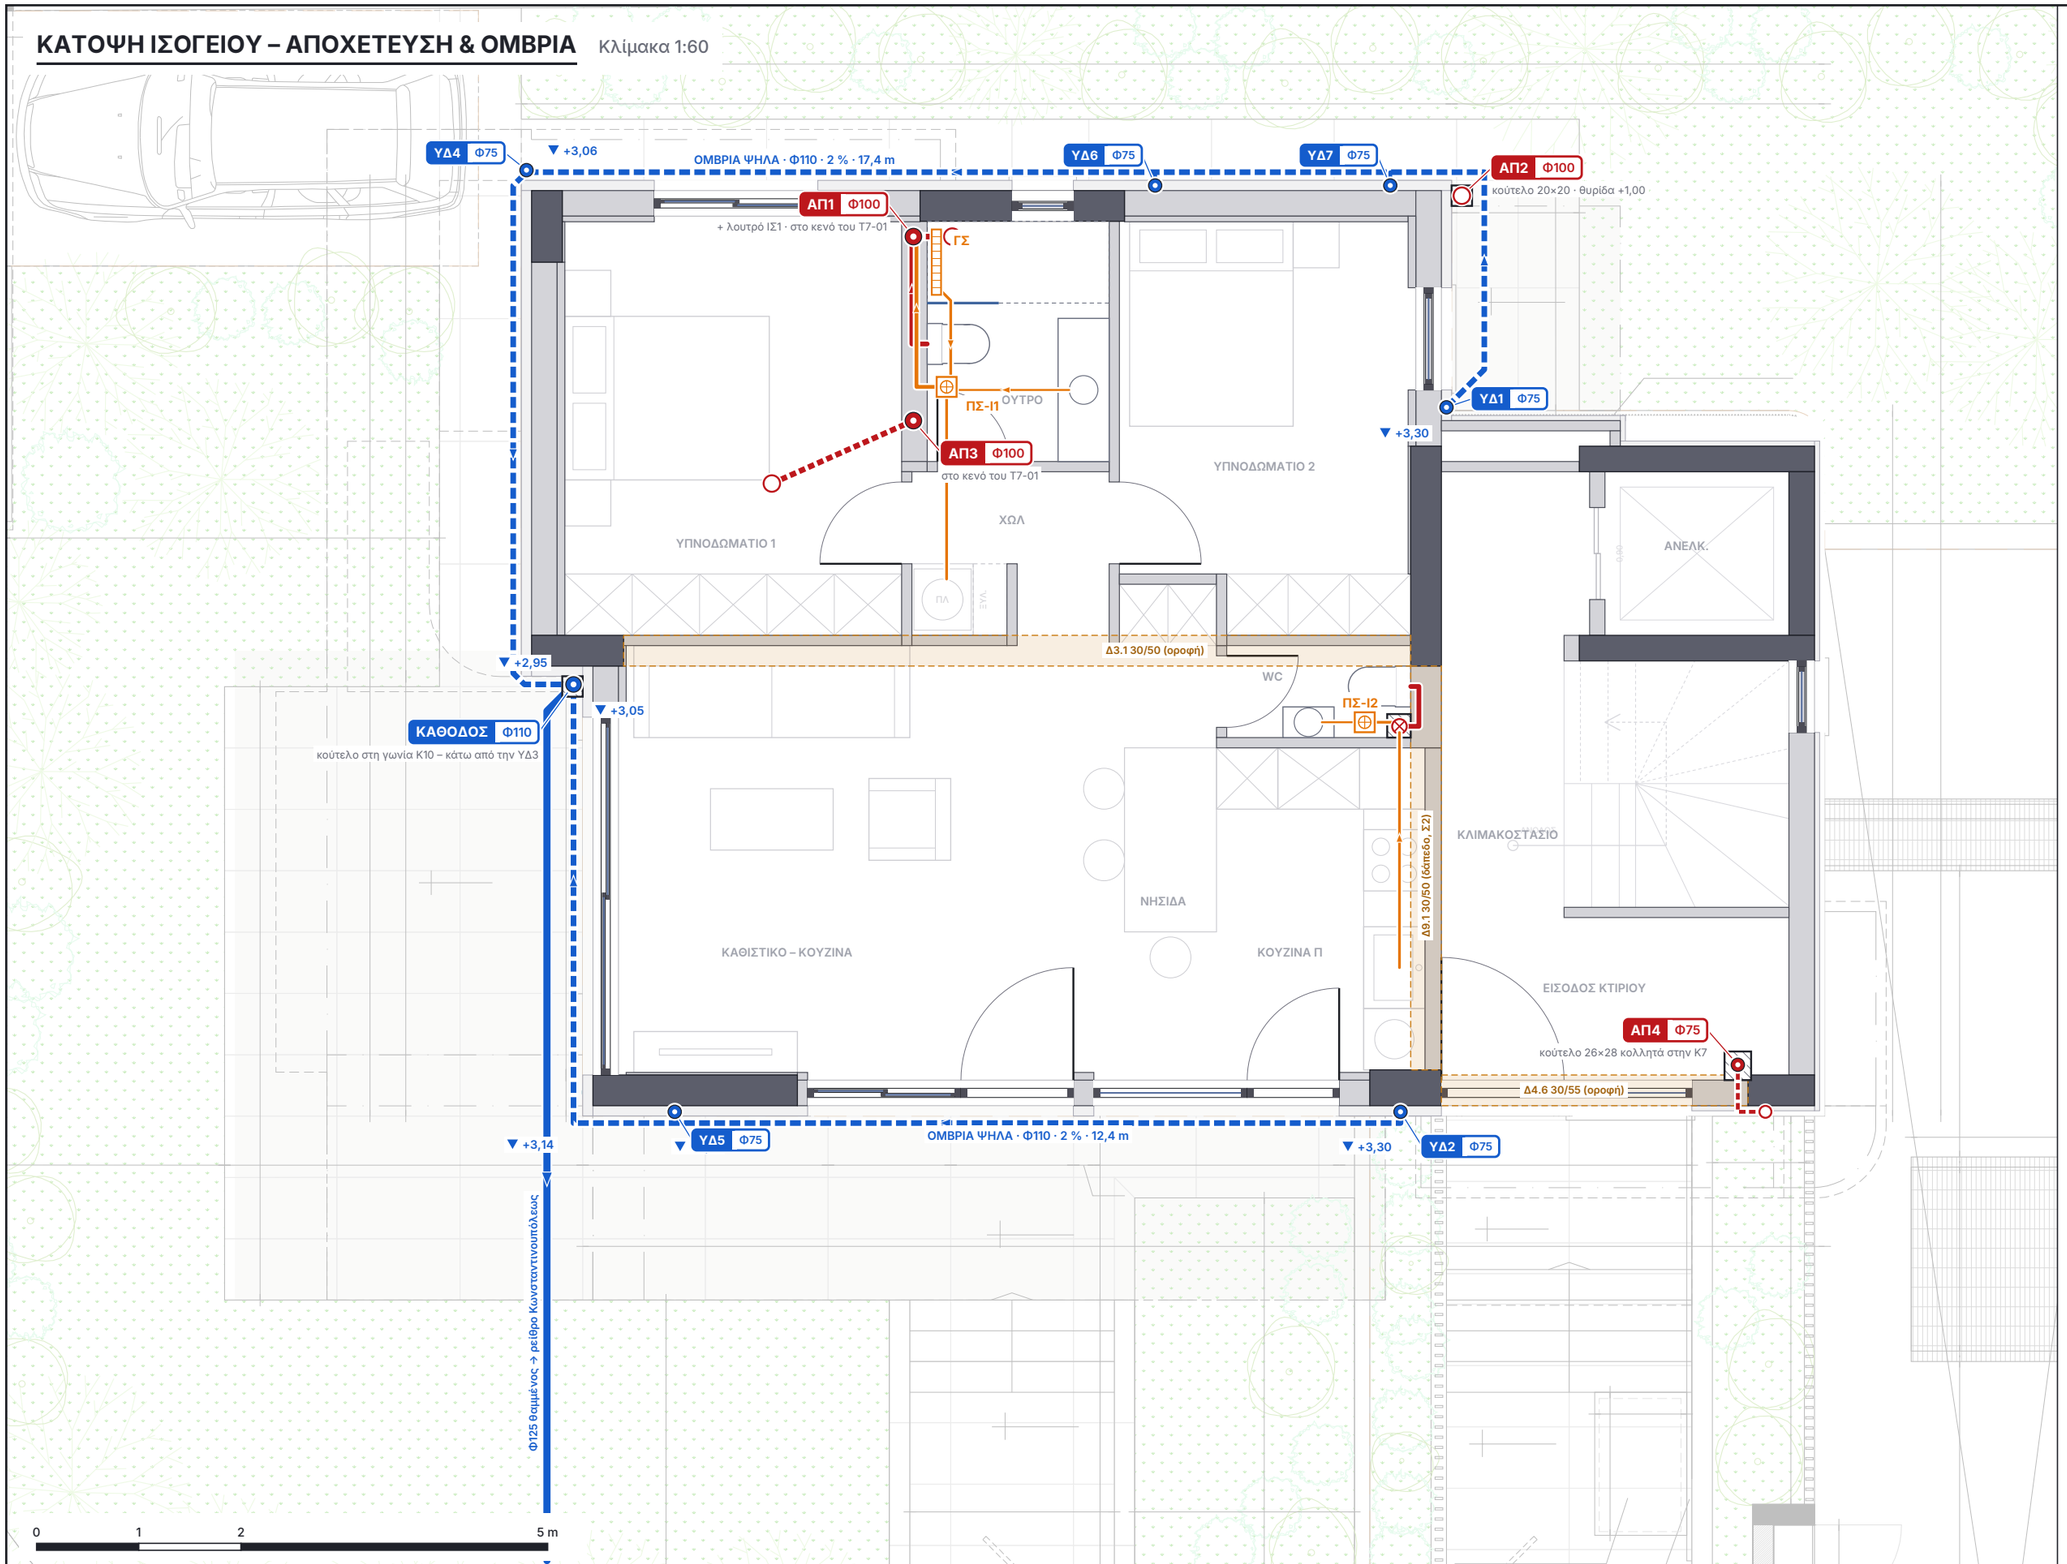


ΥΠΟΜΝΗΜΑ

- Λύματα: λεκάνη Φ90 · στήλη / αγωγός Φ100
- Ακάθαρτα: Φ40 νιπτήρας · Φ50 ντους, νεροχύτης, πλυντήριο · Φ75 έξοδος πατοσίφωνου
- Αγωγός στην οροφή του ορόφου (μετατόπιση στήλης 2×45°)
- Συλλεκτήρας ομβρίων ΨΗΛΑ +3,30 (οροφή προβόλων Α΄)
- Όμβρια: συλλεκτήρας / αγωγός
- Κατακόρυφη στήλη λυμάτων ΑΠ
- Στήλη που περνά / σταματά (χωρίς σύνδεση στον όροφο)
- Πτώση στον κάτω όροφο
- Πατοσίφωνο ΠΣ (σιφώνι δαπέδου με σχάρα)
- Γραμμικό σιφώνι ντους ΓΣ → πατοσίφωνο
- Κούτελο (κλειστό κανάλι γύρω από αγωγό)
- Υδρορροή ΥΔ Φ75 μέσα στη θερμοπρόσοψη
- Δοκός (Ευλότυποι Σ2–Σ7) – ΚΑΜΙΑ οπή

ΕΡΓΟ	ΘΕΜΑ ΣΧΕΔΙΟΥ	ΒΑΣΗ	ΑΡ. ΣΧΕΔΙΟΥ
ΠΕΝΤΑΟΡΟΦΟ ΚΤΗΡΙΟ ΚΑΤΟΙΚΙΩΝ – ΑΡΓΥΡΟΥΠΟΛΗ Κωνσταντινουπόλεως 12 & Αγ. Βαρβάρας · Ο.Τ. 103-15 Εργοδότης: INTERKAT Α.Ε. · Κατασκευή: ARKAD Ι.Κ.Ε.	**ΙΣΟΓΕΙΟ – ΑΠΟΧΕΤΕΥΣΗ & ΟΜΒΡΙΑ** R18 · λύματα · ακάθαρτα · αερισμοί · όμβρια · οπές πλακών ΑΠ1 / ΑΠ3 στο κενό του Τ7-01 · κούτελα WC / ΑΠ4 · όμβρια 2 % · λεπτομέρειες στο ΑΠ-06	Σ2 / Σ3 εφαρμογής · τοιχοποιίες ισογείου R13	**ΑΠ-02** **Κλίμακα 1:60 · Α3** 10/11/2026 · R18

ΚΑΤΟΨΗ Α΄ · Β΄ · Γ΄ ΟΡΟΦΟΥ (ΤΥΠΙΚΟΣ) – ΑΠΟΧΕΤΕΥΣΗ & ΥΔΡΟΡΡΟΕΣ

Κλίμακα 1:60

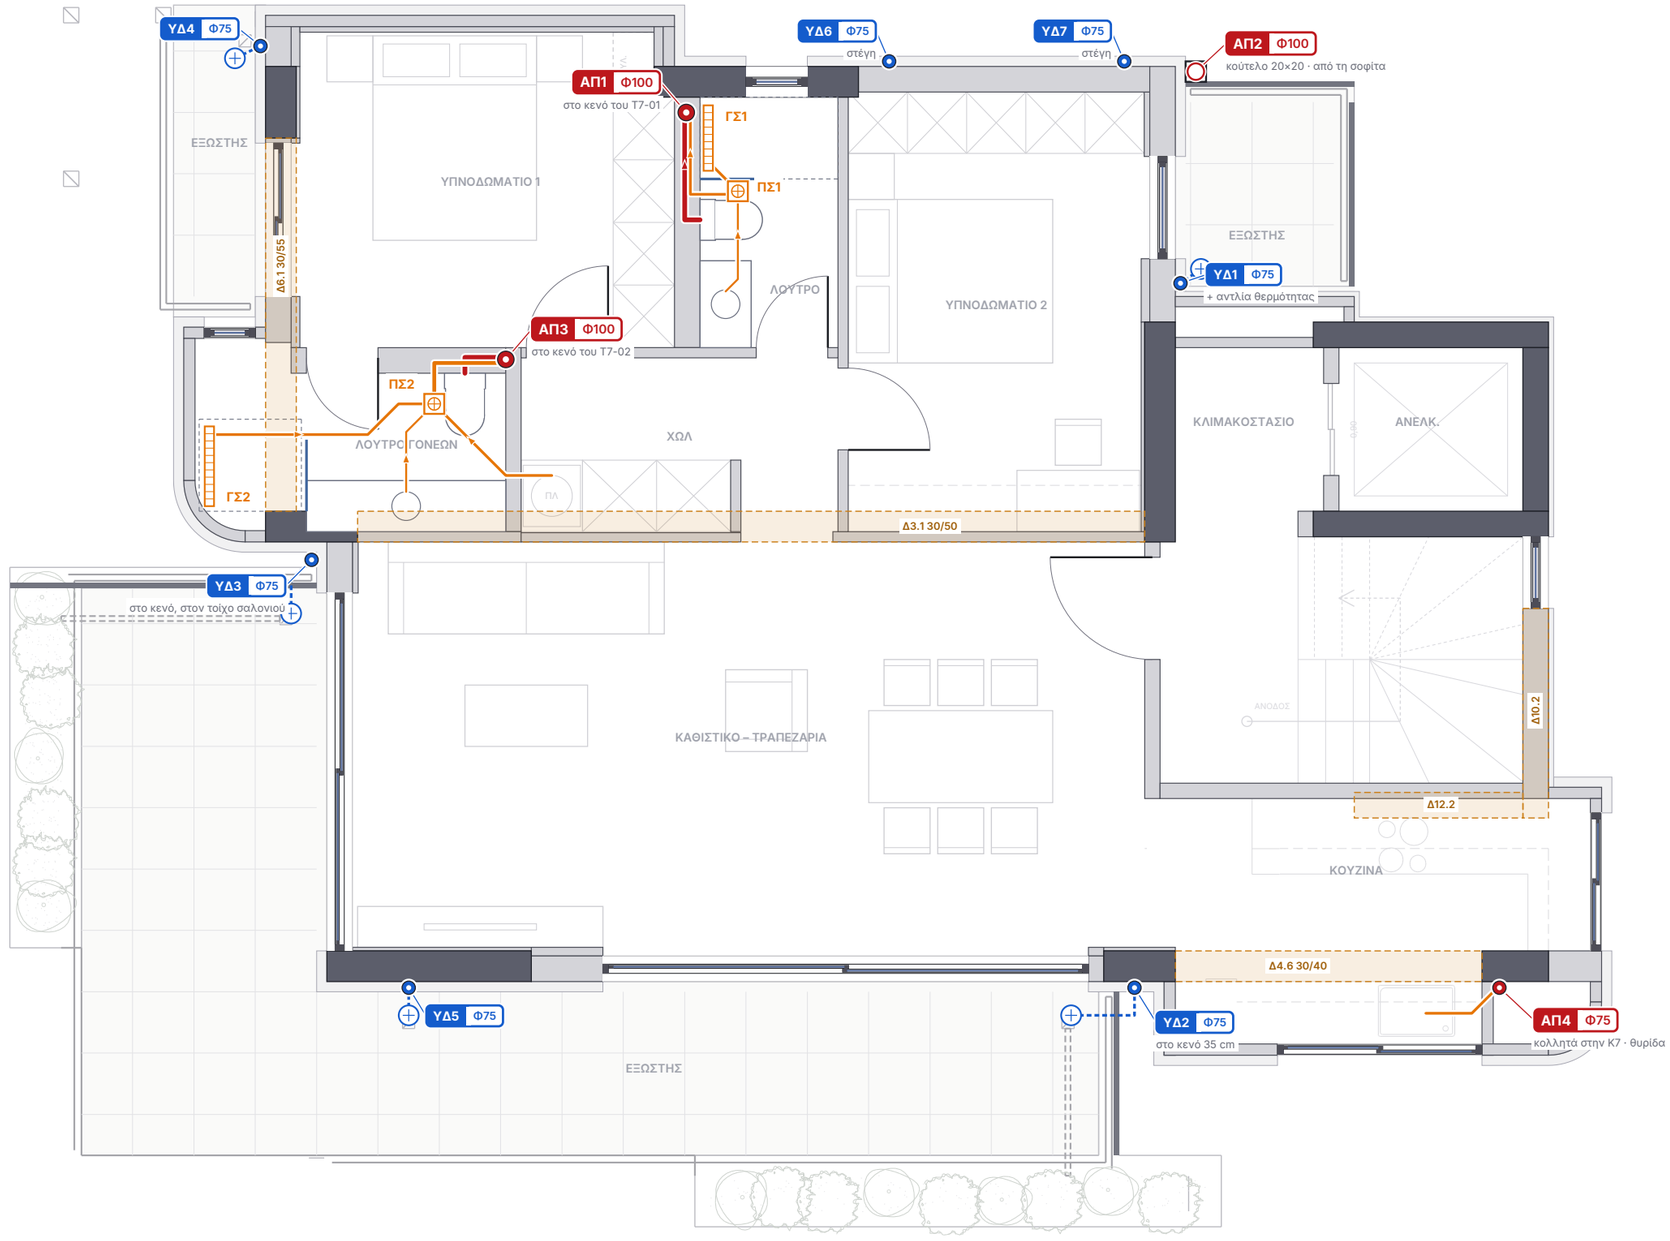


ΥΠΟΜΝΗΜΑ

- Λύματα: λεκάνη Φ90 · στήλη / αγωγός Φ100
- Ακάθαρτα: Φ40 νιπτήρας · Φ50 ντους, νεροχύτης, πλυντήριο · Φ75 έξοδος πατοσίφωνου
- Κατακόρυφη στήλη λυμάτων ΑΠ
- Στήλη που περνά / σταματά (χωρίς σύνδεση στον όροφο)
- Πατοσίφωνο ΠΣ (σιφώνι δαπέδου με σχάρα)
- Γραμμικό σιφώνι ντους ΓΣ → πατοσίφωνο
- Υδρορροή ΥΔ Φ75 μέσα στη θερμοπρόσοψη
- Σιφώνι ομβρίων εξώστη, πλευρική έξοδος
- Δοκός (ξυλότυποι Σ2–Σ7) – ΚΑΜΙΑ οπή

ΕΡΓΟ	ΘΕΜΑ ΣΧΕΔΙΟΥ	ΒΑΣΗ	ΑΡ. ΣΧΕΔΙΟΥ
ΠΕΝΤΑΟΡΟΦΟ ΚΤΗΡΙΟ ΚΑΤΟΙΚΙΩΝ – ΑΡΓΥΡΟΥΠΟΛΗ Κωνσταντινουπόλεως 12 & Αγ. Βαρβάρας · Ο.Τ. 103-15 Εργοδότης: INTERKAT Α.Ε. · Κατασκευή: ARKAD Ι.Κ.Ε.	**Α΄·Β΄·Γ΄ ΟΡΟΦΟΣ – ΑΠΟΧΕΤΕΥΣΗ** R18 · λύματα · ακάθαρτα · αερισμοί · όμβρια · οπές πλακών Τυπικός όροφος (Β1) · λεπτομέρειες στο ΑΠ-07	Σ4 / Σ5 · τοιχοποιίες τυπικού R25	**ΑΠ-03** **Κλίμακα 1:60 · Α3** 10/11/2026 · R18

ΚΑΤΟΨΗ Δ΄ ΟΡΟΦΟΥ – ΑΠΟΧΕΤΕΥΣΗ & ΥΔΡΟΡΡΟΕΣ

Κλίμακα 1:60

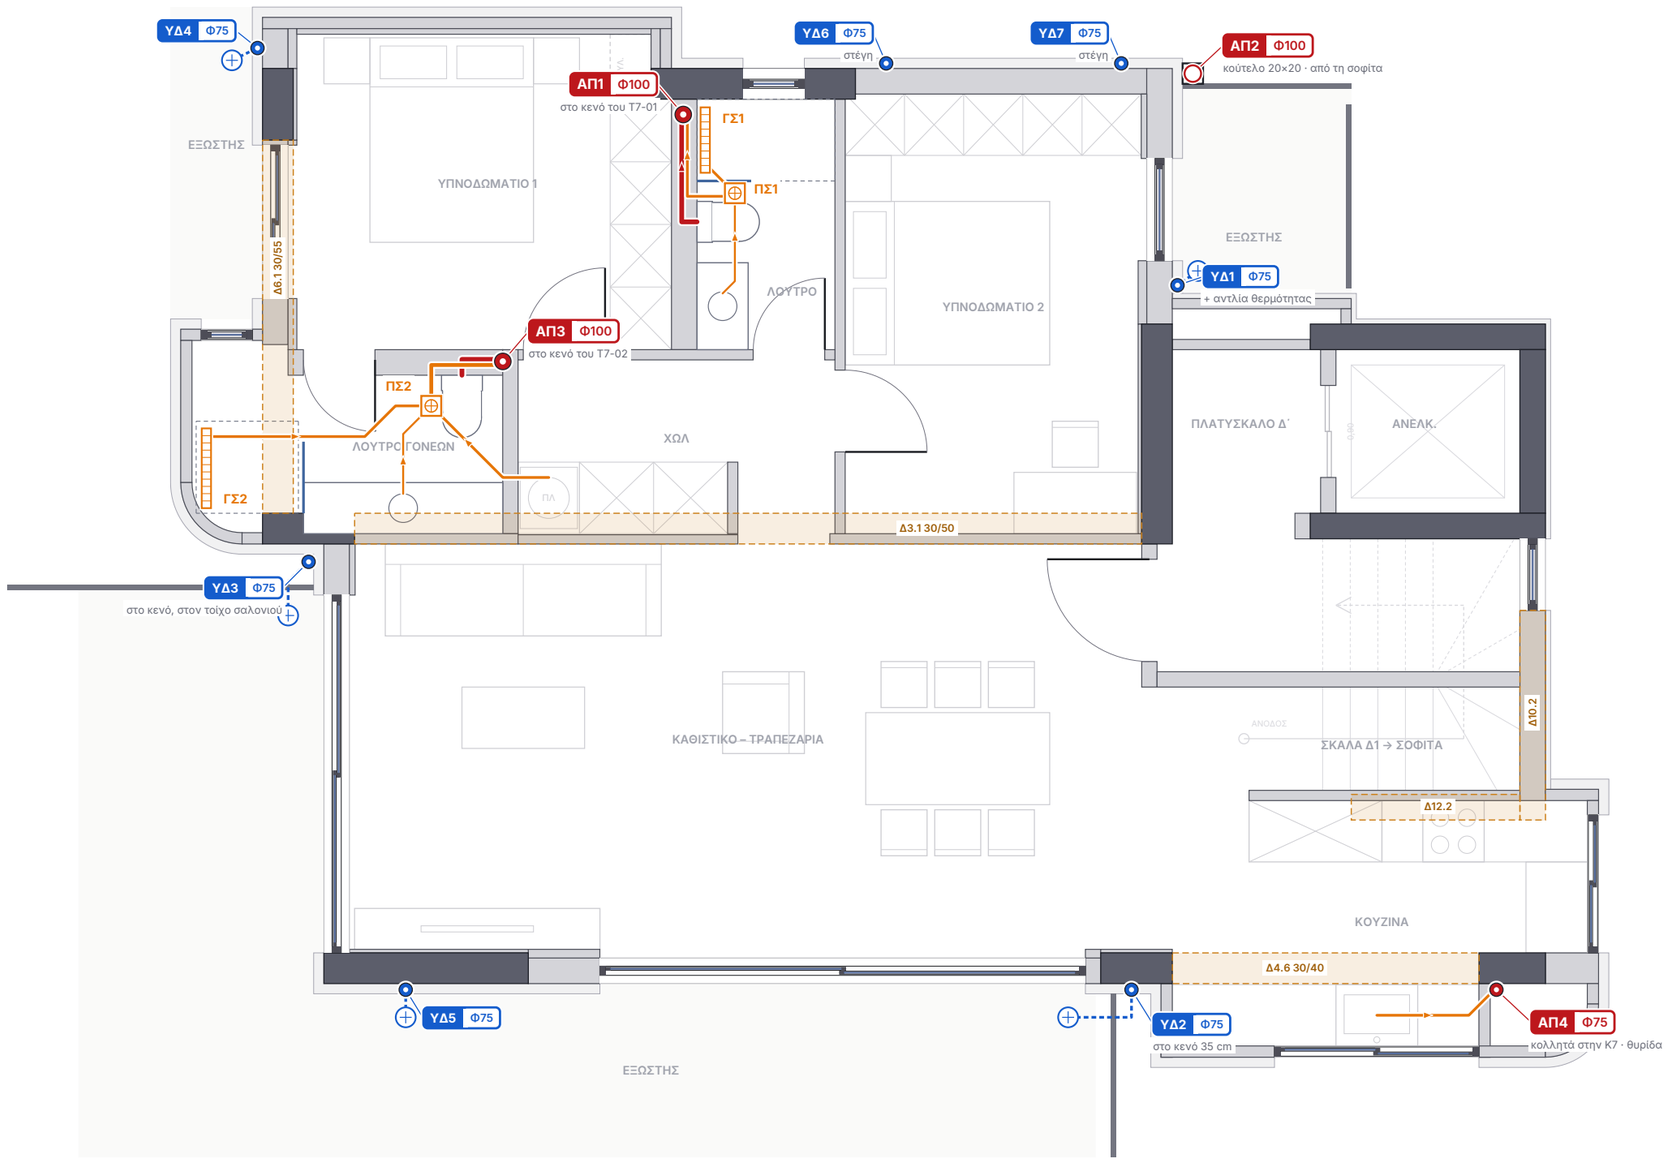

0 1 2 5 m

ΥΠΟΜΝΗΜΑ


- Λύματα: λεκάνη Φ90 · στήλη / αγωγός Φ100
- Ακάθαρτα: Φ40 νιπτήρας · Φ50 ντους, νεροχύτης, πλυντήριο · Φ75 έξοδος πατοσίφωνου
- Κατακόρυφη στήλη λυμάτων ΑΠ
- Στήλη που περνά / σταματά (χωρίς σύνδεση στον όροφο)
- Πατοσίφωνο ΠΣ (σιφώνι δαπέδου με σχάρα)
- Γραμμικό σιφώνι ντους ΓΣ → πατοσίφωνο
- Υδρορροή ΥΔ Φ75 μέσα στη θερμοπρόσοψη
- Σιφώνι ομβρίων εξώστη, πλευρική έξοδος
- Δοκός (ξυλότυποι Σ2–Σ7) – ΚΑΜΙΑ οπή
- Αερισμός ΚΑ Φ75 (βγαίνει έξω και ανεβαίνει στη θερμοπρόσοψη)

B

ΕΡΓΟ	ΘΕΜΑ ΣΧΕΔΙΟΥ	ΒΑΣΗ	ΑΡ. ΣΧΕΔΙΟΥ
ΠΕΝΤΑΟΡΟΦΟ ΚΤΗΡΙΟ ΚΑΤΟΙΚΙΩΝ – ΑΡΓΥΡΟΥΠΟΛΗ Κωνσταντινουπόλεως 12 & Αγ. Βαρβάρας · Ο.Τ. 103-15 Εργοδότης: INTERKAT Α.Ε. · Κατασκευή: ARKAD Ι.Κ.Ε.	**Δ΄ ΟΡΟΦΟΣ – ΑΠΟΧΕΤΕΥΣΗ** R18 · λύματα · ακάθαρτα · αερισμοί · όμβρια · οπές πλακών Δ1 κάτω επίπεδο · λουτρά όπως ο τυπικός (ΑΠ-07)	Σ7 · τοιχοποιίες Δ΄ R04	**ΑΠ-04** **Κλίμακα 1:60 · Α3** 10/11/2026 · R18

ΚΑΤΟΨΗ ΣΟΦΙΤΑΣ – ΑΠΟΧΕΤΕΥΣΗ & ΑΕΡΙΣΜΟΙ

Κλίμακα 1:60

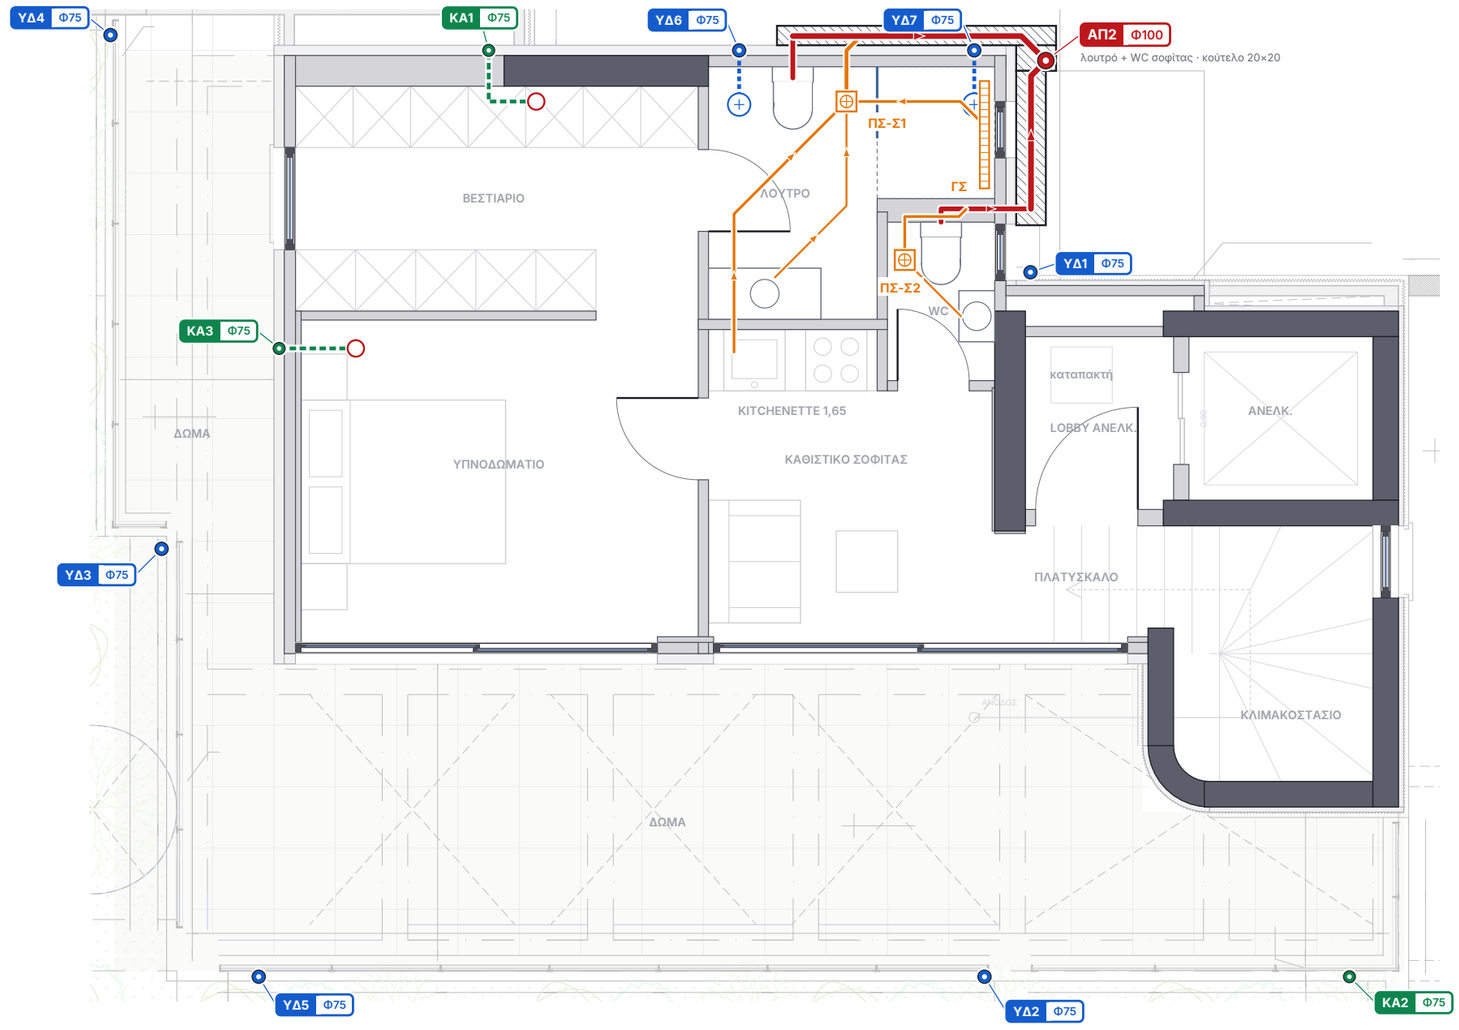

0 1 2 5 m

ΥΠΟΜΝΗΜΑ

- Λύματα: λεκάνη Φ90 · στήλη / αγωγός Φ100
- Ακάθαρτα: Φ40 νιπτήρας · Φ50 ντους, νεροχύτης, πλυντήριο · Φ75 έξοδος πατοσίφωνου
- Αερισμός ΚΑ Φ75 (βγαίνει έξω και ανεβαίνει στη θερμοπρόσοψη)
- Κατακόρυφη στήλη λυμάτων ΑΠ
- Στήλη που περνά / σταματά (χωρίς σύνδεση στον όροφο)
- Πατοσίφωνο ΠΣ (σιφώνι δαπέδου με σχάρα)
- Γραμμικό σιφώνι ντους ΓΣ → πατοσίφωνο
- Κούτελο (κλειστό κανάλι γύρω από αγωγό)
- Άνοδος αερισμού στη θερμοπρόσοψη
- Υδρορροή ΥΔ Φ75 μέσα στη θερμοπρόσοψη

B

ΕΡΓΟ

ΠΕΝΤΑΟΡΟΦΟ ΚΤΗΡΙΟ ΚΑΤΟΙΚΙΩΝ – ΑΡΓΥΡΟΥΠΟΛΗ
Κωνσταντινουπόλεως 12 & Αγ. Βαρβάρας · Ο.Τ. 103-15
Εργοδότης: INTERKAT Α.Ε. · Κατασκευή: ARKAD Ι.Κ.Ε.

ΘΕΜΑ ΣΧΕΔΙΟΥ

ΣΟΦΙΤΑ – ΑΠΟΧΕΤΕΥΣΗ & ΑΕΡΙΣΜΟΙ
R18 · λύματα · ακάθαρτα · αερισμοί · όμβρια · οπές πλακών
Δ1 πάνω επίπεδο · έξοδοι λουτρού / WC · κούτελα · λεπτομέρεια στο ΑΠ-08

ΒΑΣΗ


A-10-S · A-30-ΒΒ · Σ7 / Σ8 · τοιχοποιίες σοφίτας R04

ΑΡ. ΣΧΕΔΙΟΥ


ΑΠ-05
Κλίμακα 1:60 · Α3
10/11/2026 · R18

ΙΣΟΓΕΙΟ – ΛΕΠΤΟΜΕΡΕΙΕΣ ΥΓΡΩΝ ΧΩΡΩΝ


Κλίμακα 1:25

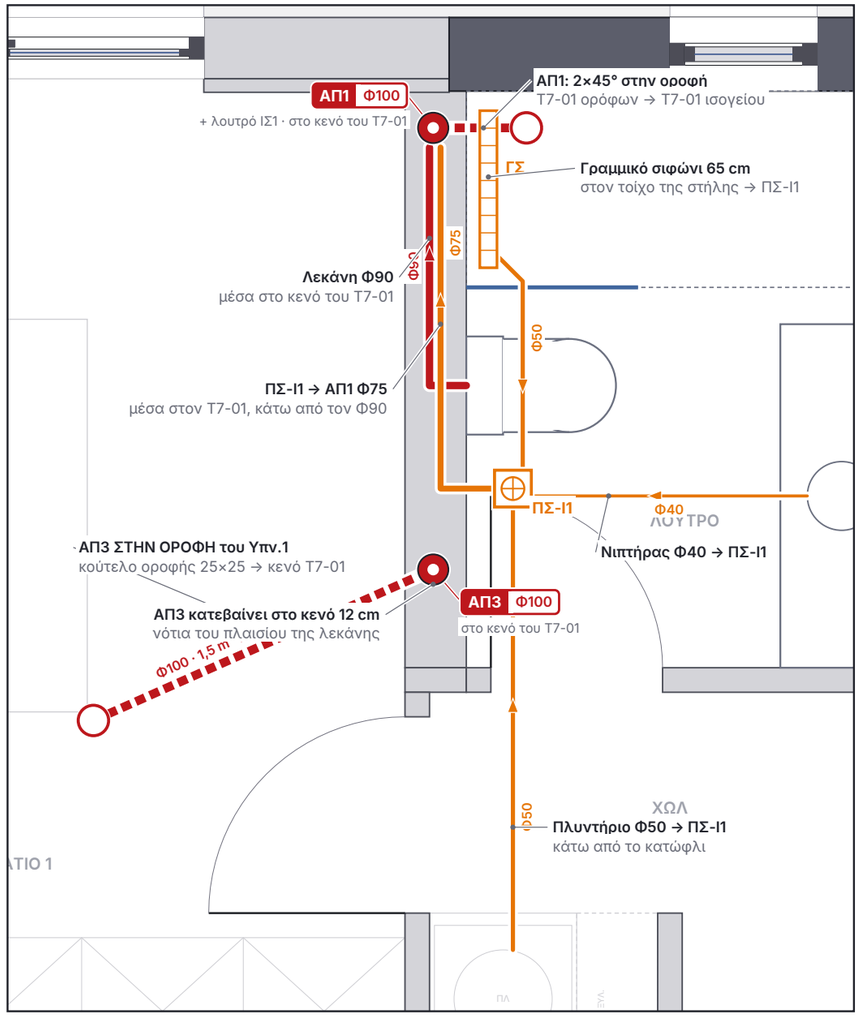

1 ΛΟΥΤΡΟ ΙΣΟΓΕΙΟΥ → ΑΠ1 · ΑΠ3 ΣΤΟ ΚΕΝΟ ΤΟΥ Τ7-01 Κλίμακα 1:25

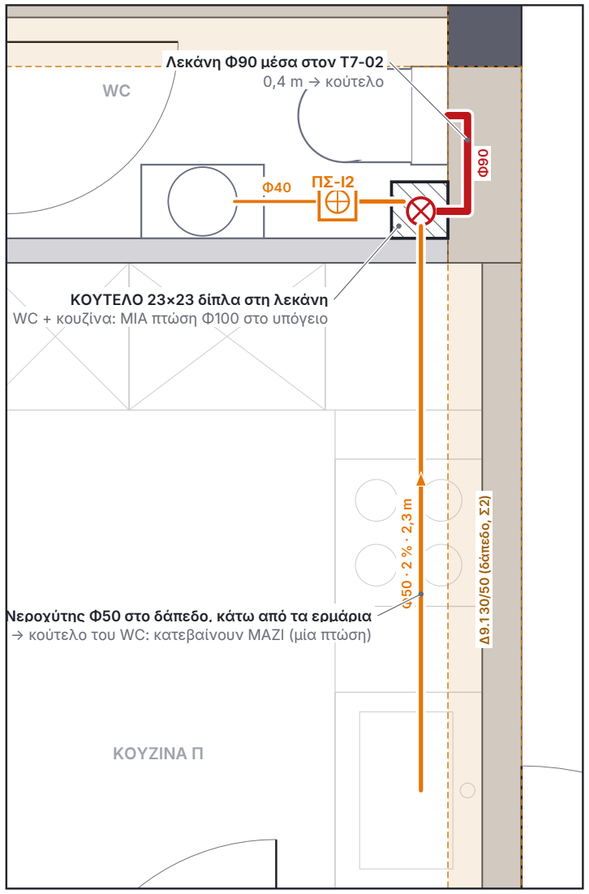

2 WC + ΚΟΥΖΙΝΑ – ΚΟΥΤΕΛΟ Κλίμακα 1:25

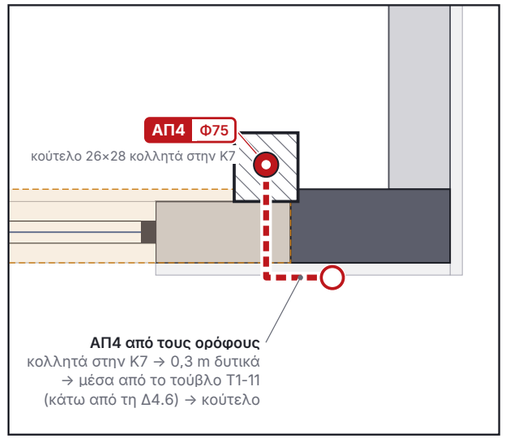

3 ΑΠ4 ΣΤΗΝ Κ7 Κλίμακα 1:25

ΥΠΟΜΝΗΜΑ


- Λύματα: λεκάνη Φ90 · στήλη / αγωγός Φ100
- Ακάθαρτα: Φ40 νιπτήρας · Φ50 ντους, νεροχύτης, πλυντήριο · Φ75 έξοδος πατοσίφωνου
- Αγωγός στην οροφή του ορόφου (μετατόπιση στήλης 2×45°)
- Κατακόρυφη στήλη λυμάτων ΑΠ
- Στήλη που περνά / σταματά (χωρίς σύνδεση στον όροφο)
- Πτώση στον κάτω όροφο
- Πατοσίφωνο ΠΣ (σιφώνι δαπέδου με σχάρα)
- Γραμμικό σιφώνι ντους ΓΣ → πατοσίφωνο
- Κούτελο (κλειστό κανάλι γύρω από αγωγό)
- Δοκός (ξυλότυποι Σ2–Σ7) – ΚΑΜΙΑ οπή

B


ΕΡΓΟ	ΘΕΜΑ ΣΧΕΔΙΟΥ	ΒΑΣΗ	ΑΡ. ΣΧΕΔΙΟΥ
ΠΕΝΤΑΟΡΟΦΟ ΚΤΗΡΙΟ ΚΑΤΟΙΚΙΩΝ – ΑΡΓΥΡΟΥΠΟΛΗ Κωνσταντινουπόλεως 12 & Αγ. Βαρβάρας · Ο.Τ. 103-15 Εργοδότης: INTERKAT Α.Ε. · Κατασκευή: ARKAD Ι.Κ.Ε.	**ΙΣΟΓΕΙΟ – ΛΕΠΤΟΜΕΡΕΙΕΣ ΥΓΡΩΝ ΧΩΡΩΝ** R18 · λύματα · ακάθαρτα · αερισμοί · όμβρια · οπές πλακών Λουτρό · WC / κουζίνα · ΑΠ4 στην Κ7	ΑΠ-02 · τοιχοποιίες ισογείου R13	**ΑΠ-06** **Κλίμακα 1:25 · Α3** 10/11/2026 · R18

Α΄ · Β΄ · Γ΄ · Δ΄ ΟΡΟΦΟΣ – ΛΕΠΤΟΜΕΡΕΙΕΣ ΥΓΡΩΝ ΧΩΡΩΝ


Κλίμακα 1:25

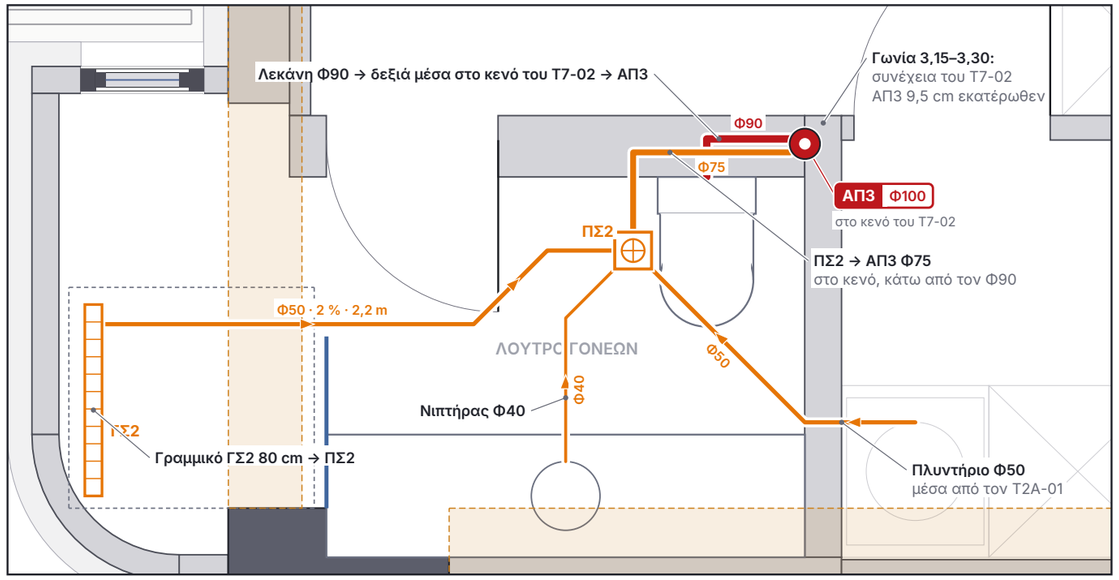


1 ΛΟΥΤΡΟ ΓΟΝΕΩΝ → ΑΠ3 Κλίμακα 1:25

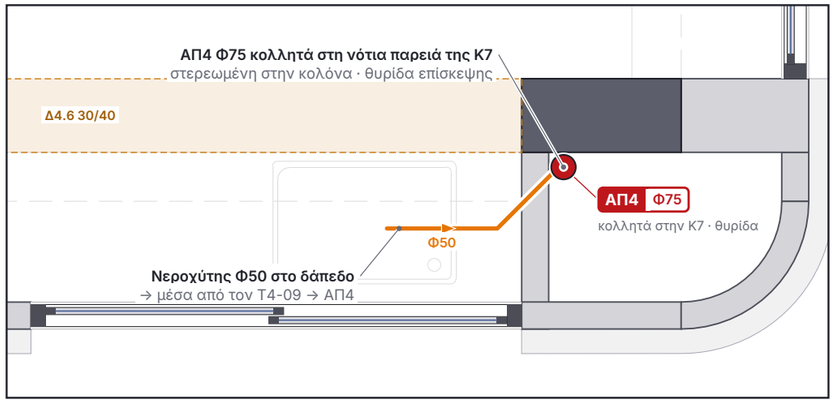


3 ΚΟΥΖΙΝΑ → ΑΠ4 ΚΟΛΛΗΤΑ ΣΤΗΝ Κ7 Κλίμακα 1:25

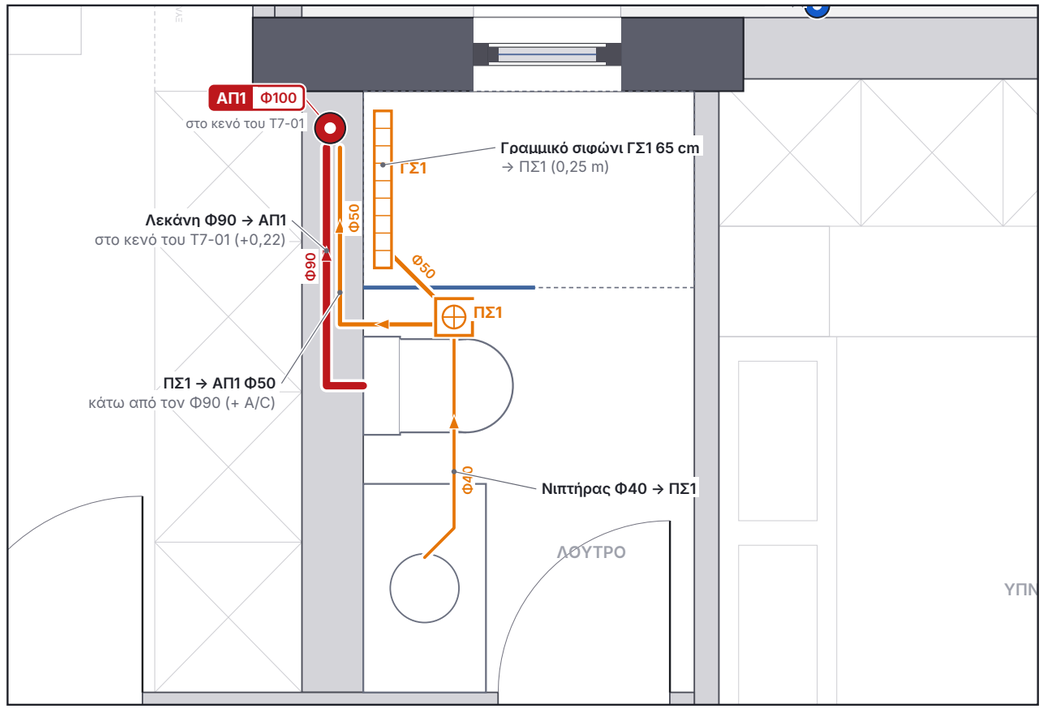

2 ΛΟΥΤΡΟ → ΑΠ1 Κλίμακα 1:25

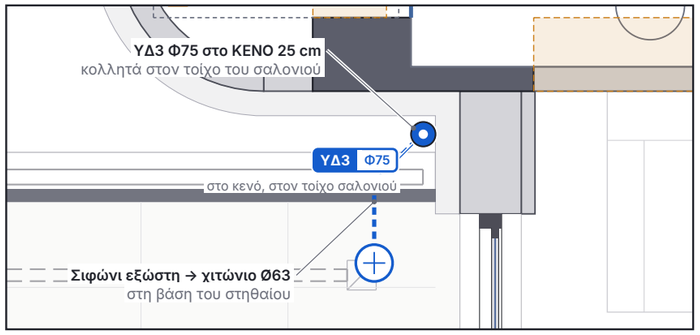

4 ΥΔ3 ΣΤΟ ΚΕΝΟ 25 cm – ΣΤΟΝ ΤΟΙΧΟ ΤΟΥ ΣΑΛΟΝΙΟΥ Κλίμακα 1:25

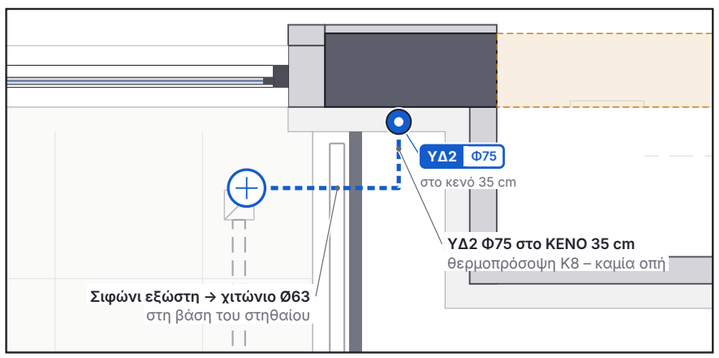

5 ΥΔ2 ΣΤΟ ΚΕΝΟ 35 cm (Κ8) Κλίμακα 1:25

ΥΠΟΜΝΗΜΑ


- Λύματα: λεκάνη Φ90 · στήλη / αγωγός Φ100
- Ακάθαρτα: Φ40 νιπτήρας · Φ50 ντους, νεροχύτης, πλυντήριο · Φ75 έξοδος πατοσίφωνου
- Κατακόρυφη στήλη λυμάτων ΑΠ
- Στήλη που περνά / σταματά (χωρίς σύνδεση στον όροφο)
- Πατοσίφωνο ΠΣ (σιφώνι δαπέδου με σχάρα)
- Γραμμικό σιφώνι ντους ΓΣ → πατοσίφωνο
- Υδρορροή ΥΔ Φ75 μέσα στη θερμοπρόσοψη
- Σιφώνι ομβρίων εξώστη, πλευρική έξοδος
- Δοκός (ξυλότυποι Σ2–Σ7) – ΚΑΜΙΑ οπή

B

ΕΡΓΟ	ΘΕΜΑ ΣΧΕΔΙΟΥ	ΒΑΣΗ	ΑΡ. ΣΧΕΔΙΟΥ
ΠΕΝΤΑΟΡΟΦΟ ΚΤΗΡΙΟ ΚΑΤΟΙΚΙΩΝ – ΑΡΓΥΡΟΥΠΟΛΗ Κωνσταντινουπόλεως 12 & Αγ. Βαρβάρας · Ο.Τ. 103-15 Εργοδότης: INTERKAT Α.Ε. · Κατασκευή: ARKAD Ι.Κ.Ε.	**Α΄·Β΄·Γ΄·Δ΄ – ΛΕΠΤΟΜΕΡΕΙΕΣ ΥΓΡΩΝ ΧΩΡΩΝ** R18 · λύματα · ακάθαρτα · αερισμοί · όμβρια · οπές πλακών Λουτρό γονέων · λουτρό · κουζίνα · υδρορροές στα κενά (ίδια και στον Δ΄)	ΑΠ-03 / ΑΠ-04 · τοιχοποιίες τυπικού R25	**ΑΠ-07** **Κλίμακα 1:25 · Α3** 10/11/2026 · R18

ΣΟΦΙΤΑ – ΛΕΠΤΟΜΕΡΕΙΑ ΥΓΡΩΝ ΧΩΡΩΝ

Κλίμακα 1:20

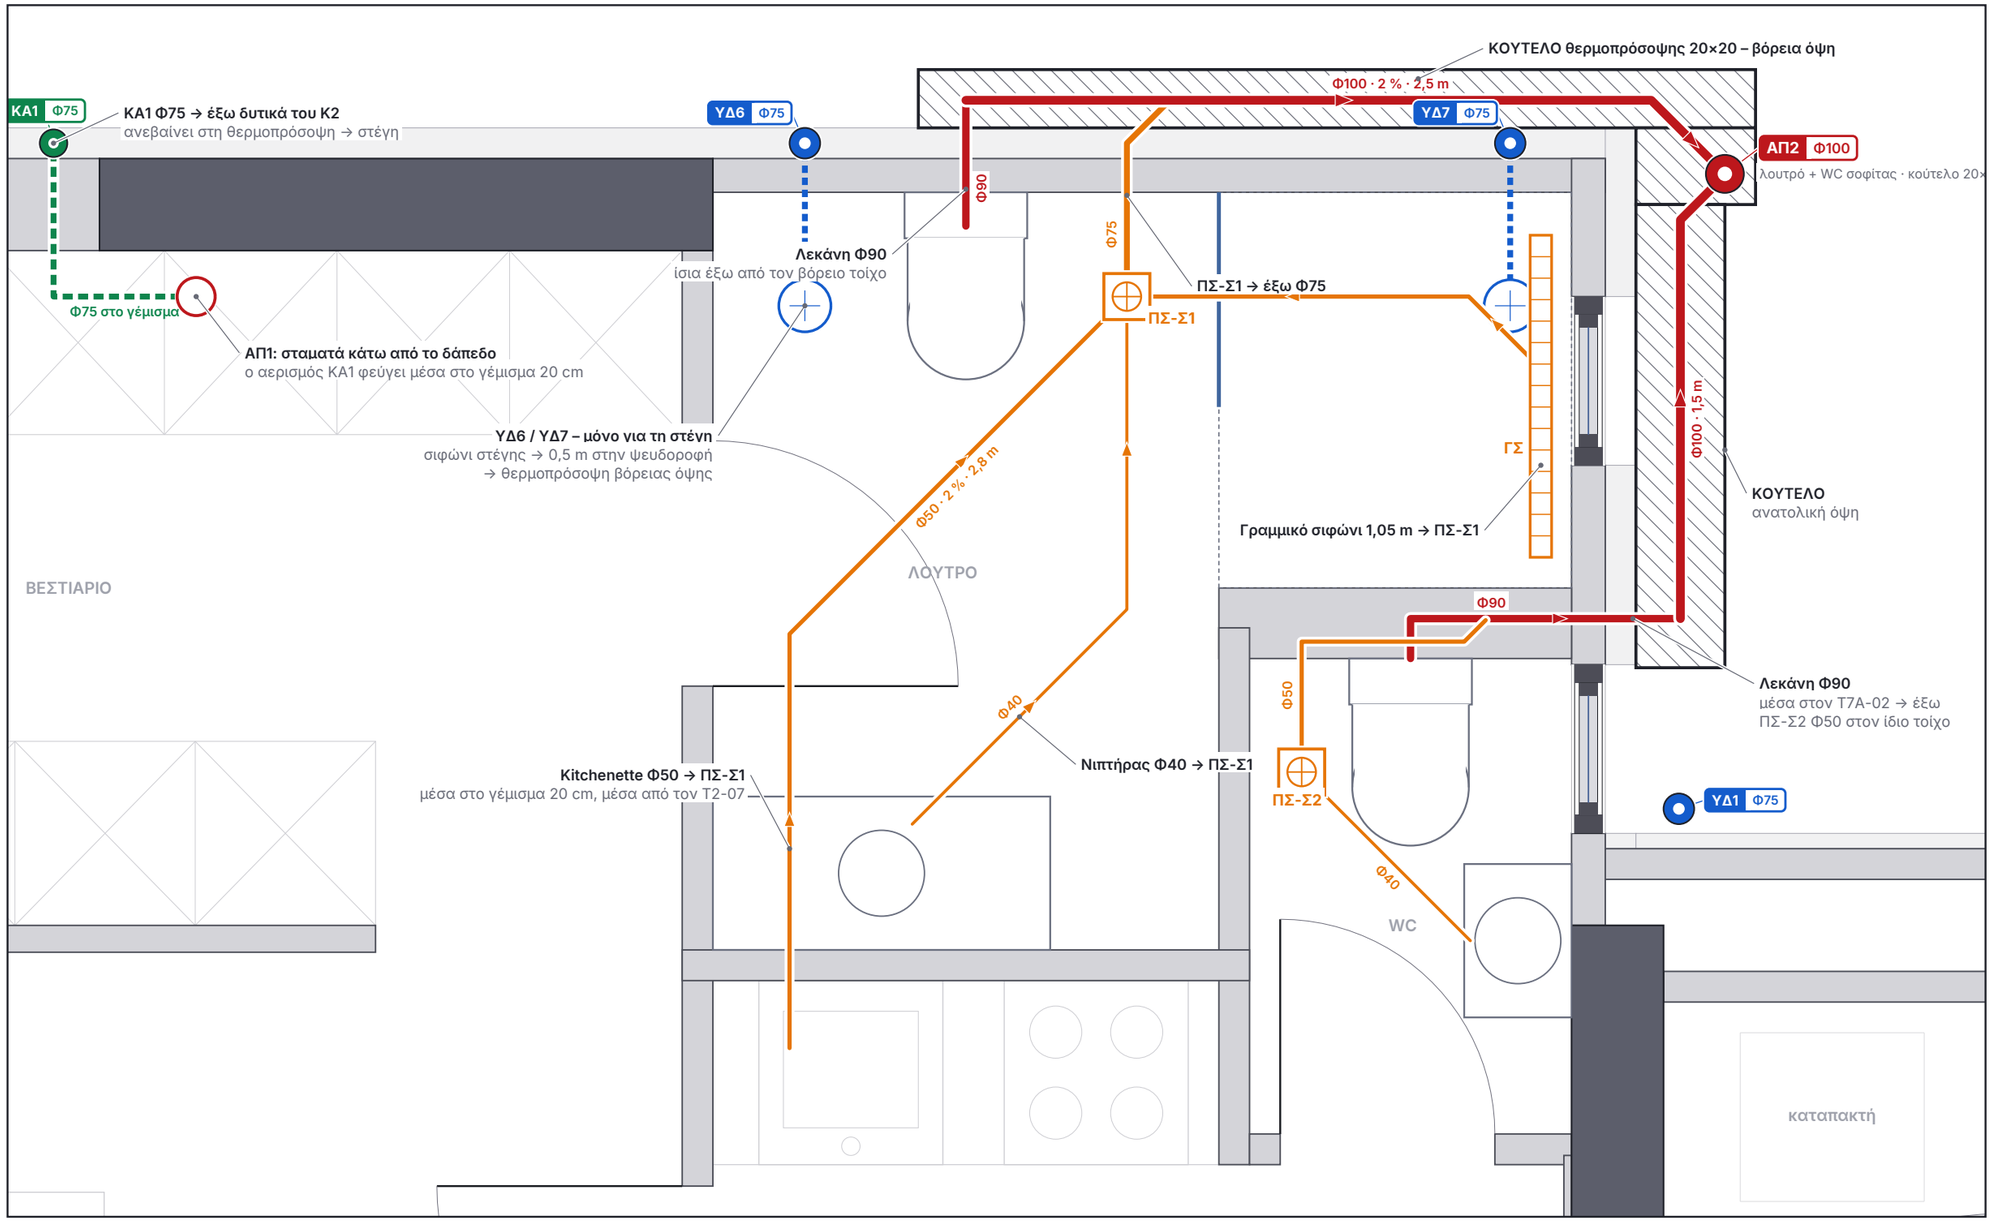

1 **ΛΟΥΤΡΟ · WC · ΚΙΤCHENETTE ΣΟΦΙΤΑΣ – ΕΞΟΔΟΙ & ΚΟΥΤΕΛΑ → ΑΠ2** Κλίμακα 1:20

ΥΠΟΜΝΗΜΑ


- Λύματα: λεκάνη Φ90 · στήλη / αγωγός Φ100
- Ακάθαρτα: Φ40 νιπτήρας · Φ50 ντους, νεροχύτης, πλυντήριο · Φ75 έξοδος πατοσίφωνου
- Αερισμός ΚΑ Φ75 (βγαίνει έξω και ανεβαίνει στη θερμοπρόσοψη)
- Κατακόρυφη στήλη λυμάτων ΑΠ
- Στήλη που περνά / σταματά (χωρίς σύνδεση στον όροφο)
- Πατοσίφωνο ΠΣ (σιφώνι δαπέδου με σχάρα)
- Γραμμικό σιφώνι ντους ΓΣ → πατοσίφωνο
- Κούτελο (κλειστό κανάλι γύρω από αγωγό)
- Άνοδος αερισμού στη θερμοπρόσοψη

B

ΕΡΓΟ	ΘΕΜΑ ΣΧΕΔΙΟΥ	ΒΑΣΗ	ΑΡ. ΣΧΕΔΙΟΥ
ΠΕΝΤΑΟΡΟΦΟ ΚΤΗΡΙΟ ΚΑΤΟΙΚΙΩΝ – ΑΡΓΥΡΟΥΠΟΛΗ Κωνσταντινουπόλεως 12 & Αγ. Βαρβάρας · Ο.Τ. 103-15 Εργοδότης: INTERKAT Α.Ε. · Κατασκευή: ARKAD Ι.Κ.Ε.	**ΣΟΦΙΤΑ – ΛΕΠΤΟΜΕΡΕΙΑ ΥΓΡΩΝ ΧΩΡΩΝ** R18 · λύματα · ακάθαρτα · αερισμοί · όμβρια · οπές πλακών Λουτρό · WC · kitchenette · εξωτερικοί Φ100 σε κούτελο	ΑΠ-05 · Α-10-S · Α-30-ΒΒ · τοιχοποιίες σοφίτας R04	**ΑΠ-08** **Κλίμακα 1:20 · Α3** 10/11/2026 · R18

ΚΑΤΑΚΟΡΥΦΟ ΔΙΑΓΡΑΜΜΑ ΑΠΟΧΕΤΕΥΣΗΣ & ΟΜΒΡΙΩΝ

Χωρίς κλίμακα

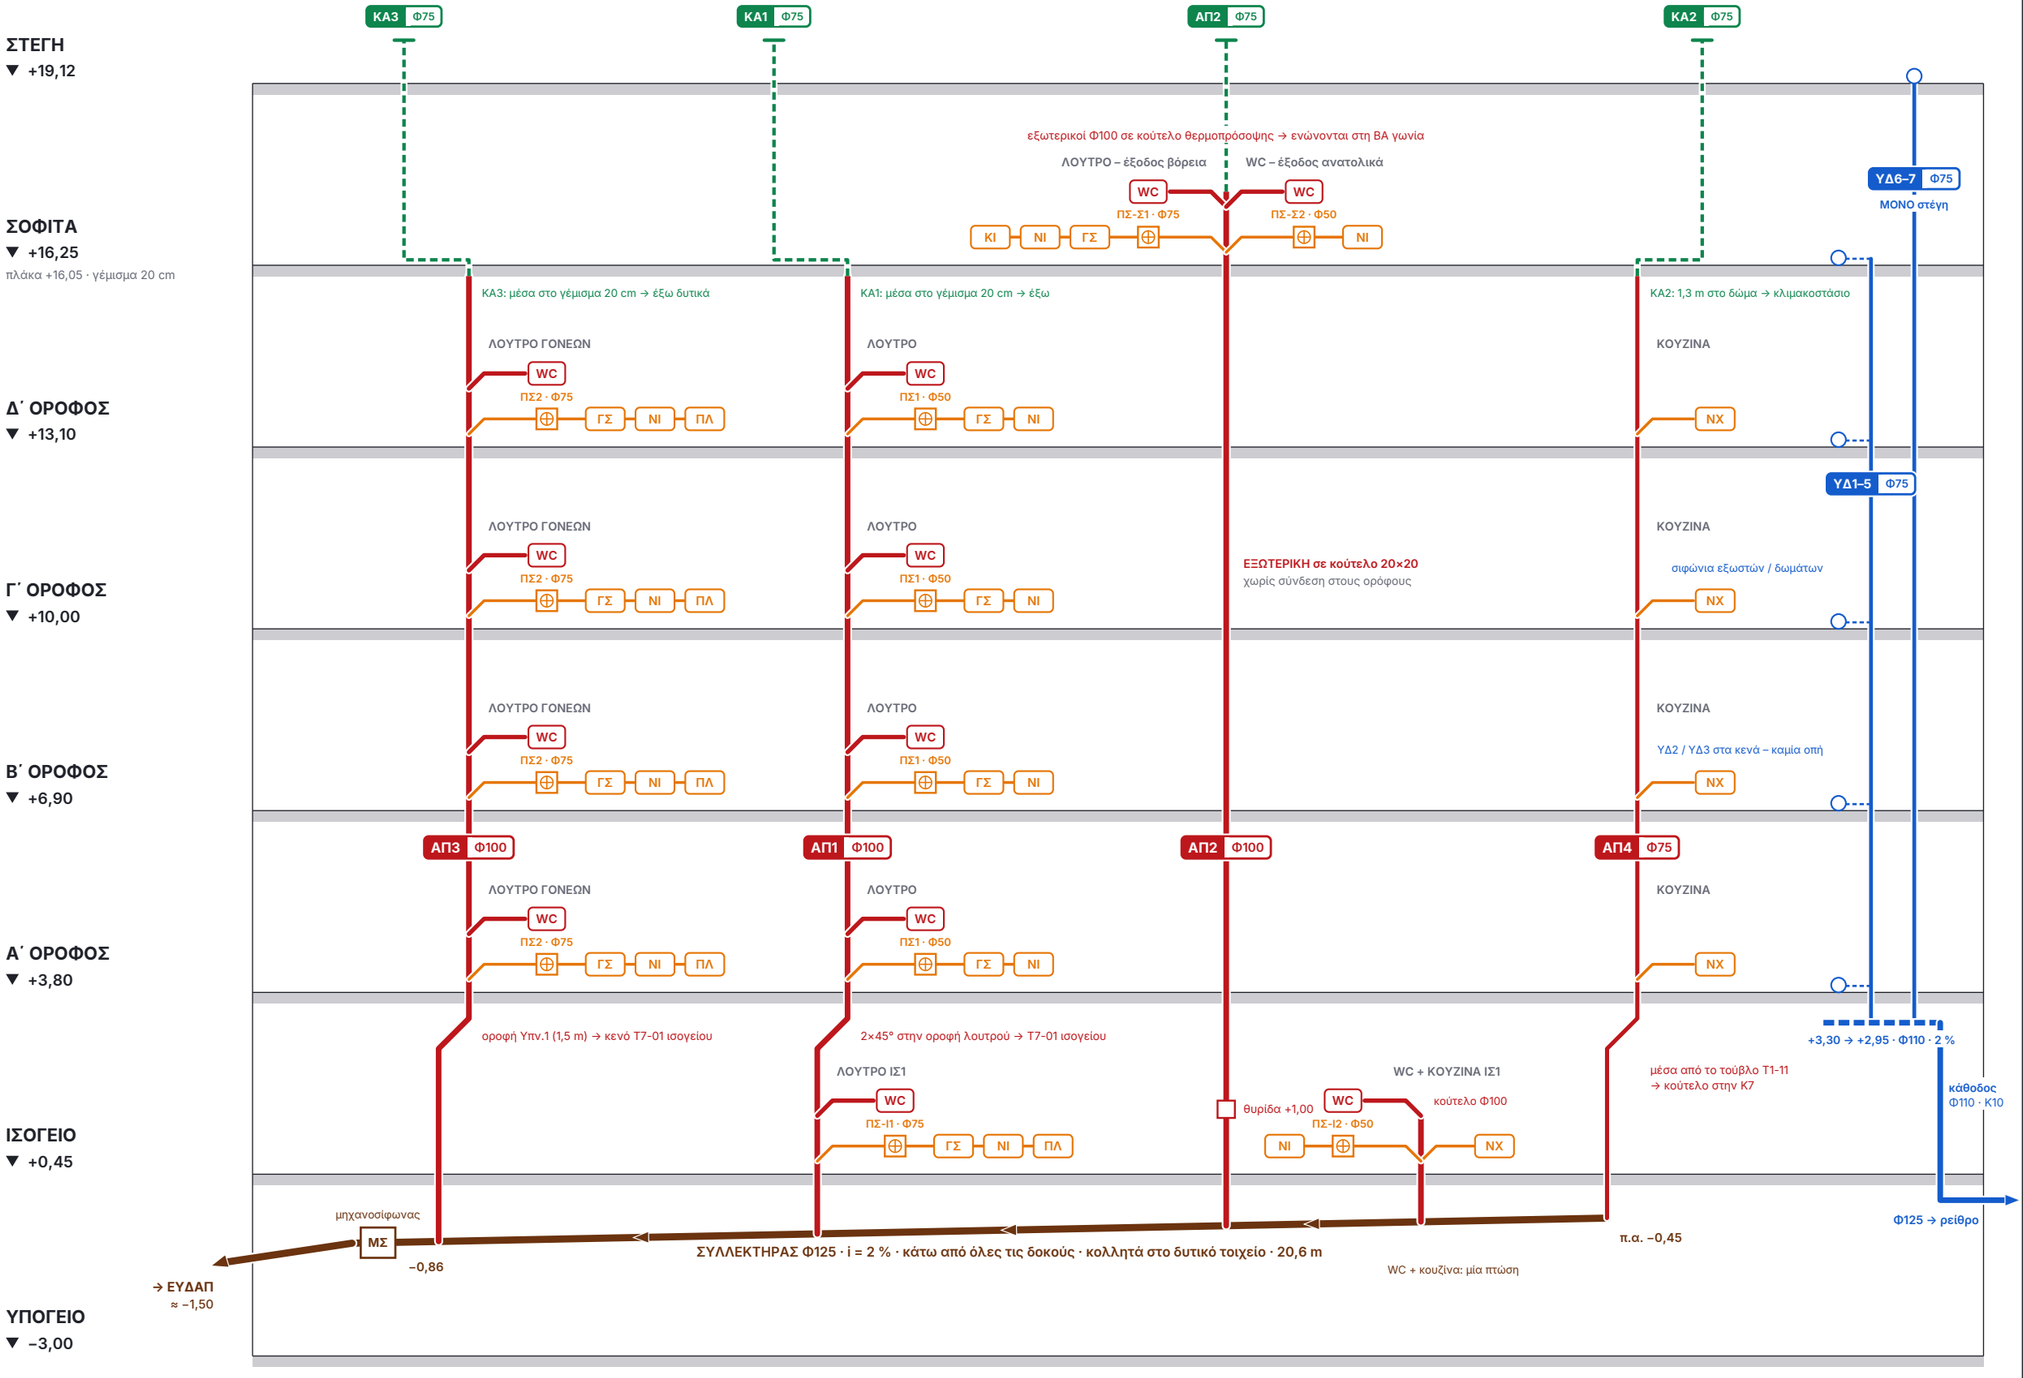

ΥΠΟΜΝΗΜΑ


- Λύματα: λεκάνη Φ90 · στήλη / αγωγός Φ100
- Ακάθαρτα: Φ40 νιπτήρας · Φ50 ντους, νεροχύτης, πλυντήριο · Φ75 έξοδος πατοσίφωνου
- Αερισμός ΚΑ Φ75 (βγαίνει έξω και ανεβαίνει στη θερμοπρόσοψη)
- Όμβρια: συλλεκτήρας / αγωγός
- Συλλεκτήρας ομβρίων ΨΗΛΑ +3,30 (οροφή προβόλων Α΄)
- Συλλεκτήρας / κλάδοι υπογείου, κρεμαστοί κάτω από τις δοκούς
- Πατοσίφωνο ΠΣ (σιφώνι δαπέδου με σχάρα)

ΣΥΝΤΟΜΟΓΡΑΦΙΕΣ

- **WC** λεκάνη κρεμαστή – Φ90 μέσα στον τοίχο λεκάνης
- **ΓΣ** γραμμικό σιφώνι ντους – Φ50 → πατοσίφωνο
- **ΝΙ** νιπτήρας – Φ40 → πατοσίφωνο
- **ΠΛ** πλυντήριο ρούχων – Φ50 → πατοσίφωνο
- **ΚΙ** kitchenette σοφίτας – Φ50 → πατοσίφωνο ΠΣ-Σ1
- **ΝΧ** νεροχύτης κουζίνας (+ πλυντήριο πιάτων) – Φ50
- **ΠΣ** πατοσίφωνο · δίπλα η διατομή εξόδου
- **ΚΑ** αερισμός στήλης Φ75 ως πάνω από τη στέγη

Β

ΕΡΓΟ	ΘΕΜΑ ΣΧΕΔΙΟΥ	ΒΑΣΗ	ΑΡ. ΣΧΕΔΙΟΥ
ΠΕΝΤΑΟΡΟΦΟ ΚΤΗΡΙΟ ΚΑΤΟΙΚΙΩΝ – ΑΡΓΥΡΟΥΠΟΛΗ Κωνσταντινουπόλεως 12 & Αγ. Βαρβάρας · Ο.Τ. 103-15 Εργοδότης: INTERKAT Α.Ε. · Κατασκευή: ARKAD Ι.Κ.Ε.	**ΚΑΤΑΚΟΡΥΦΟ ΔΙΑΓΡΑΜΜΑ** R18 · λύματα · ακάθαρτα · αερισμοί · όμβρια · οπές πλακών Στήλες ΑΠ1–ΑΠ4 · αερισμοί · συλλεκτήρας · όμβρια	ΑΠ-01 … ΑΠ-05	**ΑΠ-09** **Χωρίς κλίμακα · Α3** 10/11/2026 · R18

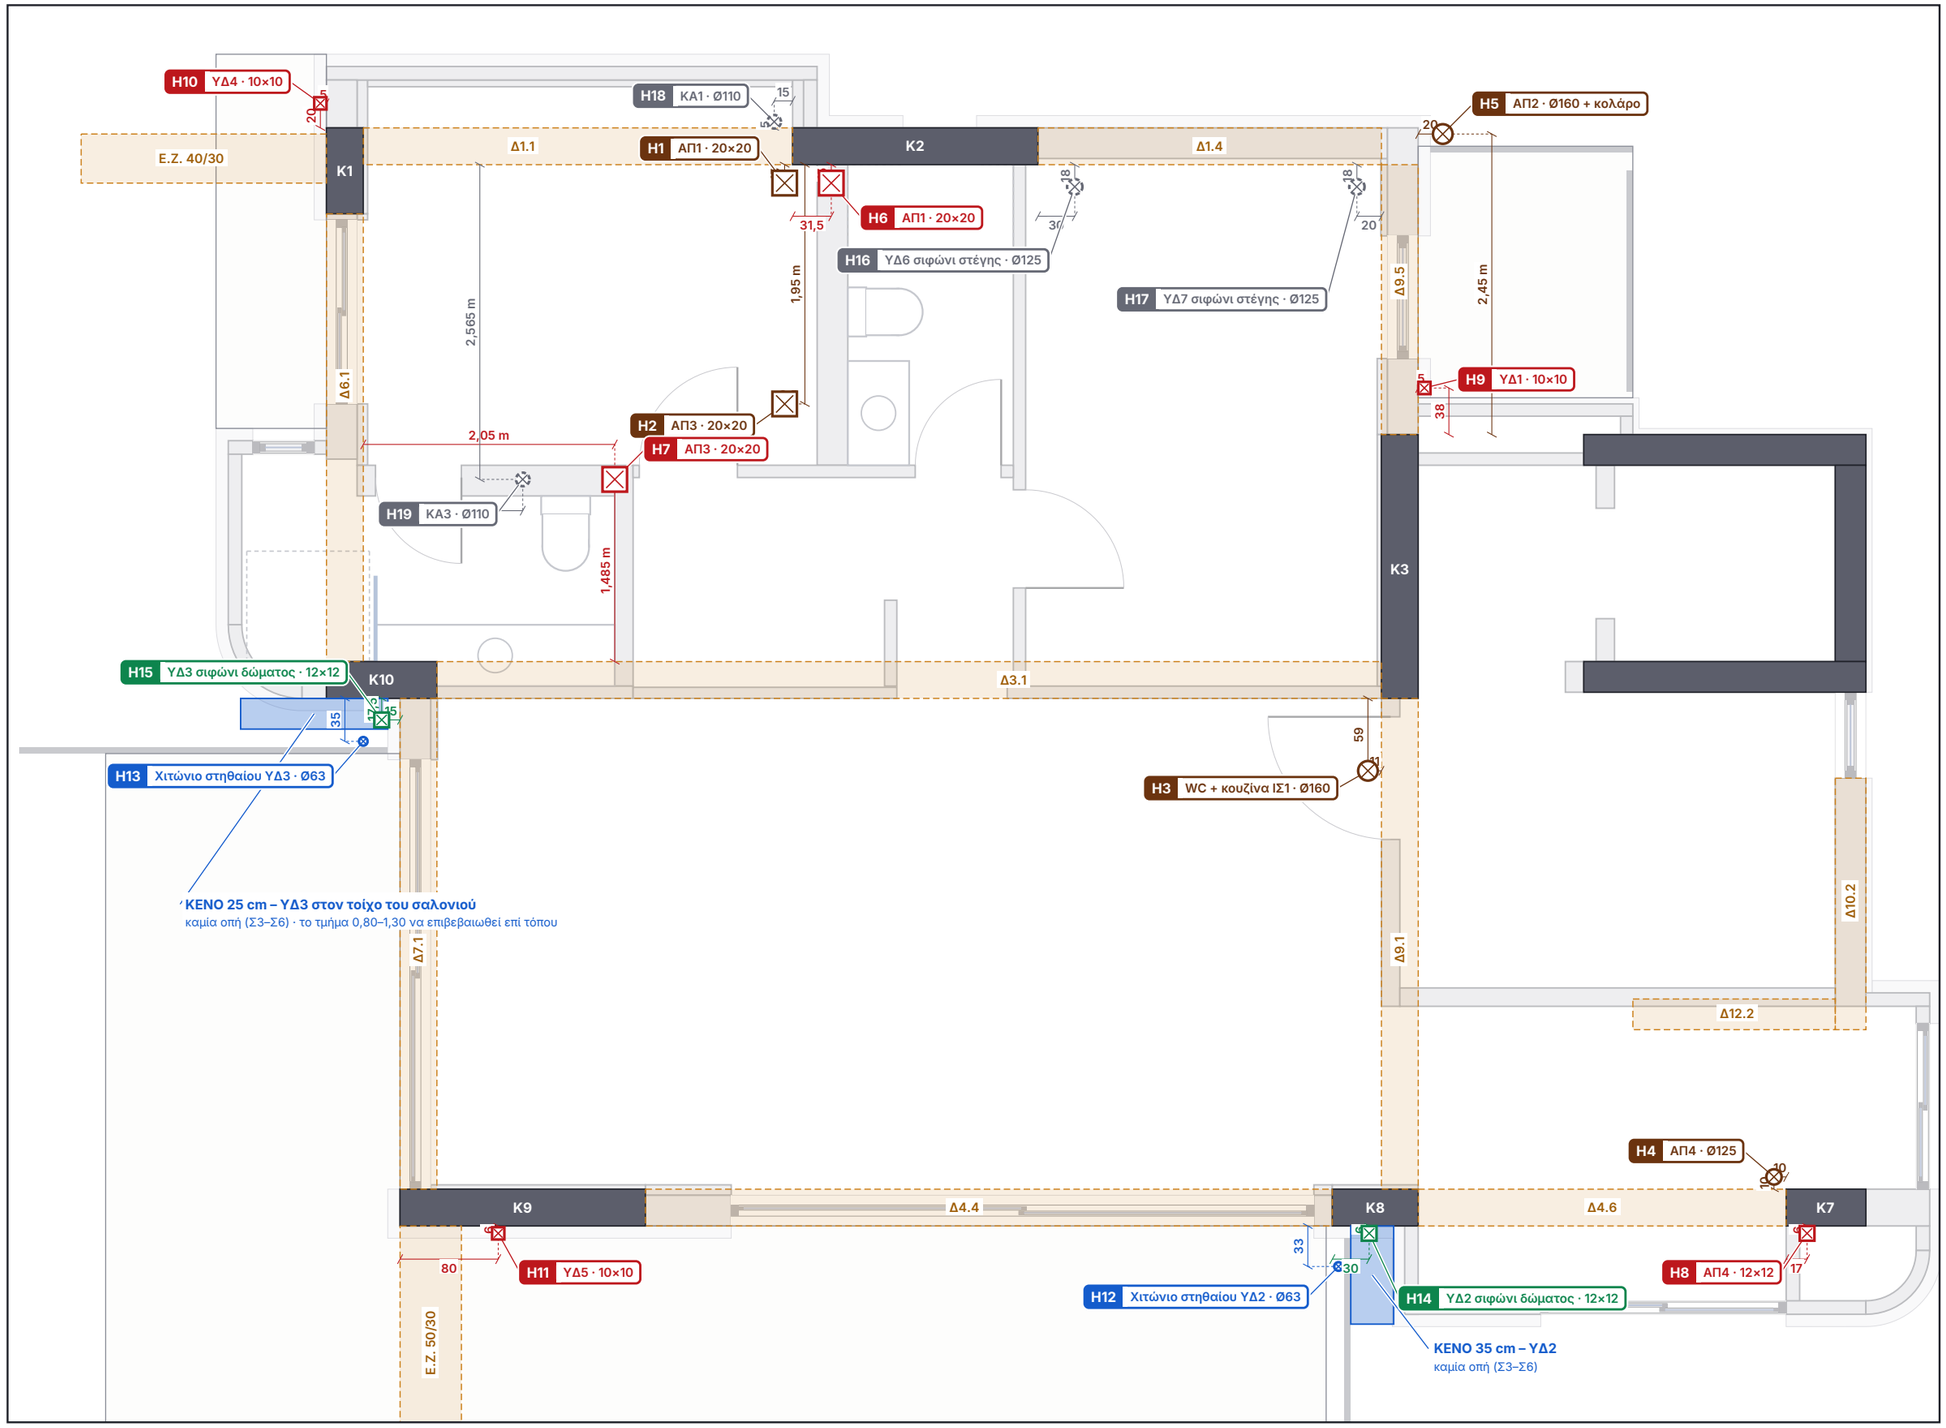

H **ΟΠΕΣ ΚΑΙ ΑΝΑΜΟΝΕΣ ΣΕ ΟΛΕΣ ΤΙΣ ΠΛΑΚΕΣ – διαστάσεις σε cm από παρειές σκυροδέματος** Κλίμακα 1:50

B

ΧΡΩΜΑ = ΠΛΑΚΑ

- Σ2 – πλάκα οροφής υπογείου (+0,30)
- Σ3 … Σ7 – οροφή ισογείου, Α΄, Β΄, Γ΄, Δ΄ (ίδια θέση σε όλες)
- Σ3 … Σ6 – χιτώνιο στη βάση του στηθαίου (όχι στην πλάκα)
- Σ7 μόνο – δώμα (+16,05): σιφώνια δώματος
- Σ8 – στέγη (προκαταρκτικά)

ΠΙΝΑΚΑΣ ΟΠΩΝ

H1 **ΑΠ1 Φ100 · 20×20 · Σ2**
6,5 δυτ. της Δ παρ. Κ2 · 15 νότια της Ν παρ. Κ2

H2 **ΑΠ3 Φ100 · 20×20 · Σ2**
6,5 δυτ. της Δ παρ. Κ2 · 1,95 m νότια της Ν παρ. Κ2

H3 **WC + κουζίνα ΙΣ1 Φ100 · Ø160 · Σ2**
11 δυτ. της Δ παρ. Δ9.1 · 59 νότια της Ν παρ. Κ3

H4 **ΑΠ4 Φ75 · Ø125 · Σ2**
10 δυτ. της Δ παρ. Κ7 · 10 βόρ. της Β παρ. Κ7

H5 **ΑΠ2 Φ100 · Ø160 + κολάρο · Σ2**
20 ανατ. της Α παρ. Δ9.5 · 2,45 m βόρ. της Β παρ. Κ3

H6 **ΑΠ1 Φ100 · 20×20 · Σ3–Σ7**
31,5 ανατ. της Δ παρ. Κ2 · 15 νότια της Ν παρ. Κ2

H7 **ΑΠ3 Φ100 · 20×20 · Σ3–Σ7**
2,05 m ανατ. της Α παρ. Δ6.1 · 1,485 m βόρ. της Β παρ. Δ3.1

H8 **ΑΠ4 Φ75 · 12×12 · Σ3–Σ7**
17 ανατ. της Δ παρ. Κ7 · 6 νότια της Ν παρ. Κ7

H9 **ΥΔ1 Φ75 · 10×10 · Σ3–Σ7**
5 ανατ. της Α παρ. Δ9.5 · 38 βόρ. της Β παρ. Κ3

H10 **ΥΔ4 Φ75 · 10×10 · Σ3–Σ7**
5 δυτ. της Δ παρ. Κ1 · 20 βόρ. της Β παρ. Κ1

H11 **ΥΔ5 Φ75 · 10×10 · Σ3–Σ7**
80 ανατ. της Δ παρ. Κ9 · 6 νότια της Ν παρ. Κ9

H12 **Χιτώνιο στηθαίου ΥΔ2 Φ50 · Ø63 · Σ3–Σ6**
33 νότια της Ν παρ. Κ8

H13 **Χιτώνιο στηθαίου ΥΔ3 Φ50 · Ø63 · Σ3–Σ6**
35 νότια της Ν παρ. Κ10

H14 **ΥΔ2 σιφώνι δώματος Φ75 · 12×12 · Σ7**
30 ανατ. της Δ παρ. Κ8 · 6 νότια της Ν παρ. Κ8

H15 **ΥΔ3 σιφώνι δώματος Φ75 · 12×12 · Σ7**
15 δυτ. της Δ παρ. Δ7.1 · 17,5 νότια της Ν παρ. Κ10

H16 **ΥΔ6 σιφώνι στέγης Φ75 · Ø125 · Σ8**
30 ανατ. της Α παρ. Κ2 · 18 νότια της Ν παρ. Δ1.5

H17 **ΥΔ7 σιφώνι στέγης Φ75 · Ø125 · Σ8**
20 δυτ. της Δ παρ. Δ9.5 · 18 νότια της Ν παρ. Δ1.5

H18 **ΚΑ1 Φ75 · Ø110 · Σ8**
15 δυτ. της Δ παρ. Κ2 · 5 βόρ. της Β παρ. Δ1.2

H19 **ΚΑ3 Φ75 · Ø110 · Σ8**
70 ανατ. της Α παρ. Δ7.4 · 2,565 m νότια της Ν παρ. Δ1.2

– **Έξοδος συλλεκτήρα · χιτώνιο Ø200**
νότιο τοιχείο υπογείου, 50 cm ανατ. της εσωτ. παρειάς του δυτικού τοιχείου, π.α. −0,86 (ΑΠ-01)

ΕΡΓΟ
ΠΕΝΤΑΟΡΟΦΟ ΚΤΗΡΙΟ ΚΑΤΟΙΚΙΩΝ – ΑΡΓΥΡΟΥΠΟΛΗ
Κωνσταντινουπόλεως 12 & Αγ. Βαρβάρας · Ο.Τ. 103-15
Εργοδότης: INTERKAT Α.Ε. · Κατασκευή: ARKAD Ι.Κ.Ε.

ΘΕΜΑ ΣΧΕΔΙΟΥ
ΟΠΕΣ ΠΛΑΚΩΝ – ΟΛΕΣ ΣΕ ΕΝΑ ΣΧΕΔΙΟ
R18 · λύματα · ακάθαρτα · αερισμοί · όμβρια · οπές πλακών
Σ2 · Σ3–Σ7 · Σ8 · θέσεις από παρειές σκυροδέματος

ΒΑΣΗ
Σ2_ΕΦ … Σ7_ΕΦ · Σ8 · υπόβαθρο: τυπικός όροφος

ΑΡ. ΣΧΕΔΙΟΥ
ΑΠ-10
Κλίμακα 1:50 · Α3
10/11/2026 · R18