
ΟΡΟΦΗ ΥΠΟΓΕΙΟΥ – ΣΥΛΛΕΚΤΗΡΑΣ ΛΥΜΑΤΩΝ

Κλίμακα 1:80

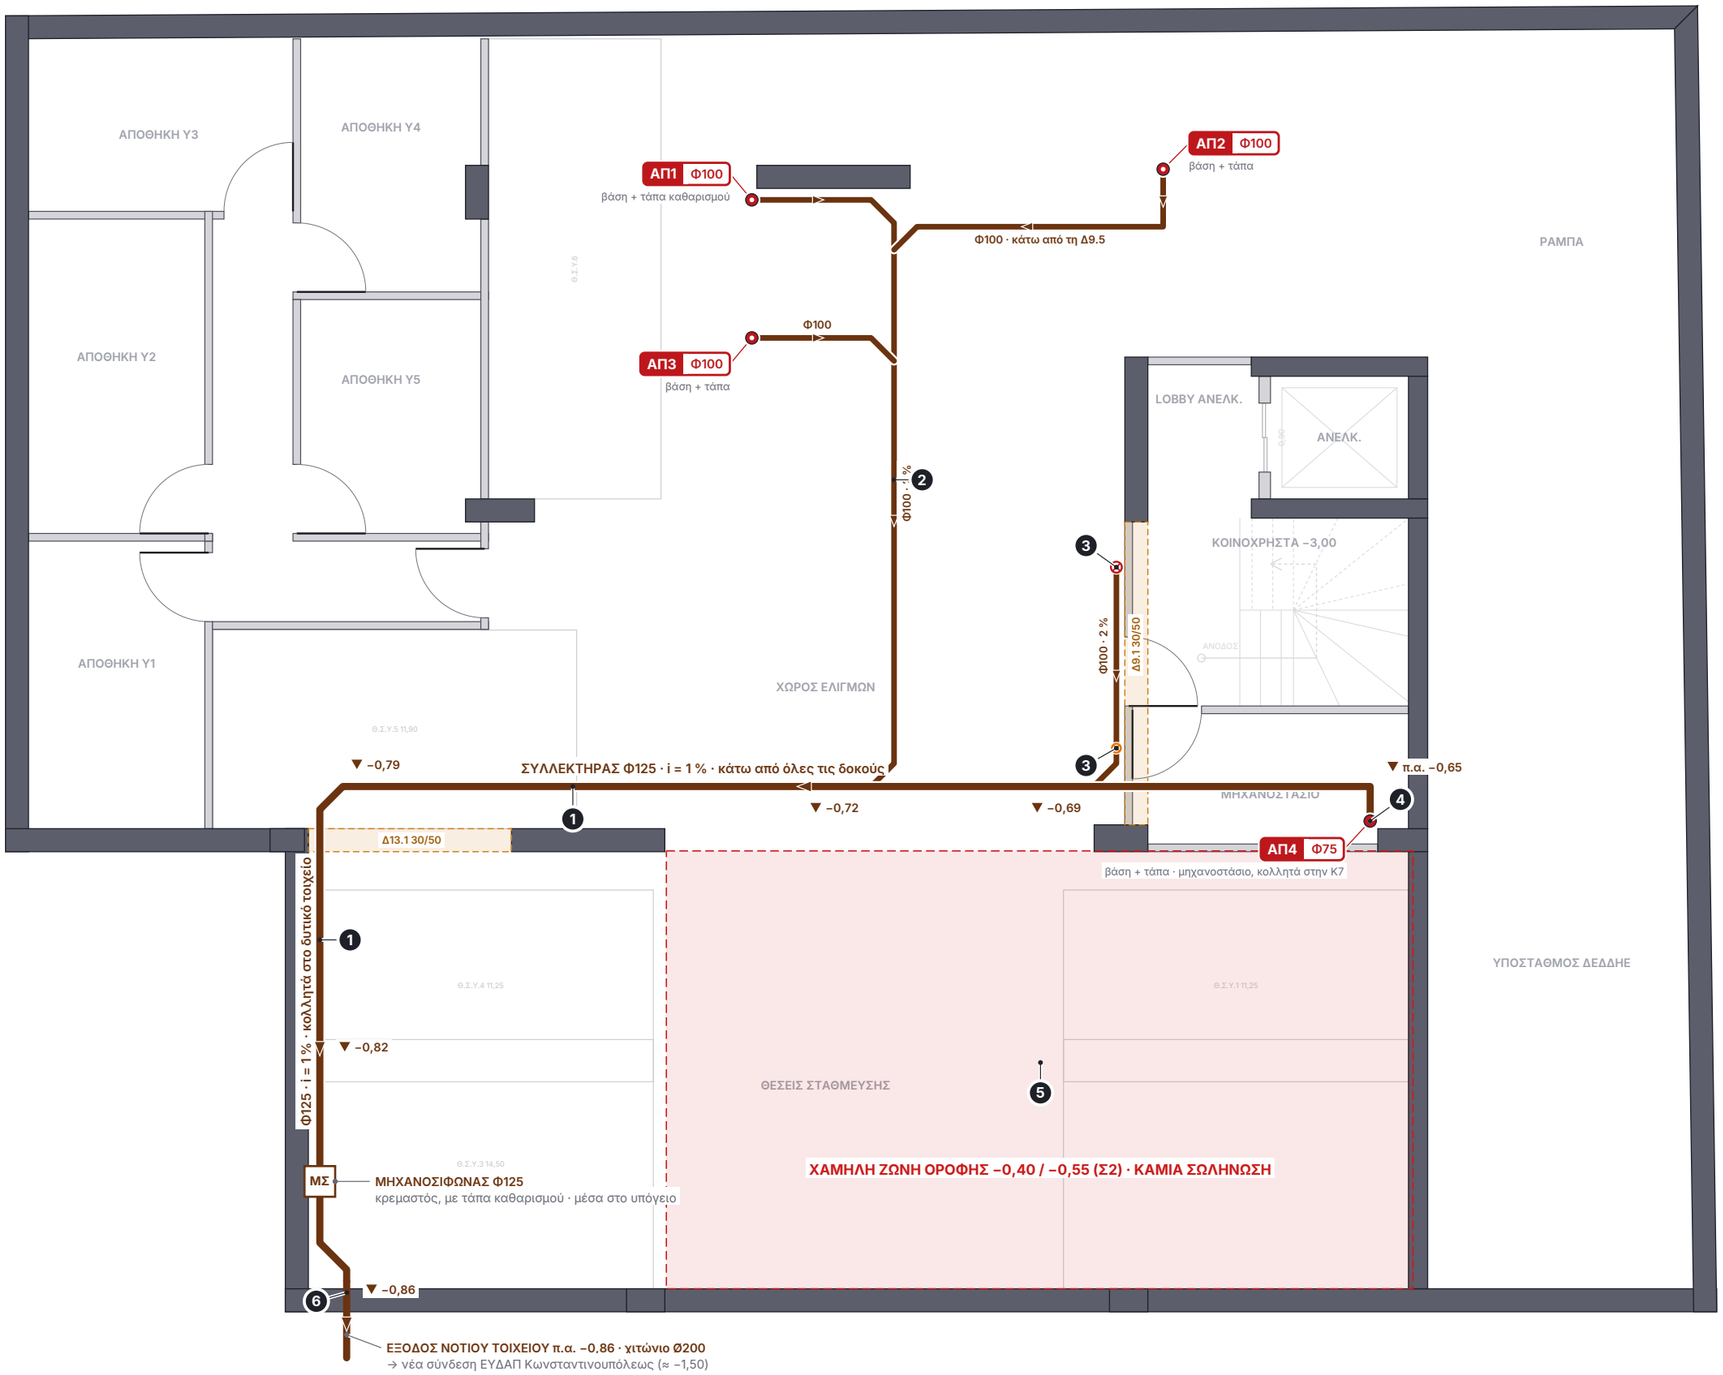

ΥΠΟΜΝΗΜΑ

- Συλλεκτήρας / κλάδοι υπογείου, κρεμαστοί κάτω από τις δοκούς
- Κατακόρυφη στήλη λυμάτων ΑΠ
- Πτώση στον κάτω όροφο
- Δοκός (ξυλότυποι Σ2–Σ7) – ΚΑΜΙΑ οπή
- Χαμηλή ζώνη οροφής υπογείου – καμία σωλήνωση
- 1 Αριθμημένη σημείωση – βλ. ΣΗΜΕΙΩΣΕΙΣ

ΣΗΜΕΙΩΣΕΙΣ

1. **Συλλεκτήρας Φ125, i = 1 %, 20,6 m:** κεφαλή ΑΠ4 π.α. −0,65 → γ 8,60 → ΚΟΛΛΗΤΑ ΣΤΟ ΔΥΤΙΚΟ ΤΟΙΧΕΙΟ (άξονας x −1,10, 15 cm από την παρειά) → έξοδος −0,86. Κρεμαστός κάτω από ΟΛΕΣ τις δοκούς – καμία διάτρηση. Οι Θ.Σ.Υ. 3 / 4 μένουν ελεύθερες.
2. **Κλάδος x 6,39:** ΑΠ1 (+ λουτρό ΙΣ1), ΑΠ3 και ΑΠ2. Οι ΑΠ1 / ΑΠ3 κατεβαίνουν στο κενό του Τ7-01 ισογείου (x 4,535). Η ΑΠ2 (σοφίτα) περνά κάτω από τη Δ9.5.
3. **WC + κουζίνα ΙΣ1 (x 9,29):** πτώση WC από το κούτελο 9,29 / 5,74 και πτώση νεροχύτη 9,29 / 8,10 σε ΕΝΑΝ κλάδο, 5 cm δυτικά της Δ9.1.
4. **Βάση ΑΠ4:** 12,60 / 9,05 μέσα στο μηχανοστάσιο, κολλητά στην Κ7 (πλάκα Π10, βόρεια της δοκού Κ8–Κ7).
5. **Χαμηλές ζώνες −0,40 / −0,55:** καμία σωλήνωση. Ο υποσταθμός ΔΕΔΔΗΕ δεν αγγίζεται.
6. **Μηχανοσίφωνας Φ125** πριν από την έξοδο, επισκέψιμος. Έξοδος από το ΝΟΤΙΟ τοιχείο στο x −0,75 (έξω από το γωνιακό υποστύλωμα), χιτώνιο Ø200. Συμβολές 45°, τάπα σε κάθε βάση στήλης.


ΕΛΕΓΧΟΣ

- Καθαρό ύψος κάτω από τον συλλεκτήρα στο δυτικό τοιχείο ≈ 2,14 m.
- Βάθος σύνδεσης ΕΥΔΑΠ (≈ −1,50) – να επιβεβαιωθεί επί τόπου.

ΕΡΓΟ	ΘΕΜΑ ΣΧΕΔΙΟΥ	ΒΑΣΗ	ΑΡ. ΣΧΕΔΙΟΥ
ΠΕΝΤΑΟΡΟΦΟ ΚΤΗΡΙΟ ΚΑΤΟΙΚΙΩΝ – ΑΡΓΥΡΟΥΠΟΛΗ Κωνσταντινουπόλεως 12 & Αγ. Βαρβάρας · Ο.Τ. 103-15 Εργοδότης: INTERKAT Α.Ε. · Κατασκευή: ARKAD Ι.Κ.Ε.	**ΥΠΟΓΕΙΟ – ΣΥΛΛΕΚΤΗΡΑΣ ΛΥΜΑΤΩΝ** R17 · λύματα · ακάθαρτα · αερισμοί · όμβρια · οπές πλακών Οροφή υπογείου · συλλεκτήρας στο δυτικό τοιχείο · έξοδος −0,86	Σ2 εφαρμογής · τοιχοποιίες υπογείου R05	**ΑΠ-01** **Κλίμακα 1:80 · A3** 10/11/2026 · R17

ΚΑΤΟΨΗ ΙΣΟΓΕΙΟΥ – ΑΠΟΧΕΤΕΥΣΗ & ΟΜΒΡΙΑ

Κλίμακα 1:60

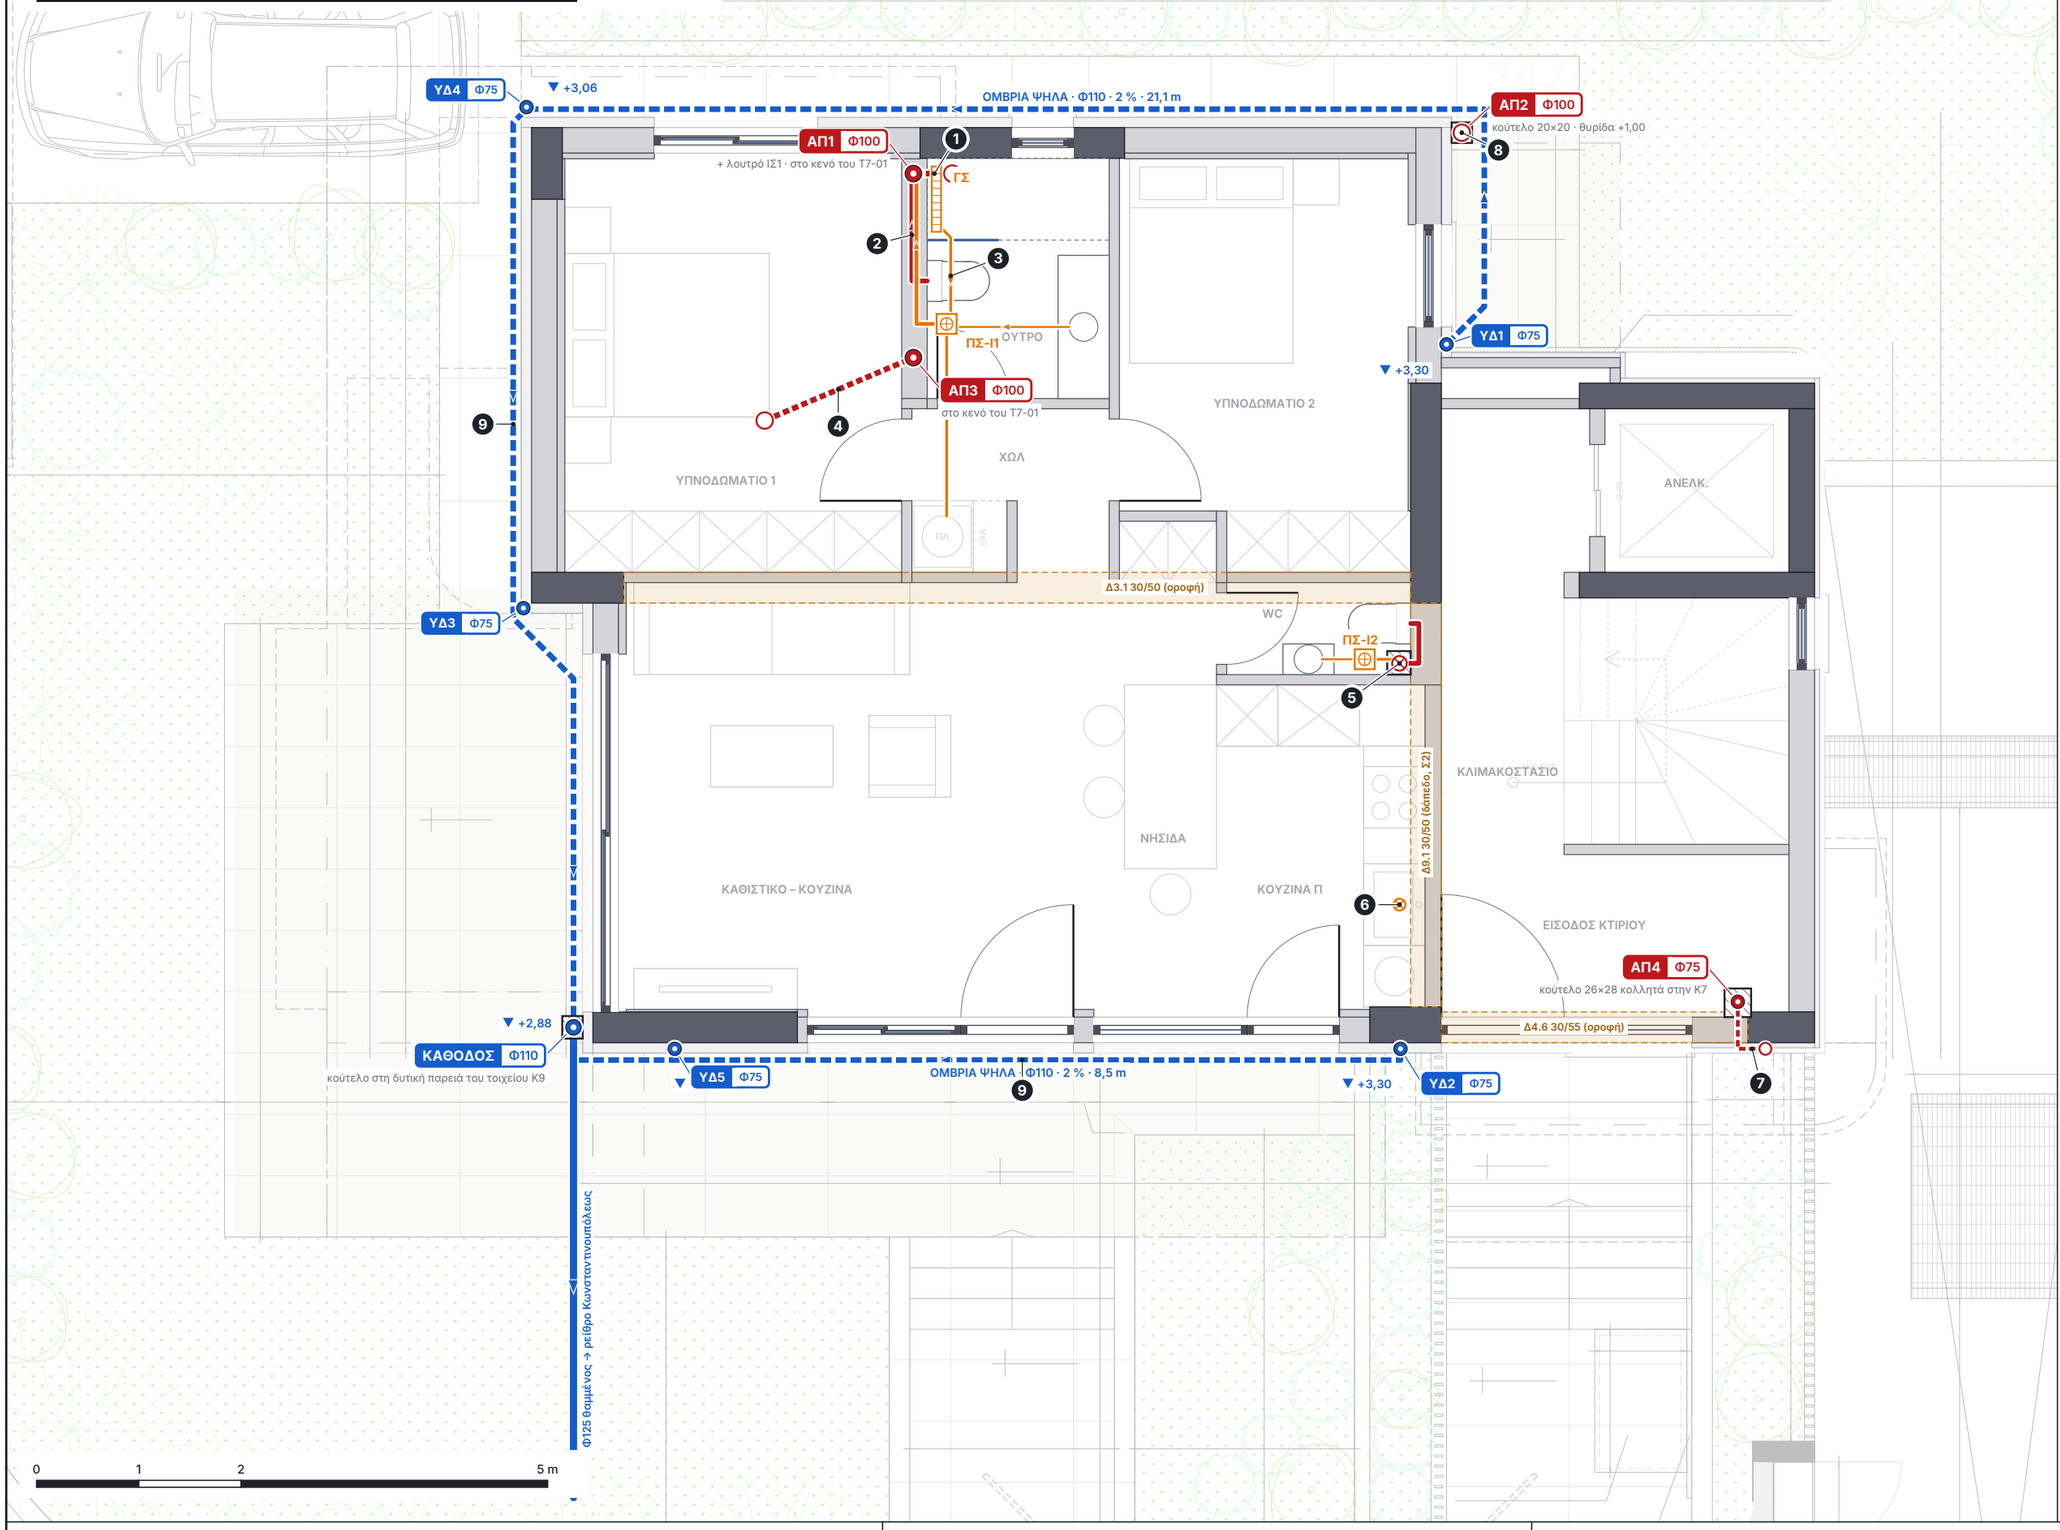

ΥΠΟΜΝΗΜΑ

- Λύματα: λεκάνη Φ90 · στήλη / αγωγός Φ100
- Ακάθαρτα: Φ40 νιπτήρας · Φ50 ντους, νεροχύτης, πλυντήριο · Φ75 έξοδος πατοσίφωνου
- Αγωγός στην οροφή του ορόφου (μετατόπιση στήλης 2×45°)
- Συλλεκτήρας ομβρίων ΨΗΛΑ +3,30 (οροφή προβόλων Α΄)
- Όμβρια: συλλεκτήρας / αγωγός
- Κατακόρυφη στήλη λυμάτων ΑΠ
- Στήλη που περνά / σταματά (χωρίς σύνδεση στον όροφο)
- Πτώση στον κάτω όροφο
- Πατοσίφωνο ΠΣ (σιφώνι δαπέδου με σχάρα)
- Γραμμικό σιφώνι ντους ΓΣ → πατοσίφωνο
- Κούτελο (κλειστό κανάλι γύρω από αγωγό)
- Υδρορροή ΥΔ Φ75 μέσα στη θερμοπρόσοψη
- Δοκός (Ευλότυποι Σ2–Σ7) – ΚΑΜΙΑ οπή


ΣΗΜΕΙΩΣΕΙΣ

1. **ΑΠ1:** μετατόπιση 2×45° στην οροφή του λουτρού → κατεβαίνει στο ΚΕΝΟ του Τ7-01 του ισογείου (4,535 / 0,95).
2. **Λουτρό → ΑΠ1:** λεκάνη Φ90 στο κενό του Τ7-01. Σύνδεση ≈ 0,6 m πάνω από τον συλλεκτήρα → βάση με 2×45° και ευθύ 25 cm.
3. **Γραμμικό σιφώνι → πατοσίφωνο ΠΣ-Ι1** (Φ50). Νιπτήρας Φ40 και πλυντήριο Φ50 επίσης στο ΠΣ-Ι1. ΠΣ-Ι1 → ΑΠ1 Φ75 μέσα στον τοίχο.
4. **ΑΠ3 ΣΤΗΝ ΟΡΟΦΗ:** 1,6 m στην οροφή του Υπν.1 (κούτελο οροφής 25×25, κλίση 2 %) → κατεβαίνει στο ΚΕΝΟ του Τ7-01 ισογείου (4,535 / 2,75), όχι μέσα στη ντουλάπα.
5. **WC:** λεκάνη Φ90 μέσα στον Τ7-02 → ΚΟΥΤΕΛΟ 23×23 δίπλα στη λεκάνη, πτώση Φ100 μέσα από πλάκα. Κάτω από τον τοίχο είναι η Δ9.1 – καμία οπή σε δοκό. Νιπτήρας → ΠΣ-Ι2 → κούτελο.
6. **Νεροχύτης:** Φ50 → πτώση Φ75. Στο υπόγειο ενώνεται με το WC.
7. **ΑΠ4 Φ75:** κατεβαίνει κολλητά στην Κ7, 0,3 m δυτικά μέσα από το τούβλο Τ1-11 (κάτω από τη Δ4.6) → ΚΟΥΤΕΛΟ 26×28 στη γωνία της Κ7 → μηχανοστάσιο.
8. **ΑΠ2 Φ100 εξωτερική** (σοφίτα) σε κούτελο 20×20 στη ΒΑ γωνία: θυρίδα καθαρισμού +1,00, περνά την πλάκα Σ2 20 cm ανατολικά της Δ9.5.
9. **Όμβρια 2 %:** ΥΔ1–ΥΔ5 → συλλεκτήρας ψηλά, δύο κλάδοι από +3,30: βόρειος 21,1 m → +2,88, νότιος 8,5 m → +3,13. Κεντρική κάθοδος Φ110 σε κούτελο στο τοιχείο Κ9 (ΝΔ γωνία) → Φ125 θαμμένος → ρείθρο.

ΕΡΓΟ	ΘΕΜΑ ΣΧΕΔΙΟΥ	ΒΑΣΗ	ΑΡ. ΣΧΕΔΙΟΥ
ΠΕΝΤΑΟΡΟΦΟ ΚΤΗΡΙΟ ΚΑΤΟΙΚΙΩΝ – ΑΡΓΥΡΟΥΠΟΛΗ Κωνσταντινουπόλεως 12 & Αγ. Βαρβάρας · Ο.Τ. 103-15 Εργοδότης: INTERKAT Α.Ε. · Κατασκευή: ARKAD Ι.Κ.Ε.	**ΙΣΟΓΕΙΟ – ΑΠΟΧΕΤΕΥΣΗ & ΟΜΒΡΙΑ** R17 · λύματα · ακάθαρτα · αερισμοί · όμβρια · οπές πλακών ΑΠ1 / ΑΠ3 στο κενό του Τ7-01 · κούτελα WC / ΑΠ4 · όμβρια 2 % · λεπτομέρειες στο ΑΠ-06	Σ2 / Σ3 εφαρμογής · τοιχοποιίες ισογείου R13	**ΑΠ-02** **Κλίμακα 1:60 · Α3** 10/11/2026 · R17

ΚΑΤΟΨΗ Α΄ · Β΄ · Γ΄ ΟΡΟΦΟΥ (ΤΥΠΙΚΟΣ) – ΑΠΟΧΕΤΕΥΣΗ & ΥΔΡΟΡΡΟΕΣ

Κλίμακα 1:60

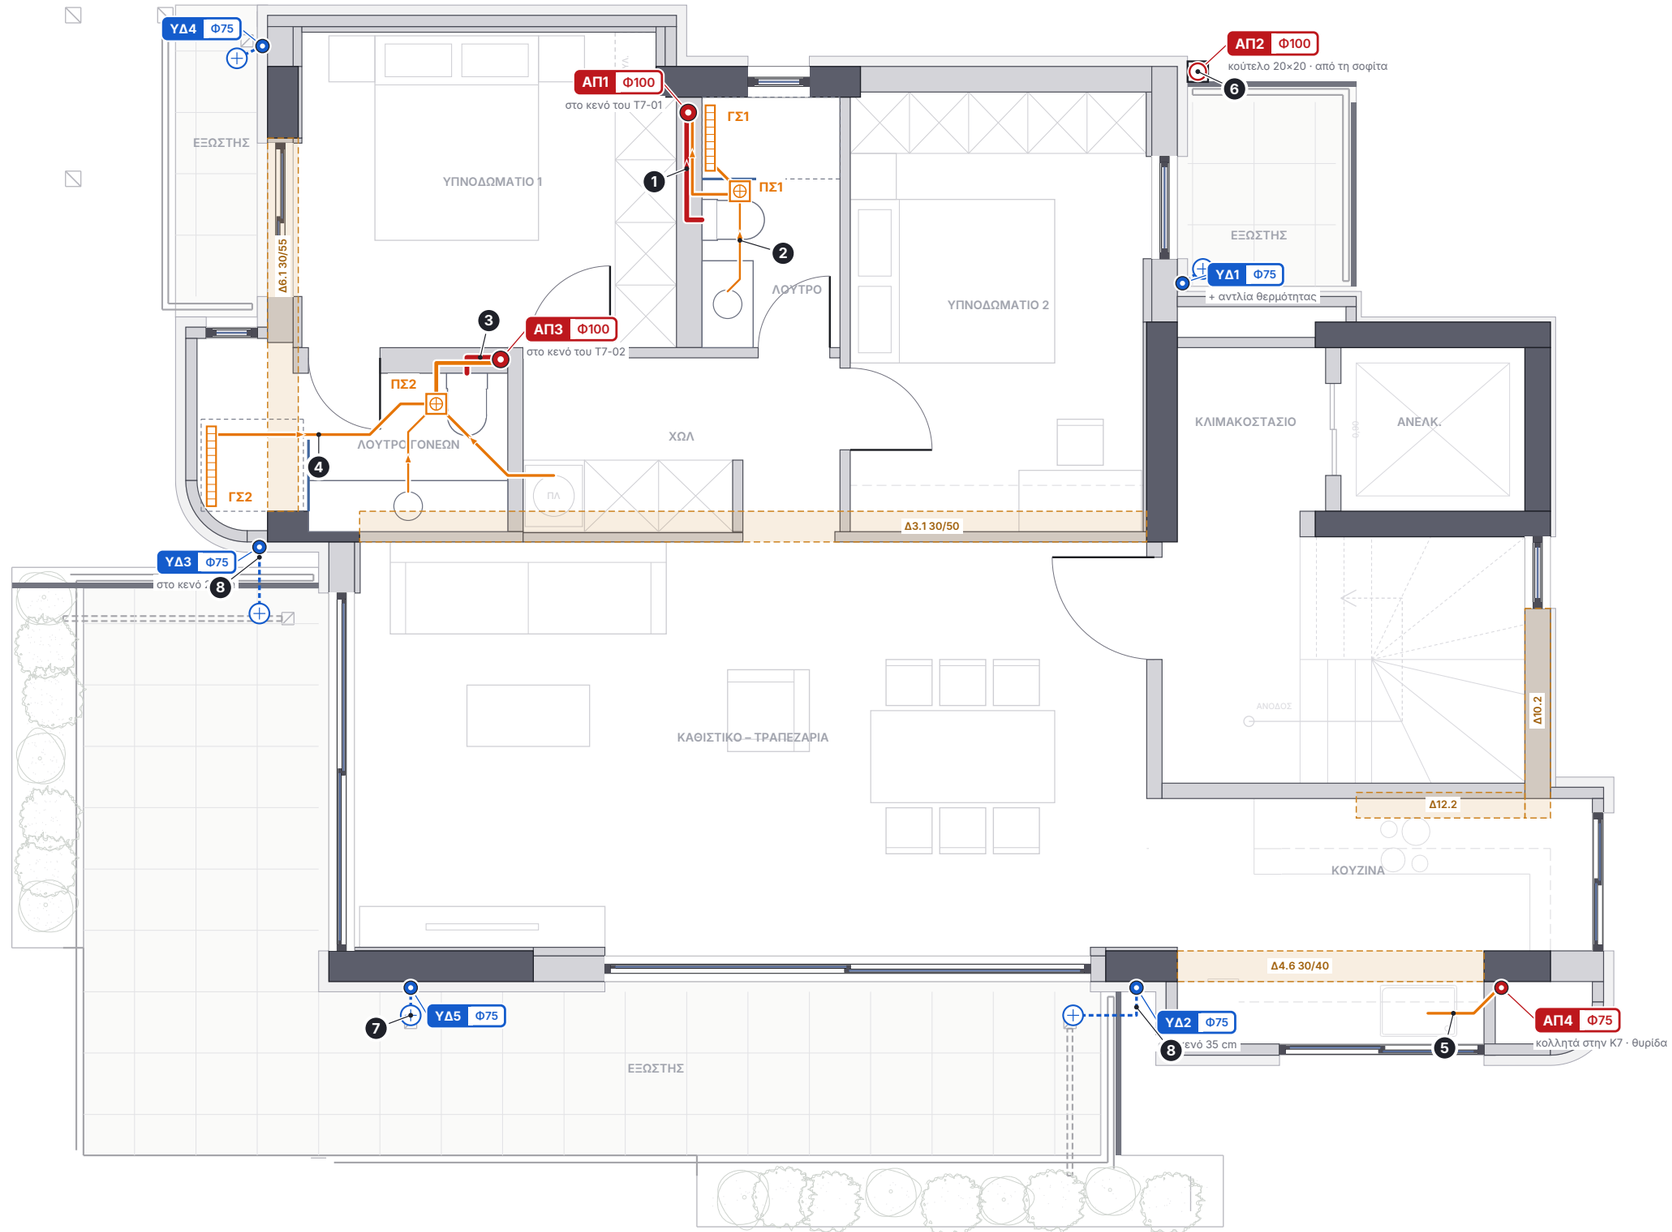

ΥΠΟΜΝΗΜΑ

- Λύματα: λεκάνη Φ90 · στήλη / αγωγός Φ100
- Ακάθαρτα: Φ40 νιπτήρας · Φ50 ντους, νεροχύτης, πλυντήριο · Φ75 έξοδος πατοσίφωνου
- Κατακόρυφη στήλη λυμάτων ΑΠ
- Στήλη που περνά / σταματά (χωρίς σύνδεση στον όροφο)
- Πατοσίφωνο ΠΣ (σιφώνι δαπέδου με σχάρα)
- Γραμμικό σιφώνι ντους ΓΣ → πατοσίφωνο
- Υδρορροή ΥΔ Φ75 μέσα στη θερμοπρόσοψη
- Σιφώνι ομβρίων εξώστη, πλευρική έξοδος
- Δοκός (ευλότυποι Σ2–Σ7) – ΚΑΜΙΑ οπή

ΣΗΜΕΙΩΣΕΙΣ


1. **Λουτρό → ΑΠ1:** λεκάνη κρεμαστή, Φ90 στο κενό του τοίχου λεκάνης Τ7-01 (+0,22). ΑΠ1 στον άξονα του κενού, 15 cm νότια της Κ2.
2. **Γραμμικό ΓΣ1 → πατοσίφωνο ΠΣ1** (Φ50). Νιπτήρας Φ40 → ΠΣ1. ΠΣ1 → ΑΠ1 Φ50 στο κενό, κάτω από τον Φ90 (+ συμπυκνώματα Α/C).
3. **Λουτρό γονέων → ΑΠ3:** λεκάνη Φ90 δεξιά, στο κενό του Τ7-02. ΑΠ3 ανάμεσα στο πλαίσιο της λεκάνης και το άκρο του τοίχου.
4. **Γραμμικό ΓΣ2 → πατοσίφωνο ΠΣ2** (Φ50, 2,4 m – το ΠΣ2 μένει δίπλα στη λεκάνη). Νιπτήρας Φ40 και πλυντήριο Φ50 (μέσα από τον Τ2Α-01) → ΠΣ2. ΠΣ2 → ΑΠ3 Φ75.
5. **Κουζίνα:** νεροχύτης Φ50 στο δάπεδο → μέσα από τον Τ4-09 → ΑΠ4 Φ75 κολλητά στη νότια παρειά της Κ7 (θυρίδα).
6. **ΑΠ2 Φ100 εξωτερική** σε κούτελο 20×20 στη ΒΑ γωνία, έξω από τη θερμοπρόσοψη: περνά χωρίς σύνδεση (παίρνει λουτρό + WC σοφίτας).
7. **Υδρορροές ΥΔ1, ΥΔ4, ΥΔ5 Φ75** μέσα στη θερμοπρόσοψη· περνούν την πλάκα του εξώστη (οπή Ø110 κολλητά στη δοκό / τοιχείο – ΑΠ-10).
8. **ΥΔ2 και ΥΔ3 ΣΤΑ ΚΕΝΑ** ανάμεσα στις πλάκες (ΥΔ2: 35 cm νότια της Κ8 · ΥΔ3: 25 cm δυτικά της Κ10), μέσα στη θερμοπρόσοψη – ΚΑΜΙΑ οπή σε εξώστη. Το σιφώνι του εξώστη βγαίνει πλευρικά από χιτώνιο Ø63 στη βάση του στηθαίου.

B

ΕΡΓΟ	ΘΕΜΑ ΣΧΕΔΙΟΥ	ΒΑΣΗ	ΑΡ. ΣΧΕΔΙΟΥ
ΠΕΝΤΑΟΡΟΦΟ ΚΤΗΡΙΟ ΚΑΤΟΙΚΙΩΝ – ΑΡΓΥΡΟΥΠΟΛΗ Κωνσταντινουπόλεως 12 & Αγ. Βαρβάρας · Ο.Τ. 103-15 Εργοδότης: INTERKAT Α.Ε. · Κατασκευή: ARKAD Ι.Κ.Ε.	**Α΄·Β΄·Γ΄ ΟΡΟΦΟΣ – ΑΠΟΧΕΤΕΥΣΗ** R17 · λύματα · ακάθαρτα · αερισμοί · όμβρια · οπές πλακών Τυπικός όροφος (Β1) · λεπτομέρειες στο ΑΠ-07	Σ4 / Σ5 · τοιχοποιίες τυπικού R25	**ΑΠ-03** **Κλίμακα 1:60 · Α3** 10/11/2026 · R17

ΚΑΤΟΨΗ Δ΄ ΟΡΟΦΟΥ – ΑΠΟΧΕΤΕΥΣΗ & ΥΔΡΟΡΡΟΕΣ

Κλίμακα 1:60

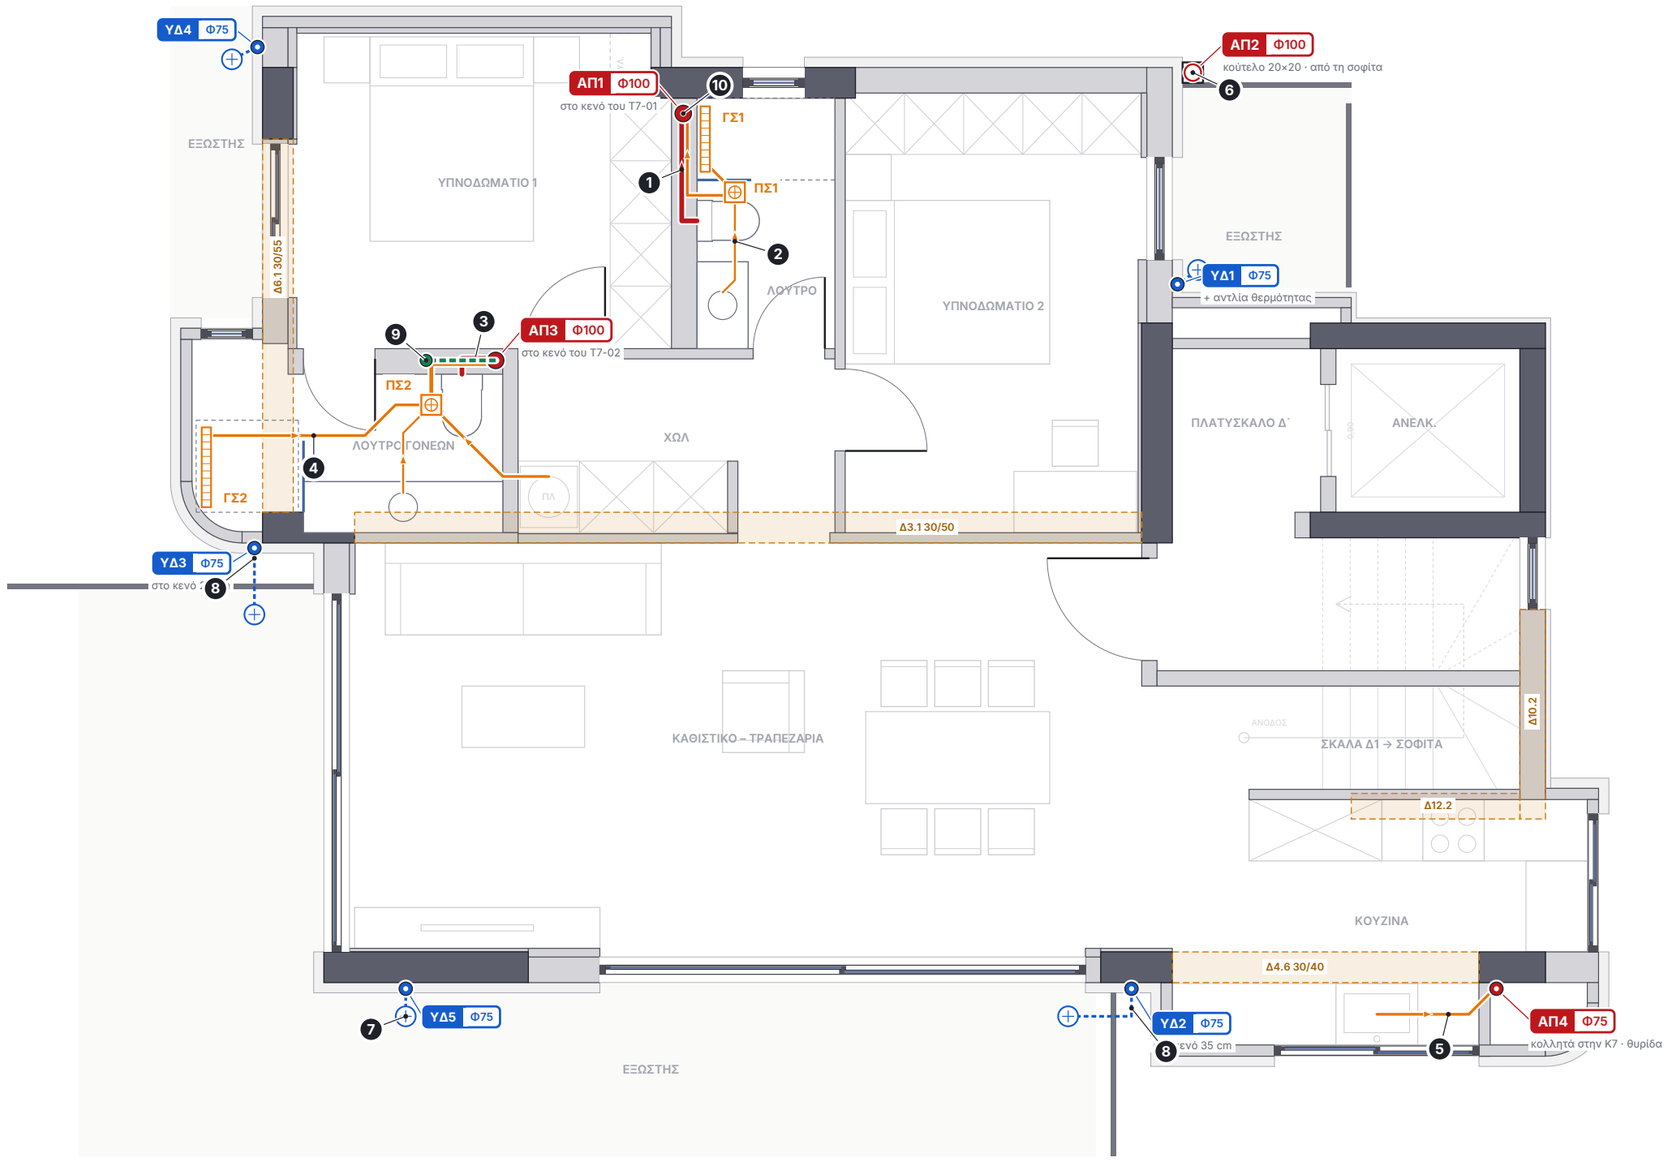

0 1 2 5 m

ΥΠΟΜΝΗΜΑ

- Λύματα: λεκάνη Φ90 · στήλη / αγωγός Φ100
- Ακάθαρτα: Φ40 νιπτήρας · Φ50 ντους, νεροχύτης, πλυντήριο · Φ75 έξοδος πατοσίφωνου
- Κατακόρυφη στήλη λυμάτων ΑΠ
- Στήλη που περνά / σταματά (χωρίς σύνδεση στον όροφο)
- Πατοσίφωνο ΠΣ (σιφώνι δαπέδου με σχάρα)
- Γραμμικό σιφώνι ντους ΓΣ → πατοσίφωνο
- Υδρορροή ΥΔ Φ75 μέσα στη θερμοπρόσοψη
- Σιφώνι ομβρίων εξώστη, πλευρική έξοδος
- Δοκός (ξυλότυποι Σ2–Σ7) – ΚΑΜΙΑ οπή
- Αερισμός ΚΑ Φ75 (βγαίνει έξω και ανεβαίνει στη θερμοπρόσοψη)

ΣΗΜΕΙΩΣΕΙΣ


1. **Λουτρό → ΑΠ1:** λεκάνη κρεμαστή, Φ90 στο κενό του τοίχου λεκάνης Τ7-01 (+0,22). ΑΠ1 στον άξονα του κενού, 15 cm νότια της Κ2.
2. **Γραμμικό ΓΣ1 → πατοσίφωνο ΠΣ1** (Φ50). Νιπτήρας Φ40 → ΠΣ1. ΠΣ1 → ΑΠ1 Φ50 στο κενό, κάτω από τον Φ90 (+ συμπυκνώματα Α/C).
3. **Λουτρό γονέων → ΑΠ3:** λεκάνη Φ90 δεξιά, στο κενό του Τ7-02. ΑΠ3 ανάμεσα στο πλαίσιο της λεκάνης και το άκρο του τοίχου.
4. **Γραμμικό ΓΣ2 → πατοσίφωνο ΠΣ2** (Φ50, 2,4 m – το ΠΣ2 μένει δίπλα στη λεκάνη). Νιπτήρας Φ40 και πλυντήριο Φ50 (μέσα από τον Τ2Α-01) → ΠΣ2. ΠΣ2 → ΑΠ3 Φ75.
5. **Κουζίνα:** νεροχύτης Φ50 στο δάπεδο → μέσα από τον Τ4-09 → ΑΠ4 Φ75 κολλητά στη νότια παρειά της Κ7 (θυρίδα).
6. **ΑΠ2 Φ100 εξωτερική** σε κούτελο 20×20 στη ΒΑ γωνία, έξω από τη θερμοπρόσοψη: περνά χωρίς σύνδεση (παίρνει λουτρό + WC σοφίτας).
7. **Υδρορροές ΥΔ1, ΥΔ4, ΥΔ5 Φ75** μέσα στη θερμοπρόσοψη· περνούν την πλάκα του εξώστη (οπή Ø110 κολλητά στη δοκό / τοιχείο – ΑΠ-10).
8. **ΥΔ2 και ΥΔ3 ΣΤΑ ΚΕΝΑ** ανάμεσα στις πλάκες (ΥΔ2: 35 cm νότια της Κ8 · ΥΔ3: 25 cm δυτικά της Κ10), μέσα στη θερμοπρόσοψη – ΚΑΜΙΑ οπή σε εξώστη. Το σιφώνι του εξώστη βγαίνει πλευρικά από χιτώνιο Ø63 στη βάση του στηθαίου.
9. **ΚΑ3:** ο αερισμός της ΑΠ3 φεύγει 0,7 m στην οροφή του Δ΄ (στο κενό του Τ7-02) ως τον δυτικό τοίχο της σοφίτας (2,40 / 3,365) και ανεβαίνει στη θερμοπρόσοψη.
10. **ΑΠ1:** τελευταία σύνδεση. Ο αερισμός ΚΑ1 συνεχίζει στο γέμισμα του δαπέδου της σοφίτας (ΑΠ-05).

B

ΕΡΓΟ	ΘΕΜΑ ΣΧΕΔΙΟΥ	ΒΑΣΗ	ΑΡ. ΣΧΕΔΙΟΥ
ΠΕΝΤΑΟΡΟΦΟ ΚΤΗΡΙΟ ΚΑΤΟΙΚΙΩΝ – ΑΡΓΥΡΟΥΠΟΛΗ Κωνσταντινουπόλεως 12 & Αγ. Βαρβάρας · Ο.Τ. 103-15 Εργοδότης: INTERKAT Α.Ε. · Κατασκευή: ARKAD Ι.Κ.Ε.	**Δ΄ ΟΡΟΦΟΣ – ΑΠΟΧΕΤΕΥΣΗ** R17 · λύματα · ακάθαρτα · αερισμοί · όμβρια · οπές πλακών Δ1 κάτω επίπεδο · λουτρά όπως ο τυπικός (ΑΠ-07)	Σ7 · τοιχοποιίες Δ΄ R04	**ΑΠ-04** **Κλίμακα 1:60 · Α3** 10/11/2026 · R17

ΚΑΤΟΨΗ ΣΟΦΙΤΑΣ – ΑΠΟΧΕΤΕΥΣΗ & ΑΕΡΙΣΜΟΙ

Κλίμακα 1:60

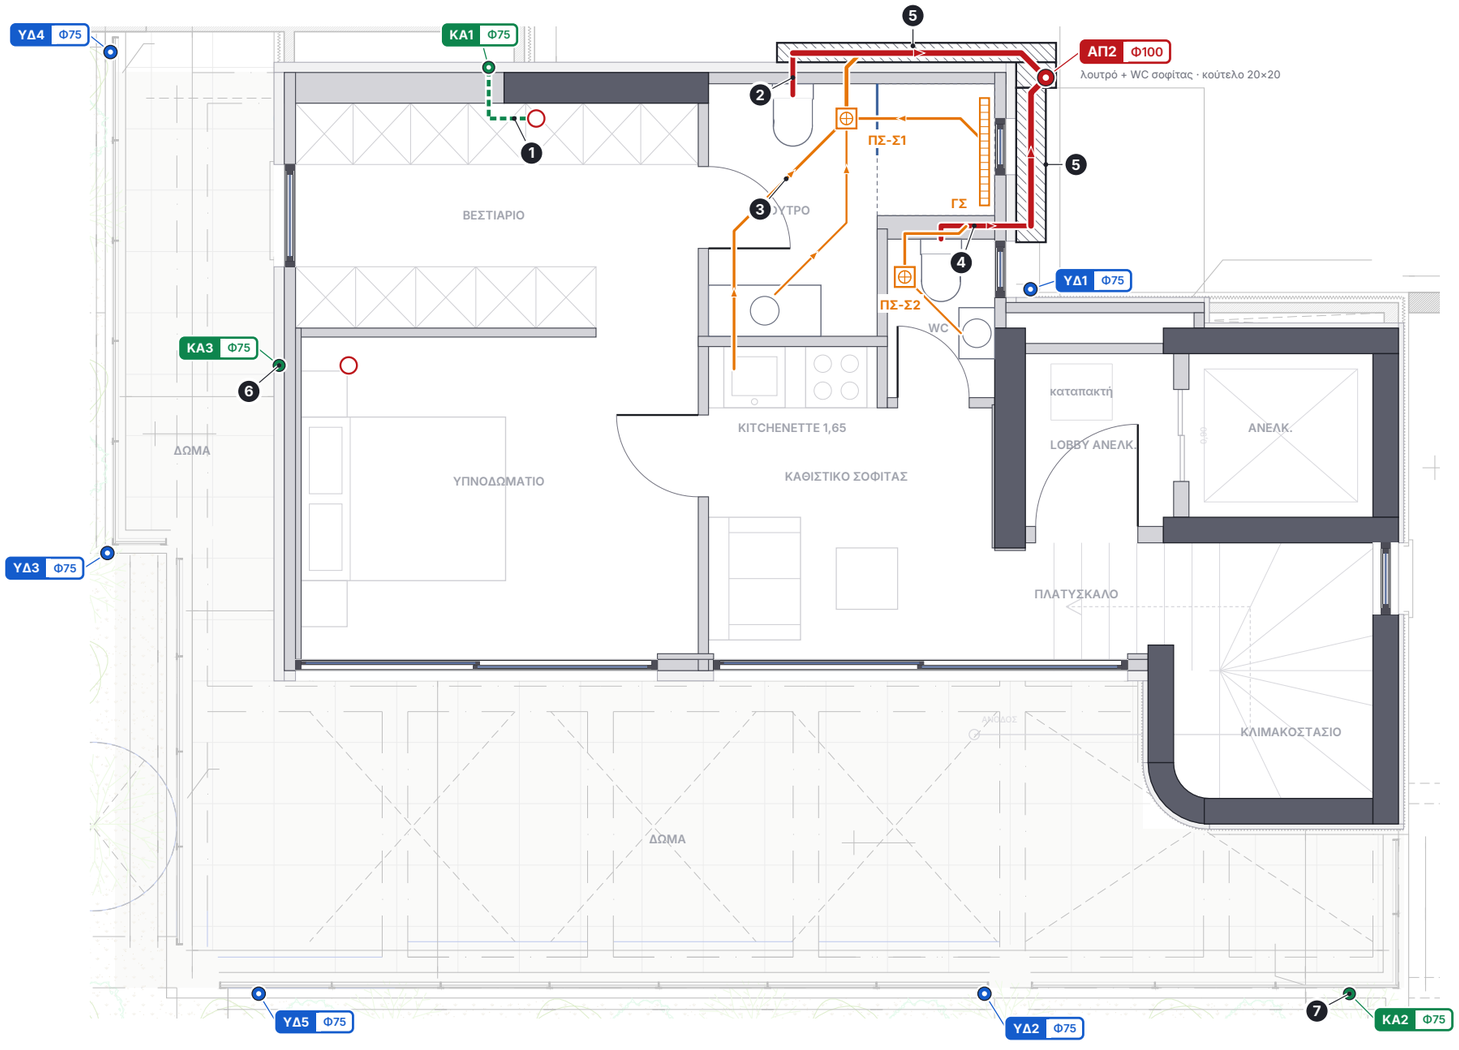

ΥΠΟΜΝΗΜΑ

- Λύματα: λεκάνη Φ90 · στήλη / αγωγός Φ100
- Ακάθαρτα: Φ40 νιπτήρας · Φ50 ντους, νεροχύτης, πλυντήριο · Φ75 έξοδος πατοσίφωνου
- Αερισμός ΚΑ Φ75 (βγαίνει έξω και ανεβαίνει στη θερμοπρόσοψη)
- Κατακόρυφη στήλη λυμάτων ΑΠ
- Στήλη που περνά / σταματά (χωρίς σύνδεση στον όροφο)
- Πατοσίφωνο ΠΣ (σιφώνι δαπέδου με σχάρα)
- Γραμμικό σιφώνι ντους ΓΣ → πατοσίφωνο
- Κούτελο (κλειστό κανάλι γύρω από αγωγό)
- Άνοδος αερισμού στη θερμοπρόσοψη
- Υδρορροή ΥΔ Φ75 μέσα στη θερμοπρόσοψη

ΣΗΜΕΙΩΣΕΙΣ

1. **ΑΠ1:** δεν ανεβαίνει στη σοφίτα. Ο αερισμός ΚΑ1 Φ75 φεύγει μέσα στο γέμισμα του δαπέδου, βγαίνει έξω δυτικά του Κ2 και ανεβαίνει στη θερμοπρόσοψη ως τη στέγη.
2. **Λουτρό:** δική του έξοδος από τον βόρειο τοίχο – λεκάνη Φ90 ίσια έξω.
3. **Γραμμικό ντους → πατοσίφωνο ΠΣ-Σ1** (Φ50). Νιπτήρας Φ40 και KITCHENETTE Φ50 (2,8 m μέσα στο γέμισμα) επίσης στο ΠΣ-Σ1. ΠΣ-Σ1 → έξω Φ75.
4. **WC:** δική του έξοδος από τον ανατολικό τοίχο – λεκάνη Φ90 μέσα στον Τ7Α-02. Νιπτήρας Φ40 → ΠΣ-Σ2 → Φ50 στον ίδιο τοίχο.
5. **Εξωτερικοί Φ100 σε ΚΟΥΤΕΛΟ** θερμοπρόσοψης 20×20 στη στάθμη της πλάκας +16,05: βόρεια όψη 2,5 m, ανατολική 1,5 m, κλίση 2 %. Ενώνονται έξω στη ΒΑ γωνία → ΑΠ2 Φ100 σε κατακόρυφο κούτελο 20×20.
6. **ΚΑ3:** αερισμός της ΑΠ3 στη θερμοπρόσοψη του δυτικού τοίχου (2,40 / 3,365).
7. **ΚΑ2:** αερισμός της ΑΠ4 (κολλητά στην Κ7) – 1,3 m στο δώμα ως τον καμπύλο τοίχο του κλιμακοστασίου → στέγη.
8. **Υδρορροές:** ΥΔ2–ΥΔ5 από τα σιφώνια των δωμάτων +16,05 (οπές Σ7 στο ΑΠ-10) · ΥΔ1 από τη στέγη. Κάτω από το Σ7 οι ΥΔ2 / ΥΔ3 κατεβαίνουν στα κενά.


ΓΕΜΙΣΜΑ ΔΑΠΕΔΟΥ ΣΟΦΙΤΑΣ 20 cm

- Πλάκα +16,05 → τελικό δάπεδο +16,25 = 20 cm (κάτοψη Α-10-S και τομή Α-30-ΒΒ της μελέτης εφαρμογής). Το δώμα είναι +16,20.
- Μέσα στα 20 cm χωράνε ο ΚΑ1 Φ75 και η kitchenette Φ50 με 2 % (πτώση 6 cm), κάτω από την ενδοδαπέδια.
- Η kitchenette έχει δικό της σιφώνι· το ΠΣ-Σ1 με ξεβιδωτή σχάρα για καθαρισμό (λίπη).


ΕΡΓΟ	ΘΕΜΑ ΣΧΕΔΙΟΥ	ΒΑΣΗ	ΑΡ. ΣΧΕΔΙΟΥ
ΠΕΝΤΑΟΡΟΦΟ ΚΤΗΡΙΟ ΚΑΤΟΙΚΙΩΝ – ΑΡΓΥΡΟΥΠΟΛΗ Κωνσταντινουπόλεως 12 & Αγ. Βαρβάρας · Ο.Τ. 103-15 Εργοδότης: INTERKAT Α.Ε. · Κατασκευή: ARKAD Ι.Κ.Ε.	**ΣΟΦΙΤΑ – ΑΠΟΧΕΤΕΥΣΗ & ΑΕΡΙΣΜΟΙ** R17 · λύματα · ακάθαρτα · αερισμοί · όμβρια · οπές πλακών Δ1 πάνω επίπεδο · έξοδοι λουτρού / WC · κούτελα · λεπτομέρεια στο ΑΠ-08	A-10-S · A-30-ΒΒ · Σ7 / Σ8 · τοιχοποιίες σοφίτας R04	**ΑΠ-05** **Κλίμακα 1:60 · A3** 10/11/2026 · R17

ΙΣΟΓΕΙΟ – ΛΕΠΤΟΜΕΡΕΙΕΣ ΥΓΡΩΝ ΧΩΡΩΝ


Κλίμακα 1:25

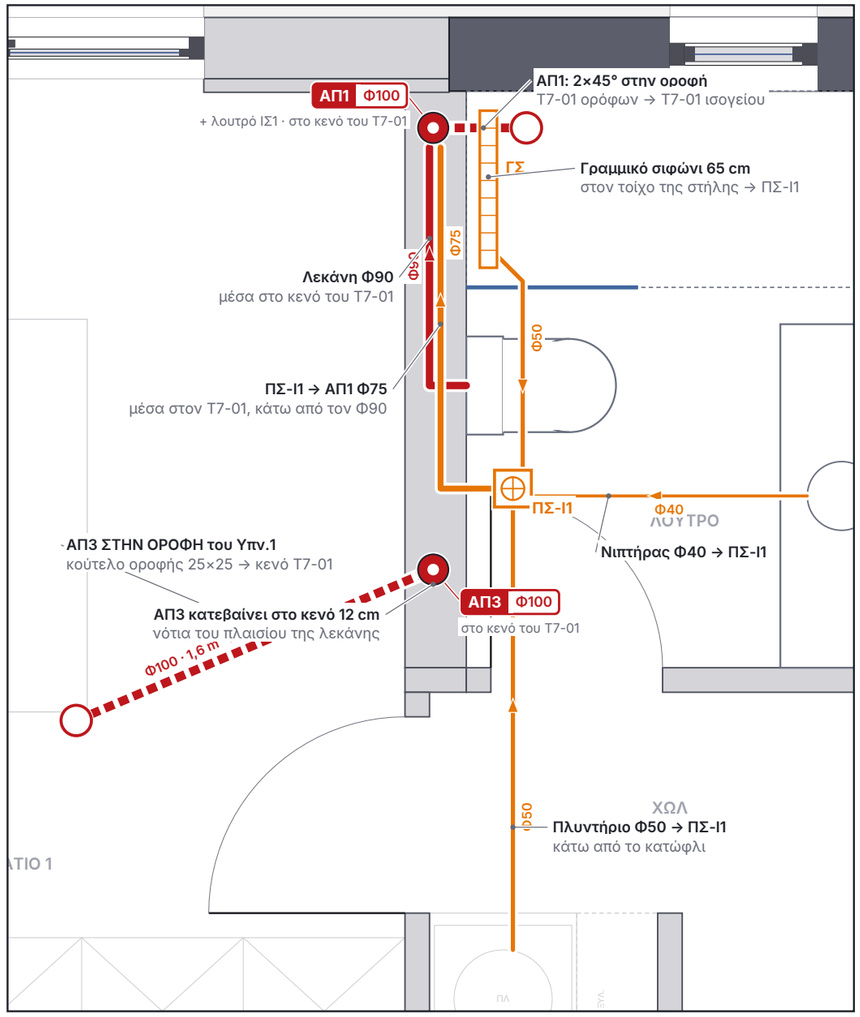

1 ΛΟΥΤΡΟ ΙΣΟΓΕΙΟΥ → ΑΠ1 · ΑΠ3 ΣΤΟ ΚΕΝΟ ΤΟΥ Τ7-01 Κλίμακα 1:25

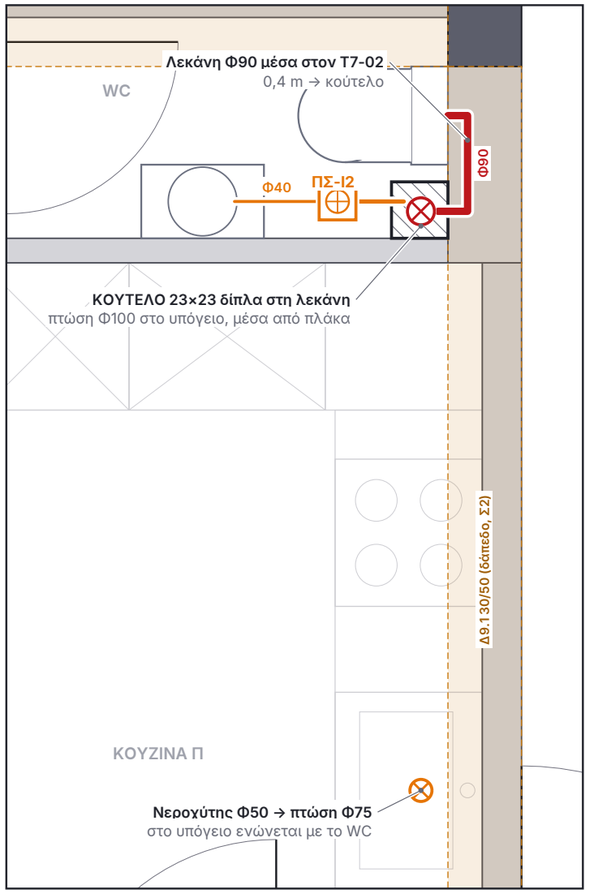

2 WC + ΚΟΥΖΙΝΑ – ΚΟΥΤΕΛΟ Κλίμακα 1:25

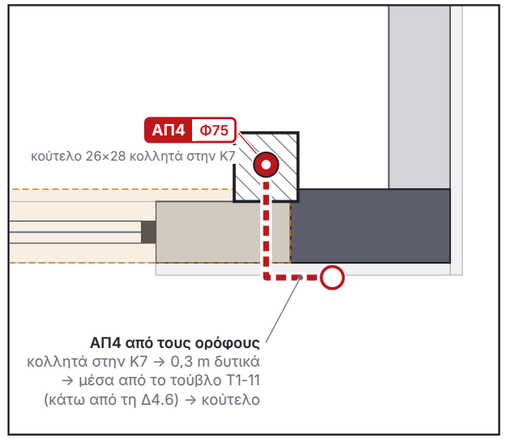

3 ΑΠ4 ΣΤΗΝ Κ7 Κλίμακα 1:25

ΥΠΟΜΝΗΜΑ

- Λύματα: λεκάνη Φ90 · στήλη / αγωγός Φ100
- Ακάθαρτα: Φ40 νιπτήρας · Φ50 ντους, νεροχύτης, πλυντήριο · Φ75 έξοδος πατοσίφωνου
- Αγωγός στην οροφή του ορόφου (μετατόπιση στήλης 2×45°)
- Κατακόρυφη στήλη λυμάτων ΑΠ
- Στήλη που περνά / σταματά (χωρίς σύνδεση στον όροφο)
- Πτώση στον κάτω όροφο
- Πατοσίφωνο ΠΣ (σιφώνι δαπέδου με σχάρα)
- Γραμμικό σιφώνι ντους ΓΣ → πατοσίφωνο
- Κούτελο (κλειστό κανάλι γύρω από αγωγό)
- Δοκός (ξυλότυποι Σ2–Σ7) – ΚΑΜΙΑ οπή

ΓΕΝΙΚΑ


- Κλίσεις: Φ40–Φ50 2 % · Φ75–Φ100 2 % (ελάχιστη 1 %). Όλα τα οριζόντια μέσα στο γέμισμα του δαπέδου ή μέσα στους τοίχους λεκάνης – τίποτα σε οροφή διαμερίσματος εκτός από τις μετατοπίσεις του ισογείου.
- Κάθε γραμμικό σιφώνι ντους αποχετεύει στο πατοσίφωνο του χώρου· στο ίδιο πατοσίφωνο ο νιπτήρας (και πλυντήριο / kitchenette όπου υπάρχει). Γραμμικά ΧΩΡΙΣ δική τους οσμοπαγίδα (παγίδα = το πατοσίφωνο).
- Έξοδος πατοσίφωνου Φ75 όπου μπαίνει πλυντήριο ή kitchenette (ΠΣ2, ΠΣ-Ι1, ΠΣ-Σ1), αλλιώς Φ50.
- ΚΑΜΙΑ οπή σε δοκό. Διελεύσεις πλακών με χιτώνιο + πυροφραγή. Δοκιμή στεγανότητας πριν από το γέμισμα.
- Στήλες ΑΠ1 / ΑΠ3 και οι μετατοπίσεις τους: ΗΧΟΜΟΝΩΤΙΚΟΣ σωλήνας PP τριών στρώσεων. Λοιπά U-PVC 6 atm (αερισμοί 4 atm).
- Οι στήλες των λουτρών στον άξονα του ΚΕΝΟΥ 12 cm των τοίχων λεκάνης Τ7 – μούφες ανάμεσα στους ορθοστάτες. Οπές πλακών: ΑΠ-10 / ΑΠ-11.

B


ΕΡΓΟ	ΘΕΜΑ ΣΧΕΔΙΟΥ	ΒΑΣΗ	ΑΡ. ΣΧΕΔΙΟΥ
ΠΕΝΤΑΟΡΟΦΟ ΚΤΗΡΙΟ ΚΑΤΟΙΚΙΩΝ – ΑΡΓΥΡΟΥΠΟΛΗ Κωνσταντινουπόλεως 12 & Αγ. Βαρβάρας · Ο.Τ. 103-15 Εργοδότης: INTERKAT Α.Ε. · Κατασκευή: ARKAD Ι.Κ.Ε.	**ΙΣΟΓΕΙΟ – ΛΕΠΤΟΜΕΡΕΙΕΣ ΥΓΡΩΝ ΧΩΡΩΝ** R17 · λύματα · ακάθαρτα · αερισμοί · όμβρια · οπές πλακών Λουτρό · WC / κουζίνα · ΑΠ4 στην Κ7	ΑΠ-02 · τοιχοποιίες ισογείου R13	**ΑΠ-06** **Κλίμακα 1:25 · Α3** 10/11/2026 · R17

Α΄ · Β΄ · Γ΄ · Δ΄ ΟΡΟΦΟΣ – ΛΕΠΤΟΜΕΡΕΙΕΣ ΥΓΡΩΝ ΧΩΡΩΝ


Κλίμακα 1:25

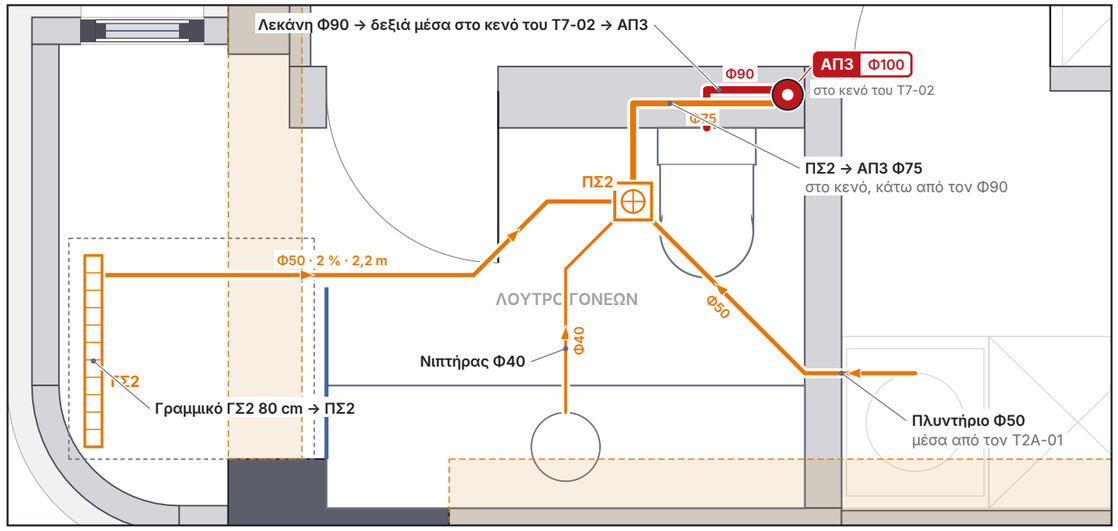


1 **ΛΟΥΤΡΟ ΓΟΝΕΩΝ → ΑΠ3** Κλίμακα 1:25

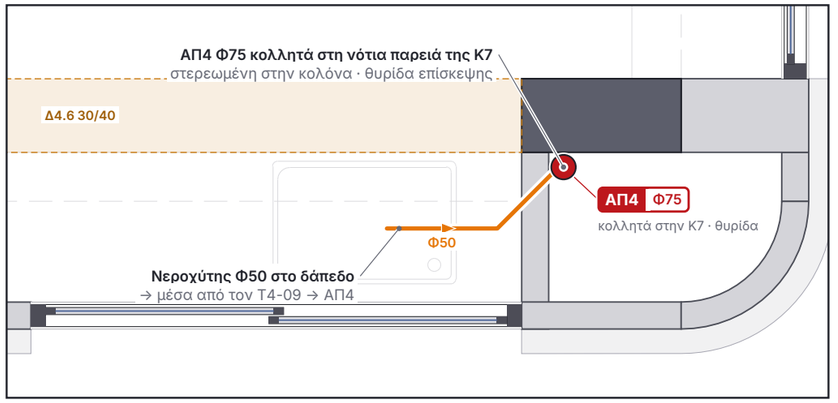


3 **ΚΟΥΖΙΝΑ → ΑΠ4 ΚΟΛΛΗΤΑ ΣΤΗΝ Κ7** Κλίμακα 1:25

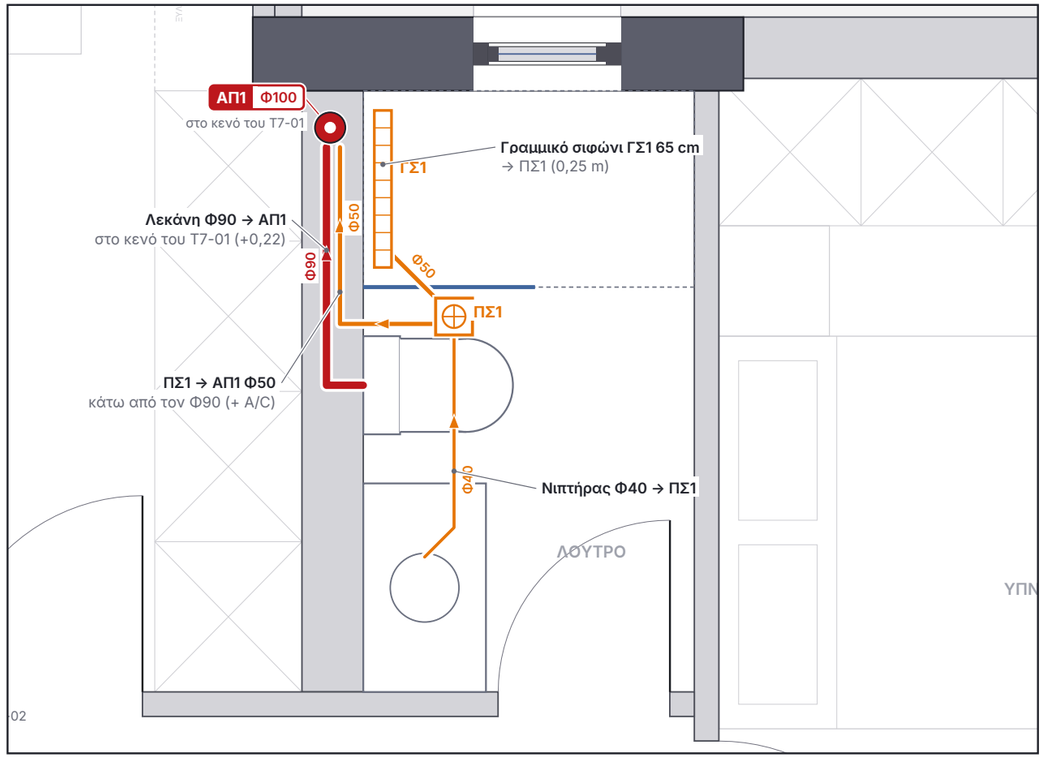

2 **ΛΟΥΤΡΟ → ΑΠ1** Κλίμακα 1:25

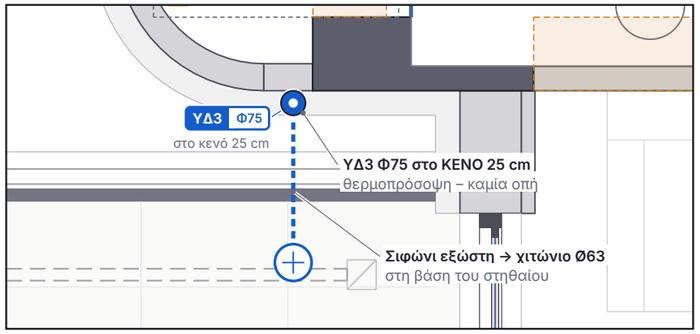

4 **ΥΔ3 ΣΤΟ ΚΕΝΟ 25 cm (Κ10)** Κλίμακα 1:25

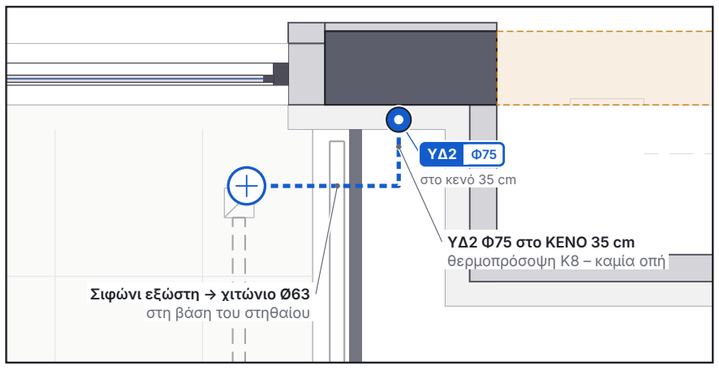

5 **ΥΔ2 ΣΤΟ ΚΕΝΟ 35 cm (Κ8)** Κλίμακα 1:25

ΥΠΟΜΝΗΜΑ

- Λύματα: λεκάνη Φ90 · στήλη / αγωγός Φ100
- Ακάθαρτα: Φ40 νιπτήρας · Φ50 ντους, νεροχύτης, πλυντήριο · Φ75 έξοδος πατοσίφωνου
- Κατακόρυφη στήλη λυμάτων ΑΠ
- Στήλη που περνά / σταματά (χωρίς σύνδεση στον όροφο)
- Πατοσίφωνο ΠΣ (σιφώνι δαπέδου με σχάρα)
- Γραμμικό σιφώνι ντους ΓΣ → πατοσίφωνο
- Υδρορροή ΥΔ Φ75 μέσα στη θερμοπρόσοψη
- Σιφώνι ομβρίων εξώστη, πλευρική έξοδος
- Δοκός (ξυλότυποι Σ2–Σ7) – ΚΑΜΙΑ οπή

ΓΕΝΙΚΑ


- Κλίσεις: Φ40–Φ50 2 % · Φ75–Φ100 2 % (ελάχιστη 1 %). Όλα τα οριζόντια μέσα στο γέμισμα του δαπέδου ή μέσα στους τοίχους λεκάνης – τίποτα σε οροφή διαμερίσματος εκτός από τις μετατοπίσεις του ισογείου.
- Κάθε γραμμικό σιφώνι ντους αποχετεύει στο πατοσίφωνο του χώρου· στο ίδιο πατοσίφωνο ο νιπτήρας (και πλυντήριο / kitchenette όπου υπάρχει). Γραμμικά ΧΩΡΙΣ δική τους οσμοπαγίδα (παγίδα = το πατοσίφωνο).
- Έξοδος πατοσίφωνου Φ75 όπου μπαίνει πλυντήριο ή kitchenette (ΠΣ2, ΠΣ-Ι1, ΠΣ-Σ1), αλλιώς Φ50.
- ΚΑΜΙΑ οπή σε δοκό. Διελεύσεις πλακών με χιτώνιο + πυροφραγή. Δοκιμή στεγανότητας πριν από το γέμισμα.
- Στήλες ΑΠ1 / ΑΠ3 και οι μετατοπίσεις τους: ΗΧΟΜΟΝΩΤΙΚΟΣ σωλήνας PP τριών στρώσεων. Λοιπά U-PVC 6 atm (αερισμοί 4 atm).
- Οι στήλες των λουτρών στον άξονα του ΚΕΝΟΥ 12 cm των τοίχων λεκάνης Τ7 – μούφες ανάμεσα στους ορθοστάτες. Οπές πλακών: ΑΠ-10 / ΑΠ-11.

B

ΕΡΓΟ	ΘΕΜΑ ΣΧΕΔΙΟΥ	ΒΑΣΗ	ΑΡ. ΣΧΕΔΙΟΥ
ΠΕΝΤΑΟΡΟΦΟ ΚΤΗΡΙΟ ΚΑΤΟΙΚΙΩΝ – ΑΡΓΥΡΟΥΠΟΛΗ Κωνσταντινουπόλεως 12 & Αγ. Βαρβάρας · Ο.Τ. 103-15 Εργοδότης: INTERKAT Α.Ε. · Κατασκευή: ARKAD Ι.Κ.Ε.	**Α΄·Β΄·Γ΄·Δ΄ – ΛΕΠΤΟΜΕΡΕΙΕΣ ΥΓΡΩΝ ΧΩΡΩΝ** R17 · λύματα · ακάθαρτα · αερισμοί · όμβρια · οπές πλακών Λουτρό γονέων · λουτρό · κουζίνα · υδρορροές στα κενά (ίδια και στον Δ΄)	ΑΠ-03 / ΑΠ-04 · τοιχοποιίες τυπικού R25	**ΑΠ-07** **Κλίμακα 1:25 · Α3** 10/11/2026 · R17

ΣΟΦΙΤΑ – ΛΕΠΤΟΜΕΡΕΙΑ ΥΓΡΩΝ ΧΩΡΩΝ

Κλίμακα 1:20

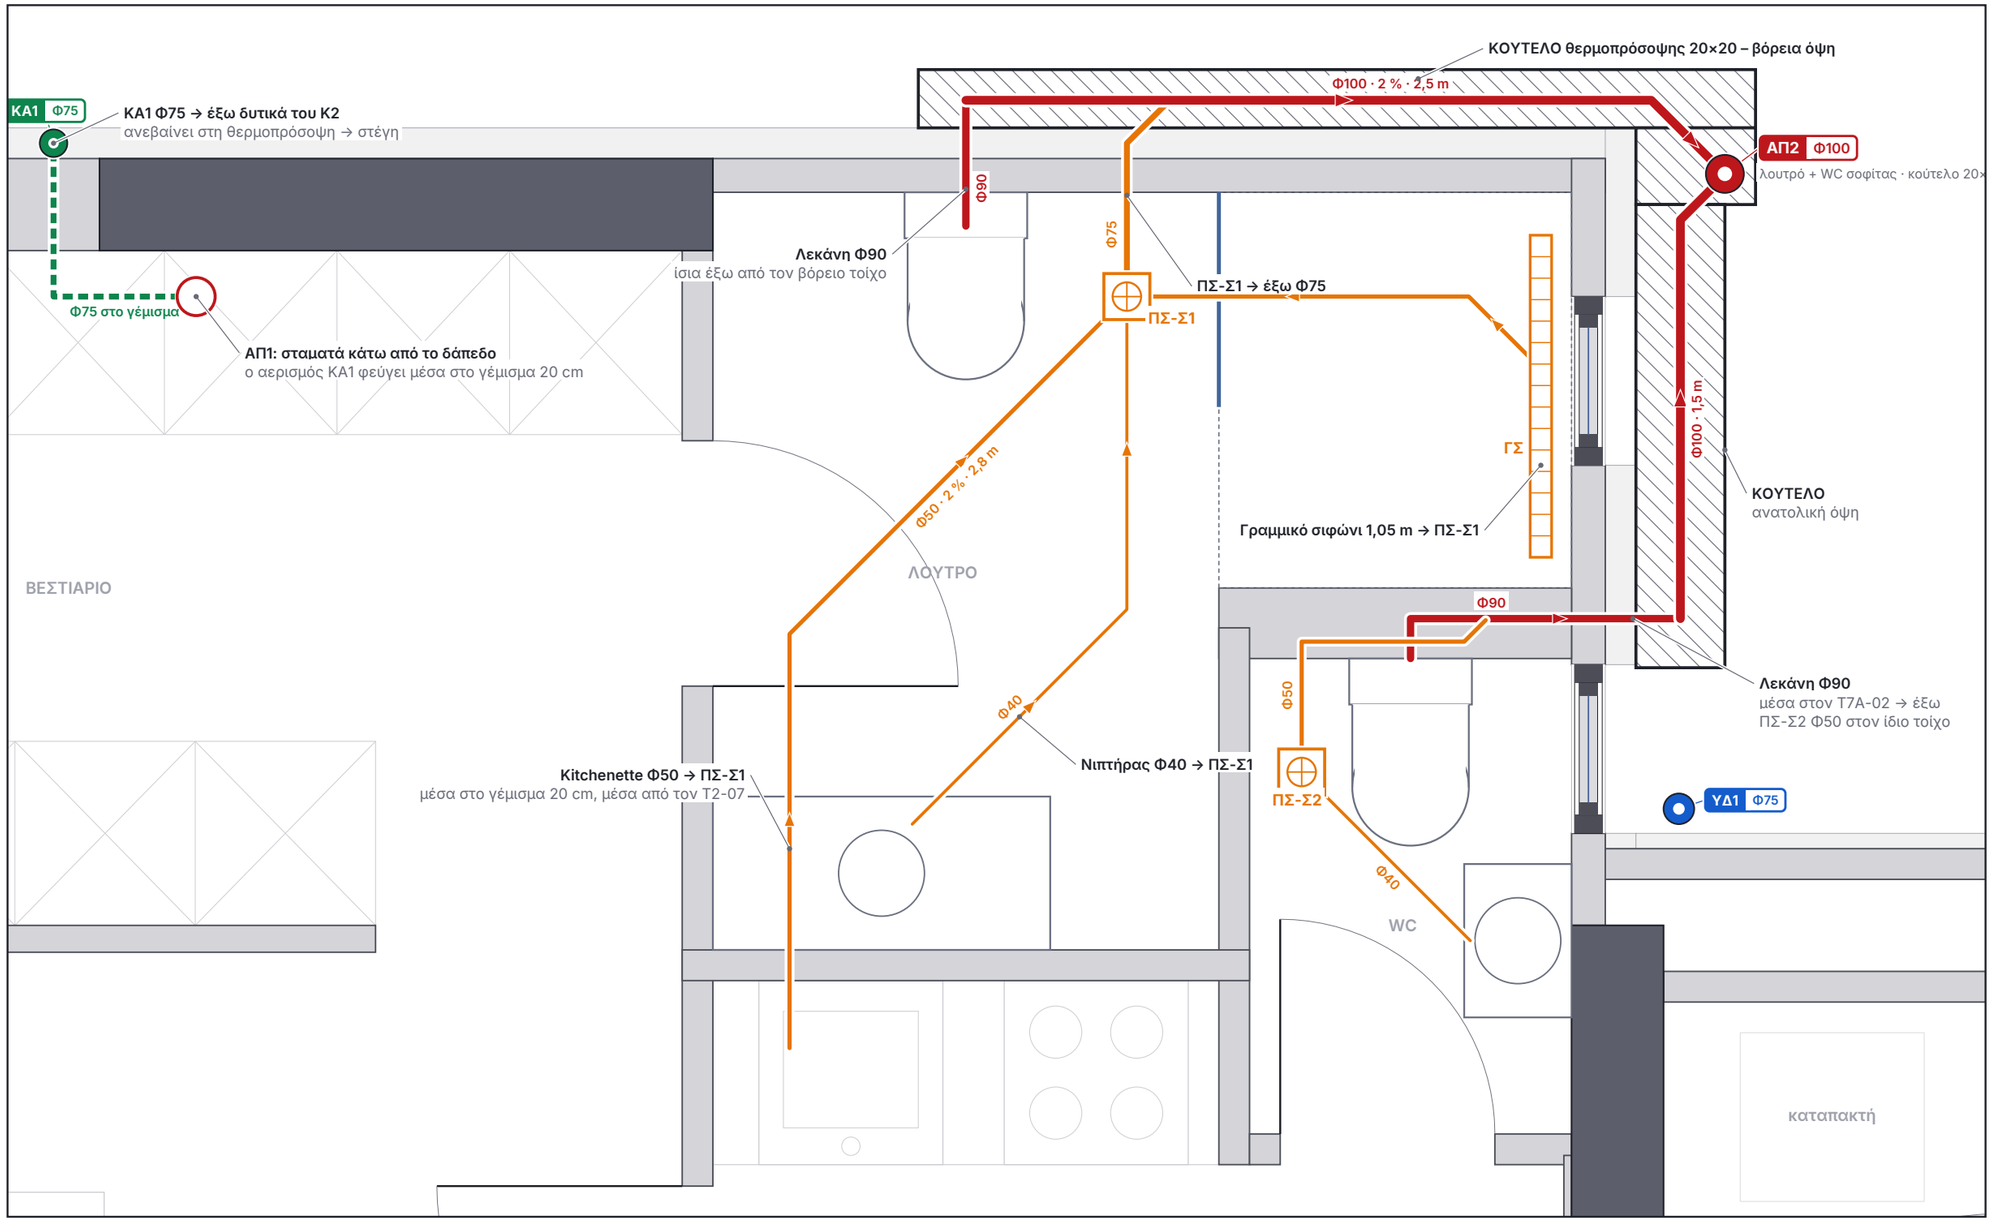

1 **ΛΟΥΤΡΟ · WC · ΚΙΤCHENETTE ΣΟΦΙΤΑΣ – ΕΞΟΔΟΙ & ΚΟΥΤΕΛΑ → ΑΠ2** Κλίμακα 1:20

ΥΠΟΜΝΗΜΑ

- Λύματα: λεκάνη Φ90 · στήλη / αγωγός Φ100
- Ακάθαρτα: Φ40 νιπτήρας · Φ50 ντους, νεροχύτης, πλυντήριο · Φ75 έξοδος πατοσίφωνου
- Αερισμός ΚΑ Φ75 (βγαίνει έξω και ανεβαίνει στη θερμοπρόσοψη)
- Κατακόρυφη στήλη λυμάτων ΑΠ
- Στήλη που περνά / σταματά (χωρίς σύνδεση στον όροφο)
- Πατοσίφωνο ΠΣ (σιφώνι δαπέδου με σχάρα)
- Γραμμικό σιφώνι ντους ΓΣ → πατοσίφωνο
- Κούτελο (κλειστό κανάλι γύρω από αγωγό)
- Άνοδος αερισμού στη θερμοπρόσοψη

ΓΕΝΙΚΑ

- Κλίσεις: Φ40–Φ50 2 % · Φ75–Φ100 2 % (ελάχιστη 1 %). Όλα τα οριζόντια μέσα στο γέμισμα του δαπέδου ή μέσα στους τοίχους λεκάνης – τίποτα σε οροφή διαμερίσματος εκτός από τις μετατοπίσεις του ισογείου.
- Κάθε γραμμικό σιφώνι ντους αποχετεύει στο πατοσίφωνο του χώρου· στο ίδιο πατοσίφωνο ο νιπτήρας (και πλυντήριο / kitchenette όπου υπάρχει). Γραμμικά ΧΩΡΙΣ δική τους οσμοπαγίδα (παγίδα = το πατοσίφωνο).
- Έξοδος πατοσίφωνου Φ75 όπου μπαίνει πλυντήριο ή kitchenette (ΠΣ2, ΠΣ-Ι1, ΠΣ-Σ1), αλλιώς Φ50.
- ΚΑΜΙΑ οπή σε δοκό. Διελεύσεις πλακών με χιτώνιο + πυροφραγή. Δοκιμή στεγανότητας πριν από το γέμισμα.
- Στήλες ΑΠ1 / ΑΠ3 και οι μετατοπίσεις τους: ΗΧΟΜΟΝΩΤΙΚΟΣ σωλήνας PP τριών στρώσεων. Λοιπά U-PVC 6 atm (αερισμοί 4 atm).
- Οι στήλες των λουτρών στον άξονα του ΚΕΝΟΥ 12 cm των τοίχων λεκάνης Τ7 – μούφες ανάμεσα στους ορθοστάτες. Οπές πλακών: ΑΠ-10 / ΑΠ-11.

ΓΕΜΙΣΜΑ ΔΑΠΕΔΟΥ ΣΟΦΙΤΑΣ 20 cm


- Πλάκα +16,05 → τελικό δάπεδο +16,25 = 20 cm (κάτοψη Α-10-S και τομή Α-30-ΒΒ της μελέτης εφαρμογής). Το δώμα είναι +16,20.
- Μέσα στα 20 cm χωράνε ο ΚΑ1 Φ75 και η kitchenette Φ50 με 2 % (πτώση 6 cm), κάτω από την ενδοδαπέδια.
- Η kitchenette έχει δικό της σιφώνι· το ΠΣ-Σ1 με ξεβιδωτή σχάρα για καθαρισμό (λίπη).

B

ΕΡΓΟ	ΘΕΜΑ ΣΧΕΔΙΟΥ	ΒΑΣΗ	ΑΡ. ΣΧΕΔΙΟΥ
ΠΕΝΤΑΟΡΟΦΟ ΚΤΗΡΙΟ ΚΑΤΟΙΚΙΩΝ – ΑΡΓΥΡΟΥΠΟΛΗ Κωνσταντινουπόλεως 12 & Αγ. Βαρβάρας · Ο.Τ. 103-15 Εργοδότης: INTERKAT Α.Ε. · Κατασκευή: ARKAD Ι.Κ.Ε.	**ΣΟΦΙΤΑ – ΛΕΠΤΟΜΕΡΕΙΑ ΥΓΡΩΝ ΧΩΡΩΝ** R17 · λύματα · ακάθαρτα · αερισμοί · όμβρια · οπές πλακών Λουτρό · WC · kitchenette · εξωτερικοί Φ100 σε κούτελο	ΑΠ-05 · Α-10-S · Α-30-ΒΒ · τοιχοποιίες σοφίτας R04	**ΑΠ-08** **Κλίμακα 1:20 · Α3** 10/11/2026 · R17

ΚΑΤΑΚΟΡΥΦΟ ΔΙΑΓΡΑΜΜΑ ΑΠΟΧΕΤΕΥΣΗΣ & ΟΜΒΡΙΩΝ

Χωρίς κλίμακα

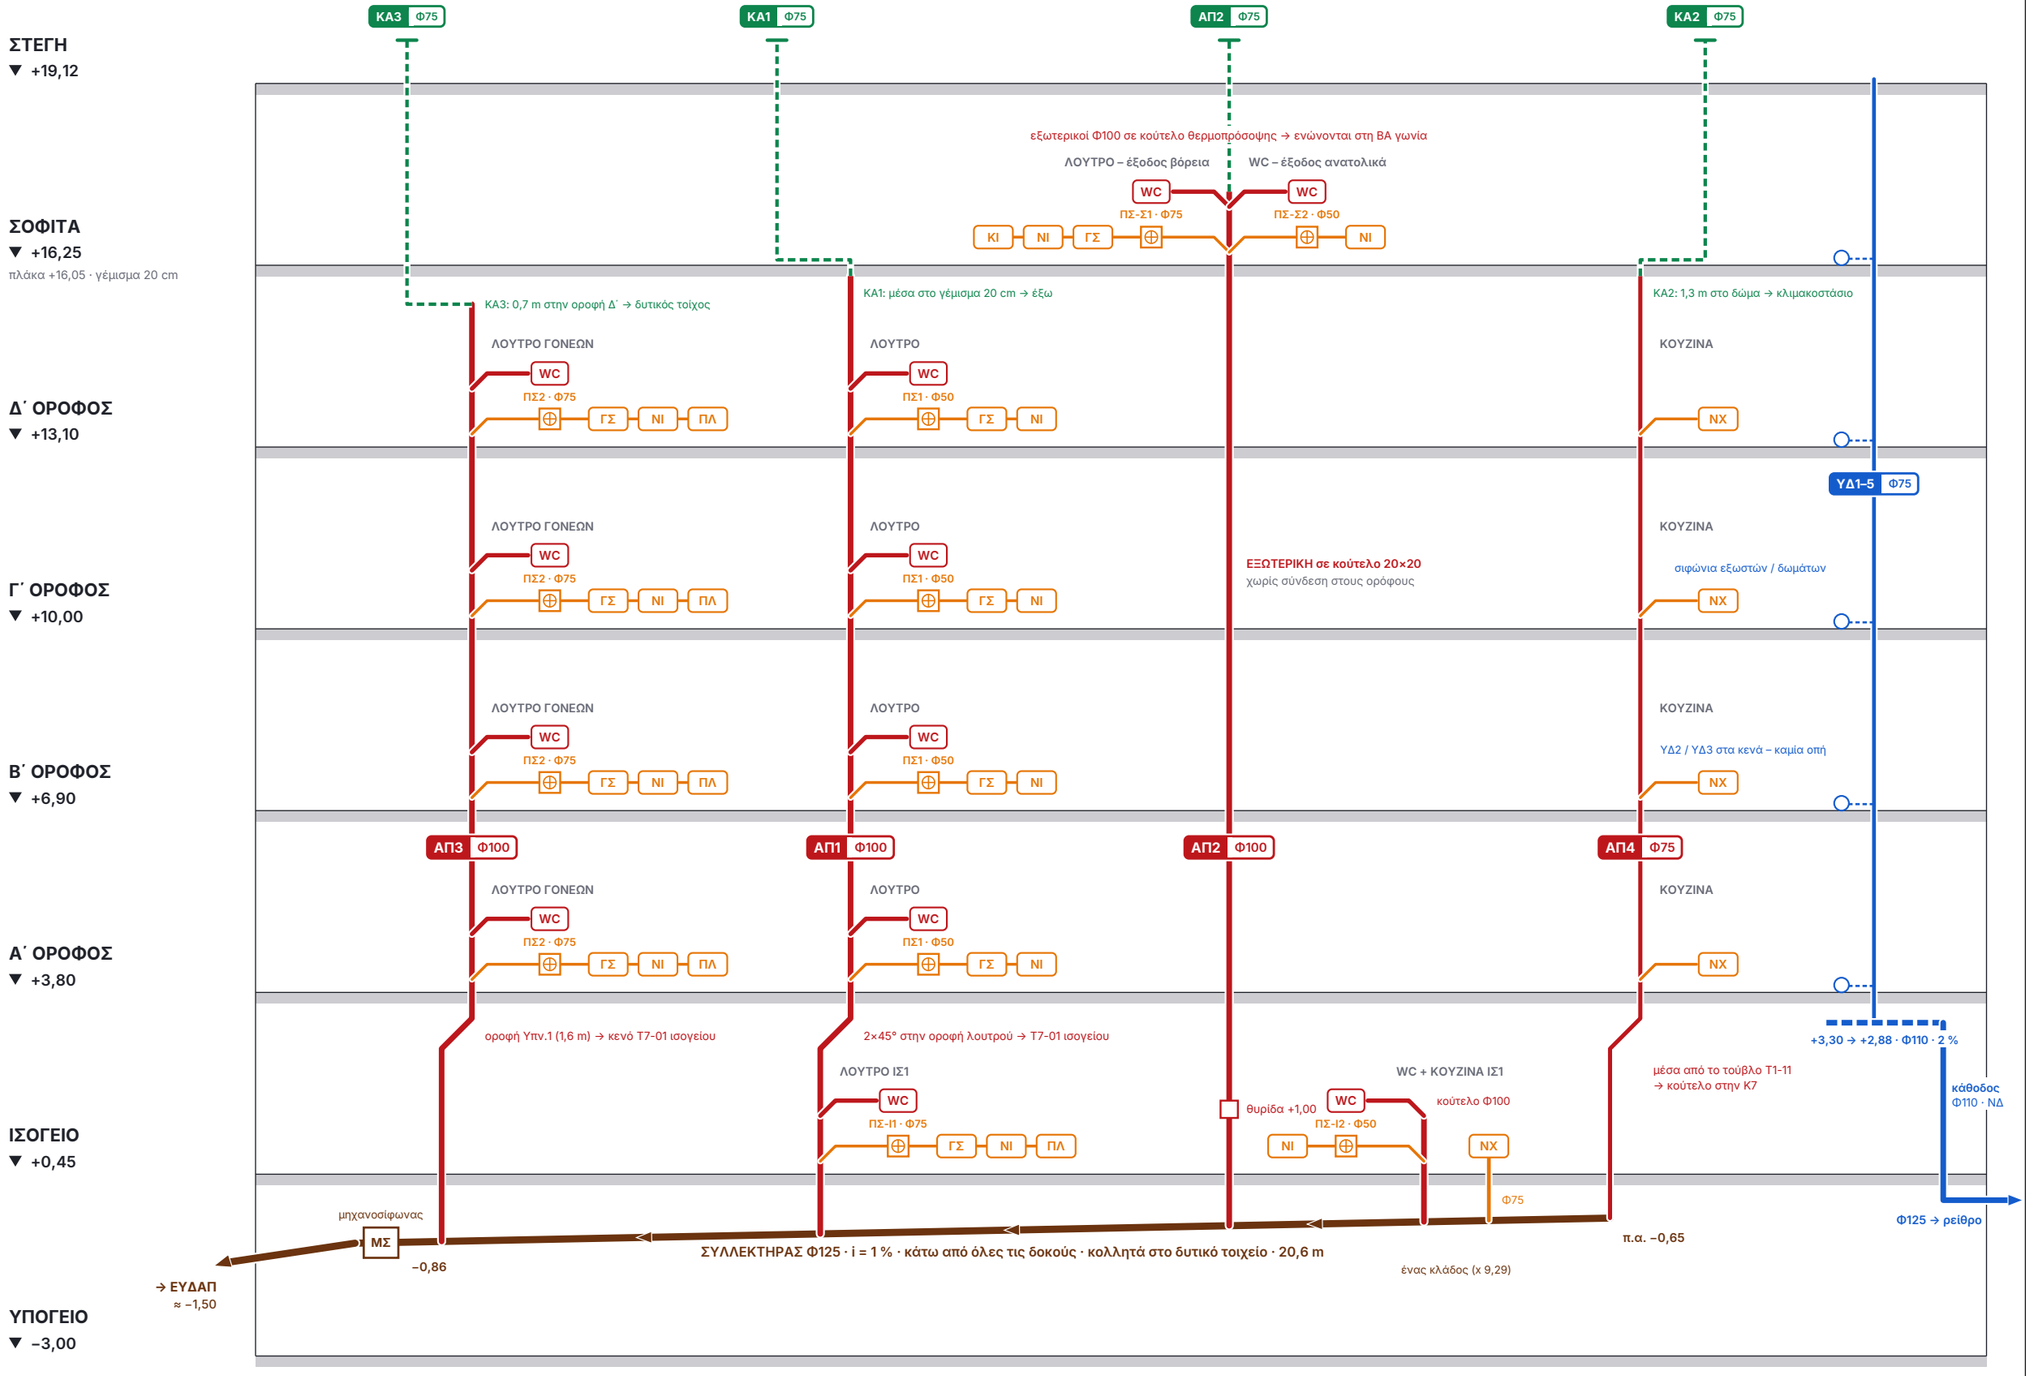

ΥΠΟΜΝΗΜΑ

- Λύματα: λεκάνη Φ90 · στήλη / αγωγός Φ100
- Ακάθαρτα: Φ40 νιπτήρας · Φ50 ντους, νεροχύτης, πλυντήριο · Φ75 έξοδος πατοσίφωνου
- Αερισμός ΚΑ Φ75 (βγαίνει έξω και ανεβαίνει στη θερμοπρόσοψη)
- Όμβρια: συλλεκτήρας / αγωγός
- Συλλεκτήρας ομβρίων ΨΗΛΑ +3,30 (οροφή προβόλων Α΄)
- Συλλεκτήρας / κλάδοι υπογείου, κρεμαστοί κάτω από τις δοκούς
- Πατοσίφωνο ΠΣ (σιφώνι δαπέδου με σχάρα)

ΣΥΝΤΟΜΟΓΡΑΦΙΕΣ

- **WC** λεκάνη κρεμαστή – Φ90 μέσα στον τοίχο λεκάνης
- **ΓΣ** γραμμικό σιφώνι ντους – Φ50 → πατοσίφωνο
- **ΝΙ** νιπτήρας – Φ40 → πατοσίφωνο
- **ΠΛ** πλυντήριο ρούχων – Φ50 → πατοσίφωνο
- **ΚΙ** kitchenette σοφίτας – Φ50 → πατοσίφωνο ΠΣ-Σ1
- **ΝΧ** νεροχύτης κουζίνας (+ πλυντήριο πιάτων) – Φ50
- **ΠΣ** πατοσίφωνο · δίπλα η διατομή εξόδου
- **ΚΑ** αερισμός στήλης Φ75 ως πάνω από τη στέγη

ΣΗΜΕΙΩΣΕΙΣ

- Στάθμες τελικού δαπέδου. Σοφίτα: πλάκα +16,05, γέμισμα 20 cm (Α-10-S, Α-30-ΒΒ).
- ΑΠ1 / ΑΠ3 Φ100 ηχομονωτικές, στο κενό 12 cm των τοίχων λεκάνης Τ7 · ΑΠ2 Φ100 εξωτερική σε κούτελο · ΑΠ4 Φ75 κολλητά στην Κ7.
- Ισόγειο: ΑΠ1 / ΑΠ3 με μετατόπιση στην οροφή → κενό του Τ7-01 ισογείου · ΑΠ4 μέσα από το τούβλο Τ1-11 στο κούτελο · WC και κουζίνα ΙΣ1 με δικές τους πτώσεις.
- Όμβρια: συλλεκτήρας ψηλά +3,30 με 2 % σε δύο κλάδους → κεντρική κάθοδος Φ110 στη ΝΔ γωνία (τοιχείο Κ9). ΥΔ2 / ΥΔ3 στα κενά των πλακών.
- Όλοι οι αερισμοί βγαίνουν έξω και καταλήγουν πάνω από τη στέγη – κανένας σε οροφή χώρου.
- Συλλεκτήρας υπογείου κάτω από όλες τις δοκούς – καμία οπή σε δοκό.

B

ΕΡΓΟ

ΠΕΝΤΑΟΡΟΦΟ ΚΤΗΡΙΟ ΚΑΤΟΙΚΙΩΝ – ΑΡΓΥΡΟΥΠΟΛΗ
Κωνσταντινουπόλεως 12 & Αγ. Βαρβάρας · Ο.Τ. 103-15
Εργοδότης: INTERKAT Α.Ε. · Κατασκευή: ARKAD Ι.Κ.Ε.

ΘΕΜΑ ΣΧΕΔΙΟΥ

ΚΑΤΑΚΟΡΥΦΟ ΔΙΑΓΡΑΜΜΑ
R17 · λύματα · ακάθαρτα · αερισμοί · όμβρια · οπές πλακών
Στήλες ΑΠ1–ΑΠ4 · αερισμοί · συλλεκτήρας · όμβρια

ΒΑΣΗ


ΑΠ-01 … ΑΠ-05

ΑΡ. ΣΧΕΔΙΟΥ


ΑΠ-09
Χωρίς κλίμακα · Α3
10/11/2026 · R17

ΟΠΕΣ – ΑΝΑΜΟΝΕΣ ΣΤΙΣ ΠΛΑΚΕΣ


Κλίμακα 1:105

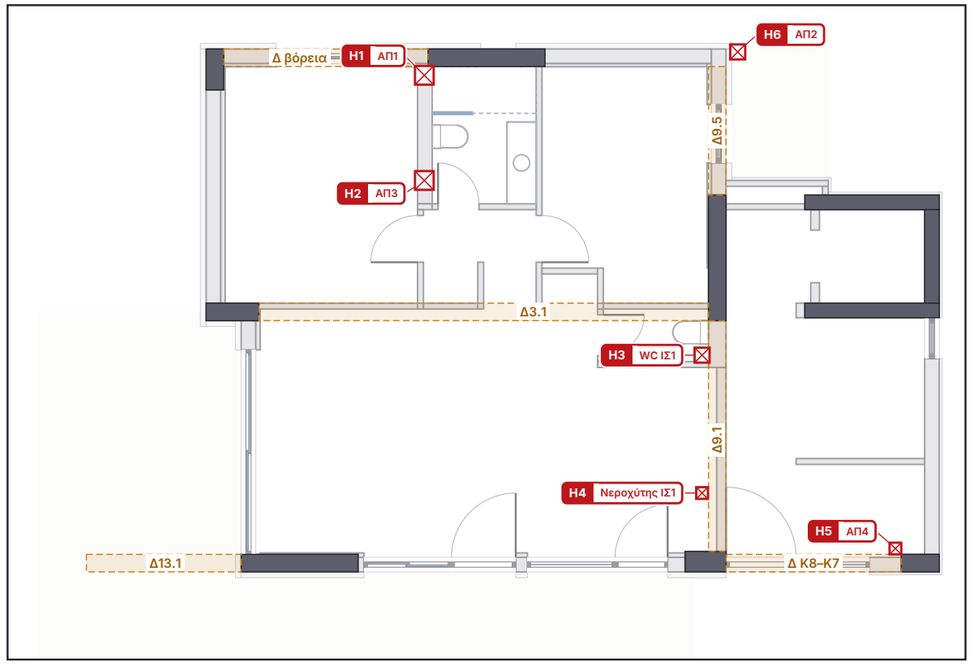

1 **Σ2 – ΠΛΑΚΑ ΟΡΟΦΗΣ ΥΠΟΓΕΙΟΥ (+0,30)** Κλίμακα 1:105

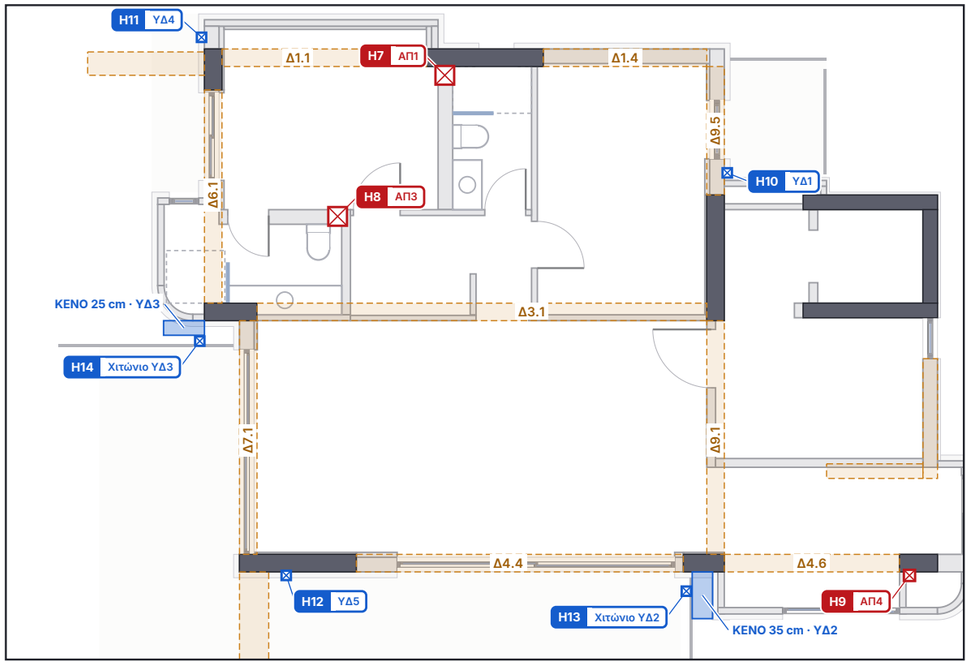

2 **Σ3 · Σ4 · Σ5 · Σ6 – ΟΡΟΦΗ ΙΣΟΓΕΙΟΥ, Α΄, Β΄, Γ΄** Κλίμακα 1:105

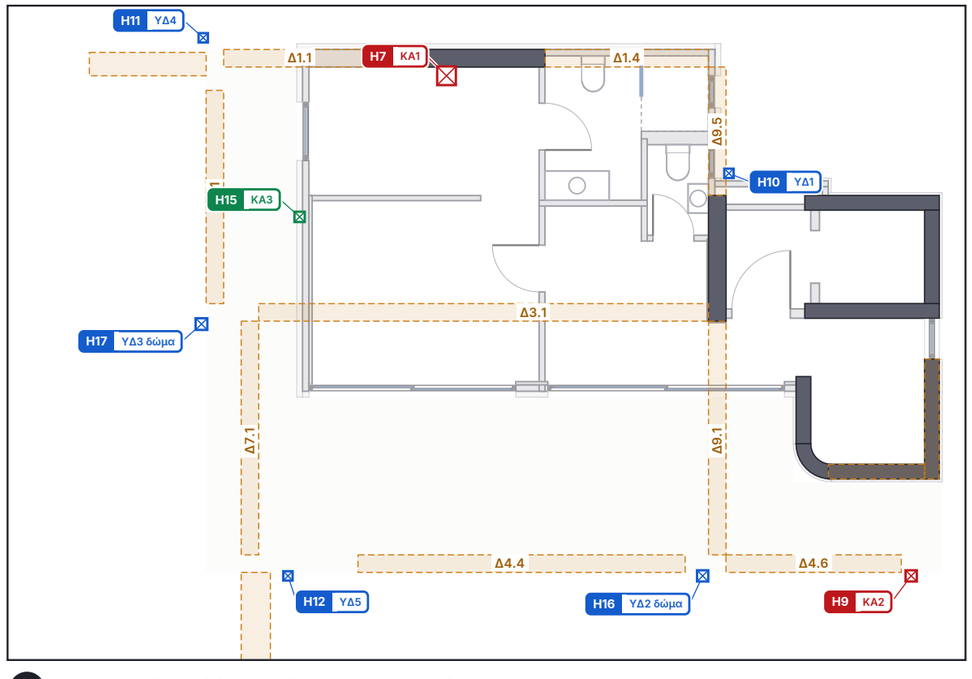

3 **Σ7 – ΟΡΟΦΗ Δ΄ (+16,05) · ΔΑΠΕΔΟ ΣΟΦΙΤΑΣ / ΔΩΜΑ** Κλίμακα 1:105

ΠΩΣ ΚΡΑΤΙΟΥΝΤΑΙ ΟΙ ΟΠΕΣ

- Η θέση κάθε οπής μετριέται ΑΠΟ ΠΑΡΕΙΕΣ ΣΚΥΡΟΔΕΜΑΤΟΣ (υποστυλώματα / δοκοί) – πίνακας ΑΠ-11. Οι τοίχοι χτίζονται μετά.
- Στήλες λουτρών ΑΠ1 / ΑΠ3: κουτί φελιζόλ 20×20 με κέντρο τον άξονα του ΚΕΝΟΥ 12 cm του τοίχου λεκάνης. Ανοχή ±2 cm.
- ΥΔ1 / ΥΔ4 / ΥΔ5: κουτί 10×10 κολλητά στην παρειά της δοκού ή του τοιχείου, ΜΕΣΑ ΣΤΗΝ ΠΛΑΚΑ του εξώστη – ποτέ μέσα στη δοκό.
- ΥΔ2 και ΥΔ3: ΚΑΜΙΑ οπή στους εξώστες (Σ3–Σ6) – κατεβαίνουν στα υπάρχοντα κενά ανάμεσα στις πλάκες. Μόνο χιτώνιο Ø63 στη βάση του στηθαίου για το σιφώνι.
- ΚΑΜΙΑ οπή σε δοκό ή Ε.Ζ. Πρόσθετος οπλισμός γύρω από κάθε οπή κατά τον στατικό – ο πίνακας να σταλεί στον κ. Κόγια πριν από τη σκυροδέτηση.

Σ8 – ΣΤΕΓΗ (προκαταρκτικά)

- ΚΑ1 Φ75: 4,45 / 0,45 στον πρόβολο Π2, κολλητά στη Β παρειά της Δ1.2 · ΚΑ3 Φ75: 2,40 / 3,365 στην πλάκα δυτικά του τοίχου της σοφίτας.
- ΚΑ2, απόληξη ΑΠ2 και υδρορροή στέγης ΥΔ1: οριστικοποιούνται με το σχέδιο στέγης (ανεστραμμένες δοκοί Σ8) – πριν από τον ξυλότυπο της στέγης.

ΥΠΟΜΝΗΜΑ

Δοκός (ξυλότυποι Σ2–Σ7) – ΚΑΜΙΑ οπή

ΟΠΕΣ ΑΝΑ ΠΛΑΚΑ

- **Σ2:** Η1 ΑΠ1 · Η2 ΑΠ3 · Η3 WC · Η4 νεροχύτης · Η5 ΑΠ4 · Η6 ΑΠ2 + χιτώνιο εξόδου στο νότιο τοιχείο (ΑΠ-01).
- **Σ3–Σ6:** Η7 ΑΠ1 · Η8 ΑΠ3 · Η9 ΑΠ4 · Η10 ΥΔ1 · Η11 ΥΔ4 · Η12 ΥΔ5 · χιτώνια στηθαίων Η13, Η14.
- **Σ7:** Η7 (ΚΑ1) · Η9 (ΚΑ2) · Η10–Η12 · Η15 ΚΑ3 · Η16, Η17 σιφώνια δώματος ΥΔ2 / ΥΔ3.
- **Σύμβολο:** τετράγωνο με Χ = οπή. Κόκκινο λύματα · πράσινο αερισμός · μπλε όμβρια. Οι διαστάσεις στο ΑΠ-11.

ΕΛΕΓΧΟΣ ΣΤΟΥΣ ΞΥΛΟΤΥΠΟΥΣ

- Οι θέσεις ελέγχθηκαν πάνω στους Σ2_ΕΦ … Σ7_ΕΦ (βαθμονόμηση στα υποστυλώματα): καμία οπή δεν πέφτει σε δοκό, υποστύλωμα ή Ε.Ζ.
- Το κενό 35 cm (ΥΔ2) και το κενό 25 cm (ΥΔ3) υπάρχουν στους Σ3, Σ4, Σ5, Σ6. Στο Σ7 η πλάκα του δώματος είναι ενιαία – εκεί μπαίνει το σιφώνι δώματος.

B

ΕΡΓΟ	ΘΕΜΑ ΣΧΕΔΙΟΥ	ΒΑΣΗ	ΑΡ. ΣΧΕΔΙΟΥ
ΠΕΝΤΑΟΡΟΦΟ ΚΤΗΡΙΟ ΚΑΤΟΙΚΙΩΝ – ΑΡΓΥΡΟΥΠΟΛΗ Κωνσταντινουπόλεως 12 & Αγ. Βαρβάρας · Ο.Τ. 103-15 Εργοδότης: INTERKAT Α.Ε. · Κατασκευή: ARKAD Ι.Κ.Ε.	**ΟΠΕΣ ΠΛΑΚΩΝ – ΚΑΤΟΨΕΙΣ** R17 · λύματα · ακάθαρτα · αερισμοί · όμβρια · οπές πλακών Σ2 · Σ3–Σ6 · Σ7 · θέσεις οπών και αναμονών	Σ2_ΕΦ … Σ7_ΕΦ · Σ8 · τοιχοποιίες R05 / R13 / R25 / R04	**ΑΠ-10** **Κλίμακα 1:105 · A3** 10/11/2026 · R17

ΠΙΝΑΚΑΣ ΟΠΩΝ ΚΑΙ ΑΝΑΜΟΝΩΝ – θέσεις από παρειές σκυροδέματος (x ανατολικά, y νότια, m μοντέλου)

No	Πλάκα	Αγωγός	x / y	Θέση από σκυρόδεμα	Οπή	Παρατήρηση
Η1	Σ2	ΑΠ1 · Φ100	4,535 / 0,95	6,5 cm δυτικά της Δ παρειάς Κ2 · 15 cm νότια της Ν παρειάς Κ2	κουτί 20×20	στο κενό του Τ7-01 ισογείου
Η2	Σ2	ΑΠ3 · Φ100	4,535 / 2,75	6,5 cm δυτικά της Δ παρειάς Κ2 · 1,95 m νότια της Ν παρειάς Κ2	κουτί 20×20	ίδιο κενό, νότια της λεκάνης
Η3	Σ2	WC ΙΣ1 · Φ100	9,29 / 5,74	άξονας 11 cm δυτικά της Δ παρειάς της δοκού Δ9.1 · 59 cm νότια της Ν παρειάς Κ3	Ø160	κούτελο δίπλα στη λεκάνη
Η4	Σ2	Νεροχύτης ΙΣ1 · Φ75	9,29 / 8,10	άξονας 11 cm δυτικά της Δ παρειάς της Δ9.1 · 2,95 m νότια της Ν παρειάς Κ3	Ø125	μέσα στο ερμάριο του νεροχύτη
Η5	Σ2	ΑΠ4 · Φ75	12,60 / 9,05	άξονας 10 cm δυτικά της Δ παρειάς Κ7 · 10 cm βόρεια της Β παρειάς Κ7	Ø125	κούτελο lobby → μηχανοστάσιο
Η6	Σ2	ΑΠ2 · Φ100	9,90 / 0,55	άξονας 20 cm ανατολικά της Α παρειάς της Δ9.5 (x 9,70) · 5 cm νότια της βόρειας γραμμής Κ2 (y 0,50)	Ø160 + στεγανό κολάρο	εξωτερικά, κάτω από τη βεράντα – στεγάνωση
Η7	Σ3–Σ7	ΑΠ1 (Σ7: ΚΑ1 Φ75) · Φ100	4,915 / 0,95	άξονας 31,5 cm ανατολικά της Δ παρειάς Κ2 · 15 cm νότια της Ν παρειάς Κ2	κουτί 20×20	άξονας κενού Τ7-01 (4,855–4,975)
Η8	Σ3–Σ6	ΑΠ3 · Φ100	3,08 / 3,365	άξονας 1,52 m δυτικά της Δ παρειάς Κ2 · 2,565 m νότια της Ν παρειάς Κ2 (= 1,485 m βόρεια της Β παρειάς της Δ3.1)	κουτί 20×20	άξονας κενού Τ7-02 (3,305–3,425)
Η9	Σ3–Σ7	ΑΠ4 (Σ7: ΚΑ2) · Φ75	12,87 / 9,51	κολλητά στη Ν παρειά Κ7 (άξονας 6 cm) · 17 cm ανατολικά της Δ παρειάς Κ7	κουτί 12×12	η «προβλεπόμενη οπή δίπλα στην κολόνα»
Η10	Σ3–Σ7	ΥΔ1 · Φ75	9,75 / 2,62	κολλητά στην Α παρειά της Δ9.5 (άξονας 5 cm) · 38 cm βόρεια της Β παρειάς Κ3	κουτί 10×10	πλάκα ΒΑ εξώστη Π4
Η11	Σ3–Σ7	ΥΔ4 · Φ75	0,75 / 0,30	άξονας 5 cm δυτικά της Δ παρειάς Κ1 · 20 cm βόρεια της Β παρειάς Κ1	κουτί 10×10	πλάκα ΒΔ εξώστη – 20 cm από την Ε.Ζ. 40/30
Η12	Σ3–Σ7	ΥΔ5 · Φ75	2,20 / 9,51	κολλητά στη Ν παρειά Κ9 (άξονας 6 cm) · 80 cm ανατολικά της Δ παρειάς Κ9	κουτί 10×10	πλάκα νότιου εξώστη Π12 – 30 cm από την Ε.Ζ. 50/30
Η13	Σ3–Σ6	Χιτώνιο στηθαίου (ΥΔ2) · Φ50	9,05 / 9,78	στη ΒΑΣΗ του στηθαίου 8,95–9,15 · 33 cm νότια της Ν παρειάς Κ8	χιτώνιο Ø63	πλευρική έξοδος σιφωνιού εξώστη – όχι στην πλάκα
Η14	Σ3–Σ6	Χιτώνιο στηθαίου (ΥΔ3) · Φ50	0,72 / 5,50	στη ΒΑΣΗ του στηθαίου 5,40–5,60 · 8 cm δυτικά της Δ παρειάς Κ10	χιτώνιο Ø63	πλευρική έξοδος σιφωνιού εξώστη – όχι στην πλάκα
Η15	Σ7	ΚΑ3 · Φ75	2,40 / 3,365	άξονας 2,20 m δυτικά της Δ παρειάς Κ2 · 2,565 m νότια της Ν παρειάς Κ2	Ø110	έξω από τον δυτικό τοίχο της σοφίτας
Η16	Σ7	ΥΔ2 – σιφώνι δώματος · Φ75	9,30 / 9,51	κολλητά στη Ν παρειά της Δ4.6 / Κ8 (άξονας 6 cm) · 30 cm ανατολικά της Δ παρειάς Κ8 (x 9,00)	κουτί 12×12	πάνω ακριβώς από το κενό 35 cm
Η17	Σ7	ΥΔ3 – σιφώνι δώματος · Φ75	0,72 / 5,20	άξονας 8 cm δυτικά της Δ παρειάς Κ10 · 5 cm νότια της Ν παρειάς Κ10	Ø125	πάνω ακριβώς από το κενό 25 cm
–	Τοιχείο	Έξοδος συλλεκτήρα · Φ125	−0,75 / 15,30	νότιο τοιχείο υπογείου · άξονας 50 cm ανατολικά της εσωτερικής παρειάς του δυτικού τοιχείου · π.α. −0,86	χιτώνιο Ø200	έξω από το γωνιακό υποστύλωμα (ως x −0,965)
–	Σ3–Σ6	ΥΔ2 και ΥΔ3 · Φ75	9,30 / 9,51 · 0,72 / 5,20	στα ΚΕΝΑ ανάμεσα στις πλάκες: 35 cm νότια της Κ8 · 25 cm δυτικά της Κ10	ΚΑΜΙΑ ΟΠΗ	«να μην τρυπάμε μπαλκόνι»

Πλάκες: Σ2 οροφή υπογείου +0,30 · Σ3 οροφή ισογείου +3,65 · Σ4 οροφή Α΄ +6,75 · Σ5 οροφή Β΄ +9,85 · Σ6 οροφή Γ΄ +12,95 · Σ7 οροφή Δ΄ +16,05 (δάπεδο σοφίτας / δώμα) · Σ8 στέγη.
Κ2 200/30: x 4,60–6,60 · y 0,50–0,80 · Κ3 30/215: x 9,40–9,70 · y 3,00–5,15 · Κ7 65/30: x 12,70–13,35 · y 9,15–9,45 · Κ8 70/30: x 9,00–9,70 · Κ9 200/30: x 1,40–3,40 · Κ10 90/30: x 0,80–1,70 · y 4,85–5,15 · Κ1 30/70: x 0,80–1,10 · y 0,50–1,20.

ΑΛΛΑΓΕΣ R16 → R17 (απαντήσεις Γιάννη 10/11/2026 στα ανοικτά του R16)

Θέμα	Απάντηση	R17	Έλεγχος / συνέπεια
1 · ΑΠ3 στο ισόγειο	«στην οροφή»	μετατόπιση 1,6 m στην οροφή του Υπν.1 → κατεβαίνει στο ΚΕΝΟ του Τ7-01 ισογείου (4,535 / 2,75)	R16: κατέβαινε μέσα στη ντουλάπα – όχι σε κενό τοίχου. Βάση υπογείου και οπή Σ2 αλλάζουν θέση
3 · Πατοσίφωνο ντους γονέων	«όχι δίπλα στο γυαλί»	το ΠΣ2 μένει δίπλα στη λεκάνη (2,45 / 3,80) · γραμμικό → ΠΣ2 2,4 m	πτώση 2 % + διάμετρος = 9,8 cm σε ωφέλιμο 12 – χωράει
4 · Όμβρια ψηλά	«κλίση 2 %»	2 % σε δύο κλάδους από +3,30 → κεντρική κάθοδος στη ΝΔ γωνία (τοιχείο Κ9): βόρειος 21,1 m → +2,88, νότιος 8,5 m → +3,13	με την κάθοδο στην είσοδο (R16) τα 30 m × 2 % = 0,60 m έφερναν τον αγωγό 20 cm ΚΑΤΩ από τα πρέκια της νότιας όψης → η κάθοδος μετακινήθηκε (ανοικτό 12)
5 · Συλλεκτήρας υπογείου	«ναι, κολλητά»	ο νότιος κλάδος κολλητά στο δυτικό τοιχείο (άξονας x −1,10) · έξοδος στο νότιο τοιχείο x −0,75, π.α. −0,86	20,6 m · οι Θ.Σ.Υ. 3 / 4 ελεύθερες · έξοδος έξω από το γωνιακό υποστύλωμα
6 · Ηχομόνωση	«ναι»	ΑΠ1 / ΑΠ3 και οι μετατοπίσεις τους: ηχομονωτικός σωλήνας PP τριών στρώσεων	εξωτ. διάμετρος 110 – χωράει στο κενό 12 cm
7 · Υδρορροές	«Φ75 μέσα στη θερμοπρόσοψη»	ΥΔ1–ΥΔ5 Φ75 μέσα στη θερμοπρόσοψη 10 cm	μένουν 2,5 cm μόνωσης πίσω από τον σωλήνα
8 · ΑΠ4	«Φ75»	Φ75, θέση οριστική	–
ΥΔ2 · ΥΔ3	«από το κενό που υπάρχει, να μην τρυπάμε μπαλκόνι»	ΥΔ2 → 9,30 / 9,51 στο κενό 35 cm νότια της Κ8 · ΥΔ3 → 0,72 / 5,20 στο κενό 25 cm δυτικά της Κ10	τα κενά υπάρχουν στους Σ3–Σ6 · καμία οπή σε εξώστη · χιτώνιο Ø63 στη βάση του στηθαίου
Στήλες λουτρών	«η κάθετη στήλη στο κενό του τοίχου»	ΑΠ1 4,915 / 0,95 · ΑΠ3 3,08 / 3,365 · ισόγειο 4,535 / 0,95 και 4,535 / 2,75 – στον άξονα του κενού 12 cm	R16: ΑΠ1 4,925 / 0,92 · ΑΠ3 3,08 / 3,38
ΑΠ2 εξωτερική	(έλεγχος)	9,90 / 0,55 σε κατακόρυφο κούτελο 20×20 έξω από τη θερμοπρόσοψη	R16: 9,755 / 0,58 – Φ110 δεν χωρά σε θερμοπρόσοψη 10 cm και εφαπτόταν στη Δ9.5
Οπές πλακών	«πες μου πού να κρατήσω τρύπες»	νέα φύλλα ΑΠ-10 (κατόψεις) και ΑΠ-11 (πίνακας από παρειές σκυροδέματος)	ελεγμένες στους Σ2_ΕΦ … Σ7_ΕΦ

ΕΛΕΓΧΟΣ ΔΙΑΣΤΑΣΕΩΝ (apox_check.py) – 93 έλεγχοι: 74 εντάξει · 19 οριακά · 0 λάθη

Ομάδα	Αποτέλεσμα	Τι ελέγχθηκε
Στήλες στο κενό	4 / 6 εντάξει	Όροφοι ΑΠ1 στον Τ7-01: περιθώριο 0,5 cm εκατέρωθεν · 9,5 cm από το άκρο του τοίχου · 74,5 cm από το πλαίσιο της λεκάνης · Όροφοι ΑΠ3 στον Τ7-02: περιθώριο 0,5 cm εκατέρωθεν · 1,4 cm από το άκρο του τοίχου · 2,5 cm από το πλαίσιο της λεκάνης · Ισόγειο ΑΠ1 στον Τ7-01: περιθώριο 0,5 cm εκατέρωθεν · 9,5 cm από το άκρο του τοίχου · 74,5 cm από το πλαίσιο της λεκάνης · Ισόγειο ΑΠ3 στον Τ7-01: περιθώριο 0,5 cm εκατέρωθεν · 34,5 cm από το άκρο του τοίχου · 44,5 cm από το πλαίσιο της λεκάνης
Γέμισμα / πατοσίφωνα	12 / 12 εντάξει	Ισόγειο: δυσμενέστερος αγωγός στο γέμισμα Φ50 1,80 m → πτώση 2 % + διάμετρος = 8,6 cm (ωφέλιμο 12,0 από γέμισμα 15,0) · Όροφοι: δυσμενέστερος αγωγός στο γέμισμα Φ50 2,21 m → πτώση 2 % + διάμετρος = 9,4 cm (ωφέλιμο 12,0 από γέμισμα 15,0) · Δ΄: δυσμενέστερος αγωγός στο γέμισμα Φ50 2,21 m → πτώση 2 % + διάμετρος = 9,4 cm (ωφέλιμο 12,0 από γέμισμα 15,0) · Σοφίτα: δυσμενέστερος αγωγός στο γέμισμα Φ50 2,80 m → πτώση 2 % + διάμετρος = 10,6 cm (ωφέλιμο 17,0 από γέμισμα 20,0)
Συνδέσεις / τοίχοι	15 / 15 εντάξει	κάθε αγωγός καταλήγει σε στήλη / πτώση / πατοσίφωνο · οι αγωγοί «σε τοίχο» βρίσκονται μέσα σε τοίχο του μοντέλου τοιχοποιών
Οπές πλακών	30 / 46 εντάξει · 16 κολλητά	απόσταση κάθε οπής από υποστυλώματα, δοκούς και Ε.Ζ. της ίδιας πλάκας. «Κολλητά» = στην παρειά δοκού / τοιχείου αλλά μέσα στην πλάκα (ΥΔ1, ΥΔ5, ΑΠ4, σιφώνια δώματος)
Υπόγειο	εντάξει	Κρεμαστοί αγωγοί: ελάχιστη απόσταση από υποστύλωμα / τοιχείο 3,7 cm · κανένας στη χαμηλή ζώνη · Συλλεκτήρας Φ125: 20,6 m × 1 % → κεφαλή −0,65, έξοδος −0,86 · καθαρό ύψος κάτω από τον αγωγό ≈ 2,07 m · Κάτω από δοκούς 30/50 (κάτω παρειά −0,20): άνω άντυγα συλλεκτήρα στην κεφαλή −0,525 → περιθώριο 32,5 cm
Όμβρια	οριακό	Βόρειος κλάδος: 21,1 m × 2 % → +3,30 → 2,88 (κάτω άντυγα στο τέλος 2,823) · Βόρειος κλάδος μπροστά από κουφώματα ισογείου: χαμηλότερη κάτω άντυγα 2,823 στο 1,21 / 9,30 → 2,7 cm ΚΑΤΩ από το πρέκι +2,85 · Νότιος κλάδος: 8,5 m × 2 % → +3,30 → 3,13 (κάτω άντυγα στο τέλος 3,076) · Νότιος κλάδος μπροστά από κουφώματα ισογείου: χαμηλότερη κάτω άντυγα 3,076 στο 1,21 / 9,30 → 22,6 cm πάνω από το πρέκι +2,85
Υδρορροές	7 / 7 εντάξει	ΥΔ1–ΥΔ5 μέσα στα πολύγωνα θερμοπρόσοψης του μοντέλου · ΥΔ2 / ΥΔ3 ολόκληρες μέσα στα κενά των πλακών

Παραδοχές: Τ7 = 2 γυψ. + CW 50 + κενό 12 + CW 30 + 2 γυψ. από την πλευρά του λουτρού · Φ100 → Ø110 · γέμισμα 15 cm (σοφίτα 20), ωφέλιμο −3 cm · πρέκια ισογείου +2,85 · συλλεκτήρας ομβρίων: άξονας +3,30 κάτω από τους προβόλους.

ΑΝΟΙΚΤΑ – απάντησε με τον αριθμό

No	Θέμα	Τι έγινε / τι προτείνεται	Ερώτηση
12	Κεντρική κάθοδος ομβρίων	Για να βγει το 2 % η κάθοδος Φ110 πήγε από τον πεσσό της εισόδου στη ΝΔ γωνία (κούτελο στο τοιχείο Κ9, βεράντα ΙΣ1) και ο θαμμένος Φ125 φεύγει από εκεί. Αν η κάθοδος πρέπει να μείνει στην είσοδο, η μέγιστη κλίση που χωράει πάνω από τα πρέκια είναι 1,3 %.	ΝΔ γωνία με 2 % ή είσοδος με 1,3 %;
13	Οπές στέγης Σ8	ΚΑ1 και ΚΑ3 περνούν την πλάκα της στέγης (πρόβολοι). ΚΑ2, απόληξη ΑΠ2 και υδρορροή στέγης θέλουν το σχέδιο της στέγης.	Να γίνει φύλλο στέγης πριν από τον ξυλότυπο Σ8;
14	Στατικός	Ο πίνακας ΑΠ-11 να εγκριθεί από τον κ. Κόγια (οπές δίπλα σε δοκούς / τοιχεία: Η9, Η10, Η12, Η16, Η17).	Να του σταλεί;

ΕΚΛΕΙΣΑΝ ΣΤΟ R17: 1 (ΑΠ3 στην οροφή) · 3 (ΠΣ2 μένει) · 4 (2 %) · 5 (κολλητά στο τοιχείο) · 6 (ηχομονωτικοί) · 7 (Φ75 στη θερμοπρόσοψη) · 8 (ΑΠ4 Φ75).

ΕΡΓΟ

ΠΕΝΤΑΟΡΟΦΟ ΚΤΗΡΙΟ ΚΑΤΟΙΚΙΩΝ – ΑΡΓΥΡΟΥΠΟΛΗ
Κωνσταντινουπόλεως 12 & Αγ. Βαρβάρας · Ο.Τ. 103-15
Εργοδότης: INTERKAT Α.Ε. · Κατασκευή: ARKAD Ι.Κ.Ε.

ΘΕΜΑ ΣΧΕΔΙΟΥ

ΑΛΛΑΓΕΣ R16 → R17 · ΕΛΕΓΧΟΣ ΔΙΑΣΤΑΣΕΩΝ
R17 · λύματα · ακάθαρτα · αερισμοί · όμβρια · οπές πλακών
Απαντήσεις Γιάννη 10/11/2026 · έλεγχος · ανοικτά

ΒΑΣΗ

Όλο το κτίριο · τοιχοποιίες ΥΠ R05 · ΙΣ R13 · Β1 R25 · Δ R04 · ΣΟΦ R04

ΑΡ. ΣΧΕΔΙΟΥ

ΑΠ-12
Χωρίς κλίμακα · Α3
10/11/2026 · R17