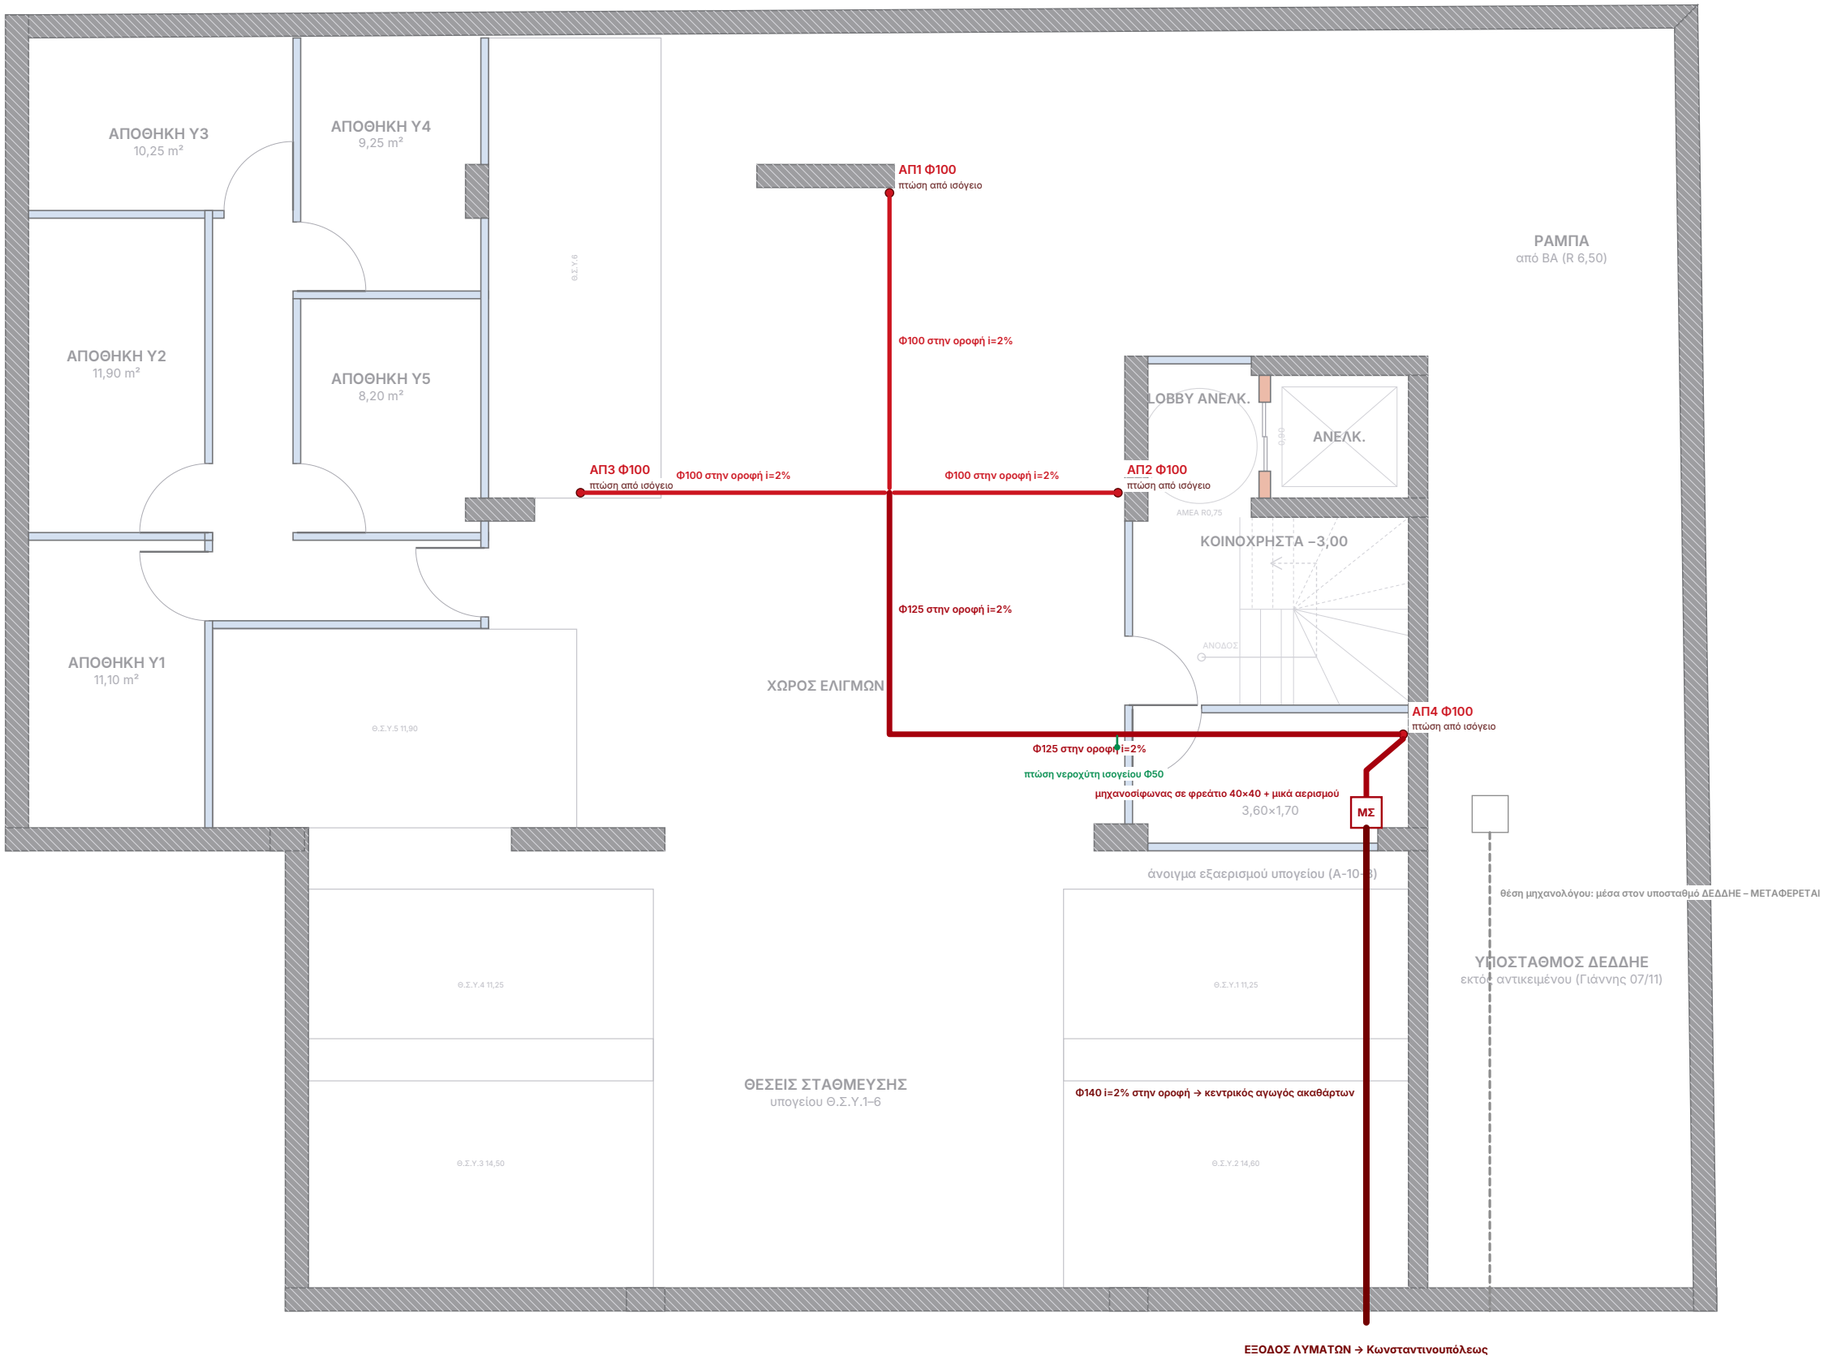


ΥΠΟΜΝΗΜΑ

- Στήλη λυμάτων ΑΠ Φ100 – U-PVC 6 atm, συνεχίζει ως αερισμός
- Θέση μηχανολόγου όπου μετακινήθηκε (διακεκομμένη)
- Λεκάνη → στήλη Φ100 (ή Φ90 όπου γράφεται)
- Σιφώνι δαπέδου → στήλη Φ70
- Ντους / πλυντήριο Φ50 · νιπτήρας Φ40 · νεροχύτης Φ50
- Σιφώνι δαπέδου (ΣΔ)
- Υδρορροή ΥΔ Φ75 – έξω από πλάκα / γέμισμα
- Σιφώνι ομβρίων εξώστη · διακεκ. = πλευρική έξοδος
- Δοκός (Σ4/Σ5) – καμία οπή
- Συλλεκτήριος Φ125 / έξοδος Φ140 στην οροφή υπογείου

ΣΗΜΕΙΩΣΕΙΣ ΥΠΟΓΕΙΟΥ

1. Όλοι οι συλλεκτήριοι κρέμονται στην οροφή (κατά μηχανολογική) – καμία όδευση στο δάπεδο του υπογείου.
2. Οι πτώσεις ΑΠ1–ΑΠ4 κατεβαίνουν στις ίδιες θέσεις με τους ορόφους· ΑΠ2/ΑΠ3 0,15 m βόρεια της γραμμής Δ3.1.
3. Μηχανοσίφωνας + έξοδος Φ140: η θέση του μηχανολόγου (x 14,16) είναι μέσα στον υποσταθμό ΔΕΔΔΗΕ → μεταφέρθηκαν στο μηχανοστάσιο (x 12,55), έξοδος νότια.
4. Πριν την παραγγελία: έλεγχος δοκών Σ2 στις διαδρομές, ελεύθερο ύψος κάτω από Φ125 (πτώση ~0,30 m συνολικά) και βάθος αγωγού ΕΥΔΑΠ στον δρόμο.
5. Νεροχύτης ισογείου: κατακόρυφη πτώση Φ50 στον Φ125 από κάτω (αντί για 3 m στο γέμισμα ως ΑΠ2).
6. Τα όμβρια ΔΕΝ μπαίνουν στο υπόγειο: βγαίνουν στο έδαφος του ισογείου προς το ρείθρο (βλ. ΑΠ-02).

ΕΡΓΟ

ΠΕΝΤΑΟΡΟΦΟ ΚΤΗΡΙΟ ΚΑΤΟΙΚΙΩΝ – ΑΡΓΥΡΟΥΠΟΛΗ
Κωνσταντινουπόλεως 12 & Αγ. Βαρβάρας · Ο.Τ. 103-15
Εργοδότης: INTERKAT Α.Ε. · Κατασκευή: ARKAD Ι.Κ.Ε.

ΘΕΜΑ ΣΧΕΔΙΟΥ


ΑΠΟΧΕΤΕΥΣΗ – ΥΠΟΓΕΙΟ
Αποχετεύσεις λυμάτων · υδρορροές · κατά μηχανολογική μελέτη αδείας
ΥΠΟΓΕΙΟ – συλλεκτήριοι στην οροφή, μηχανοσίφωνας, έξοδος

ΒΑΣΗ

Μηχ. μελέτη αδείας Α-02 (υπόγειο) · τοιχοποιίες υπογείου R05

ΑΡ. ΣΧΕΔΙΟΥ

ΑΠ-01
Κλίμακα 1:80 · Α3
09/11/2026 · R00

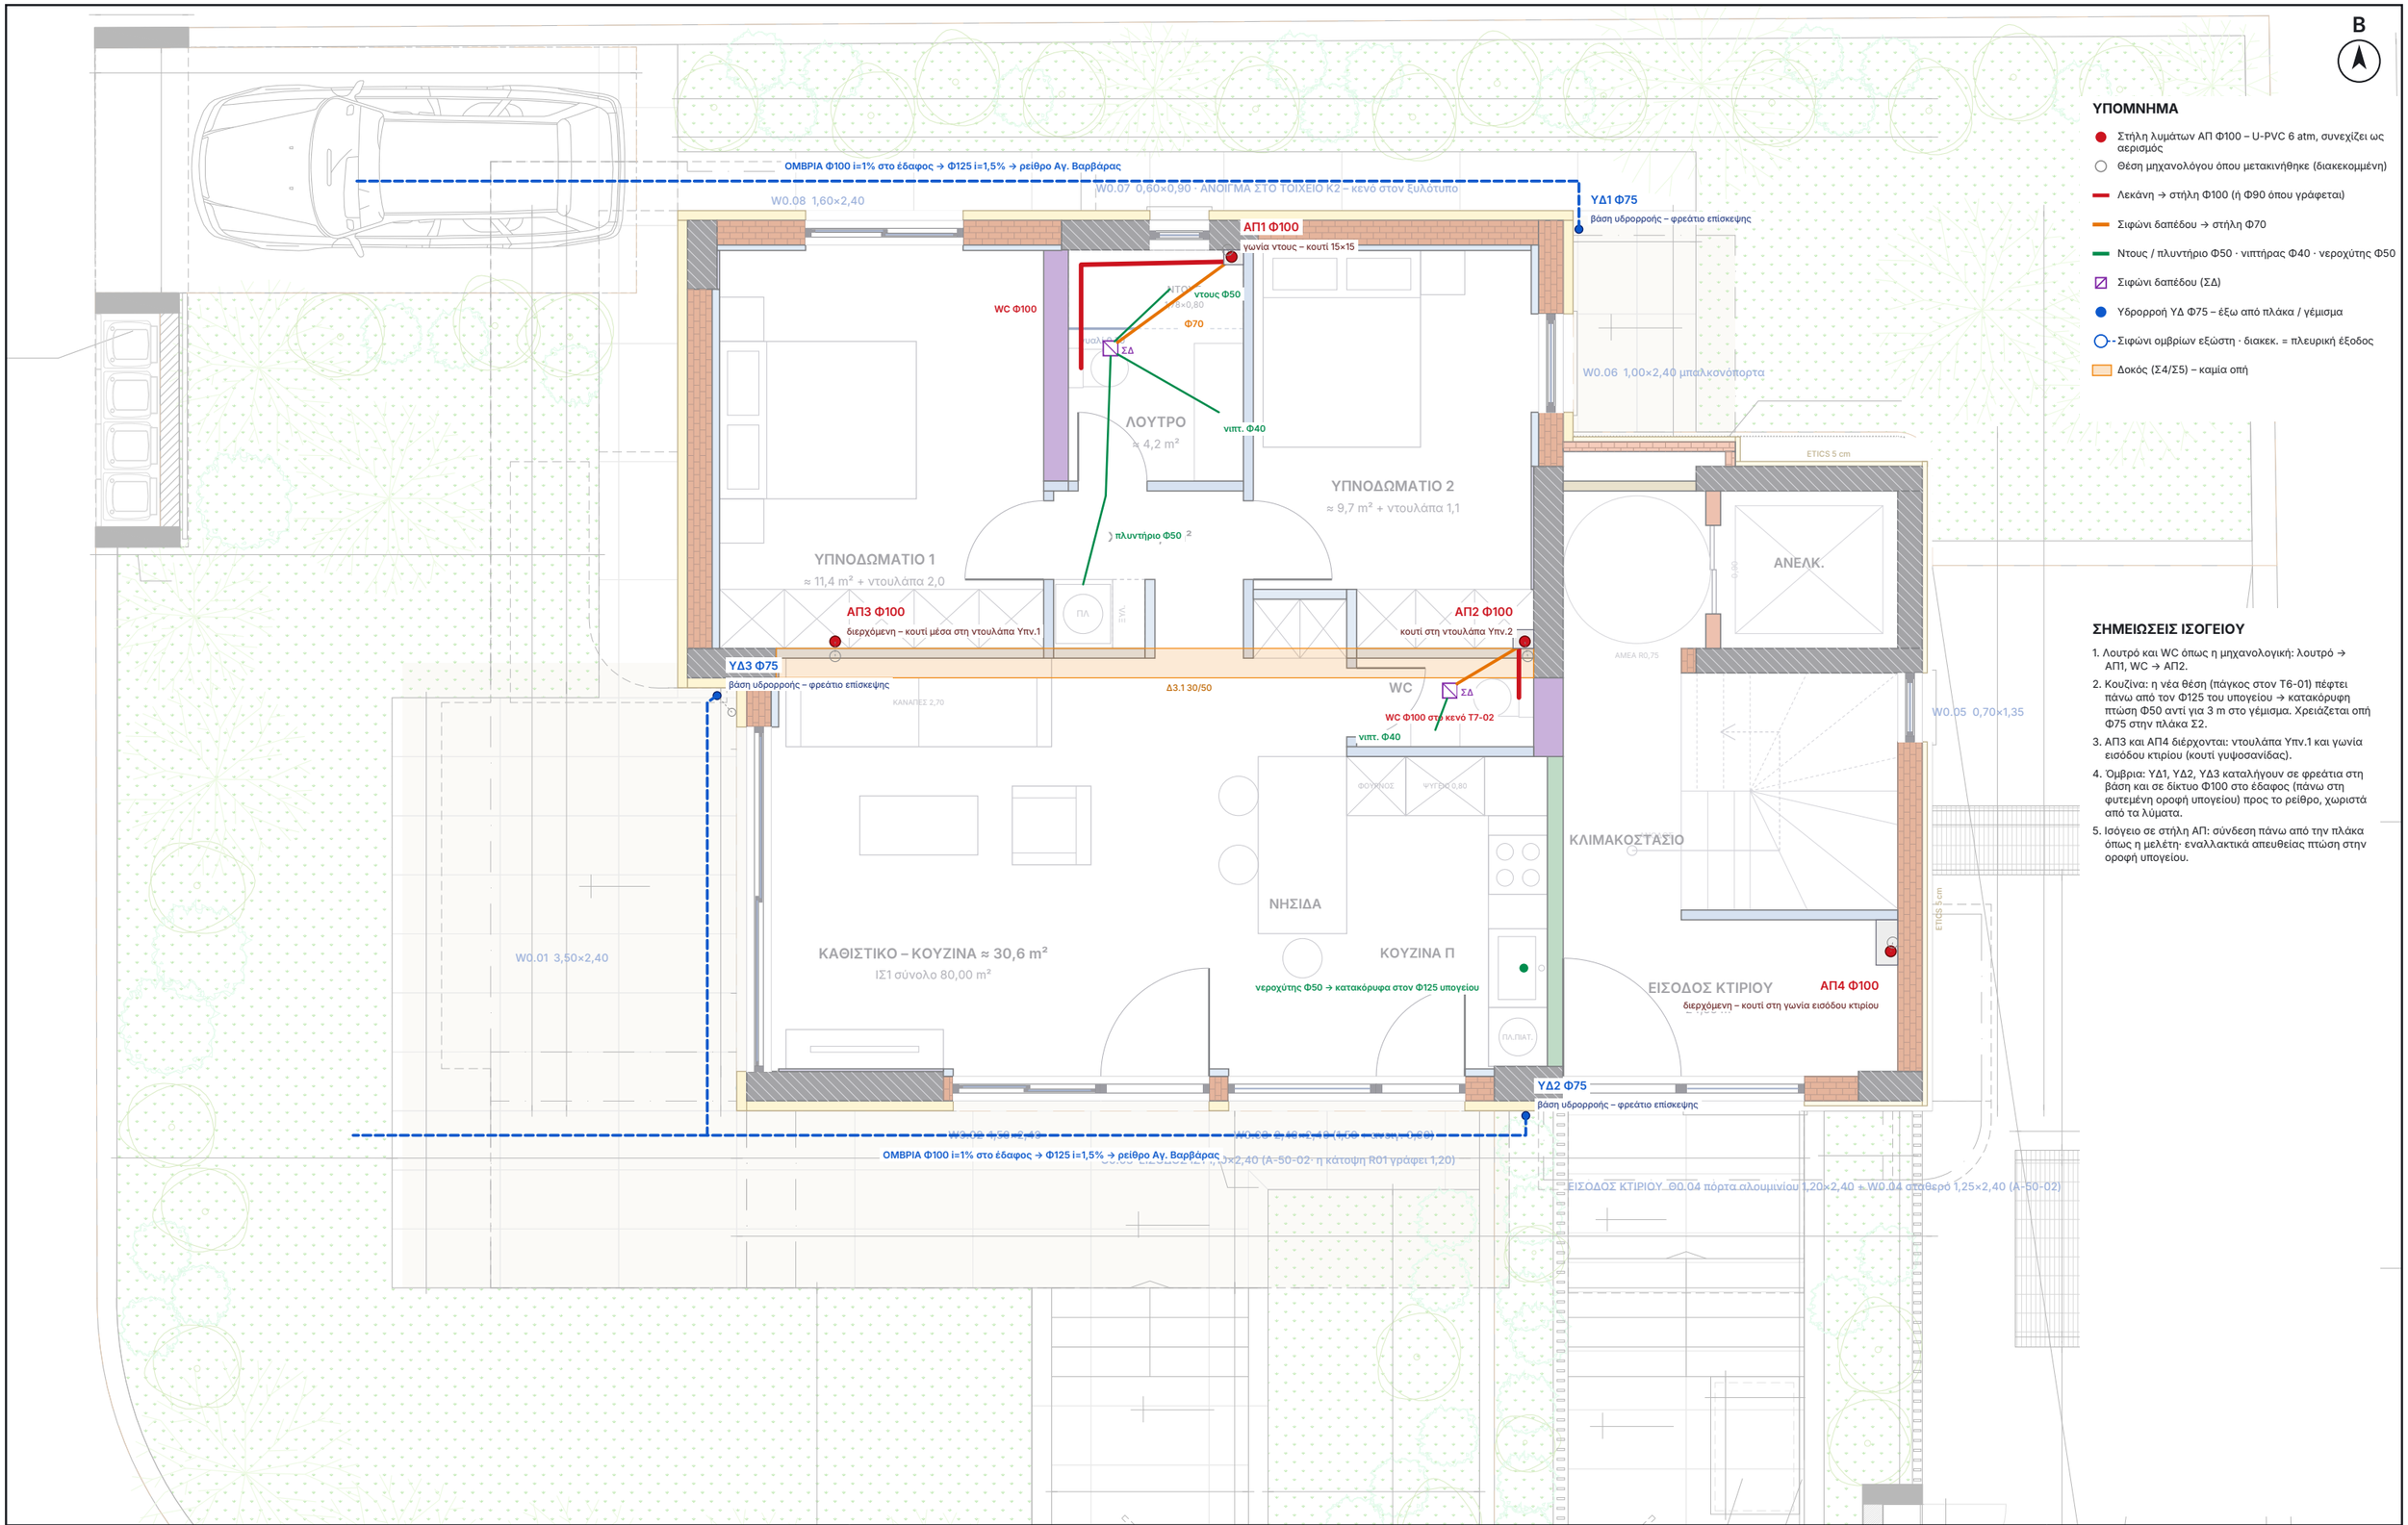

ΕΡΓΟ

ΠΕΝΤΑΟΡΟΦΟ ΚΤΗΡΙΟ ΚΑΤΟΙΚΙΩΝ – ΑΡΓΥΡΟΥΠΟΛΗ
Κωνσταντινουπόλεως 12 & Αγ. Βαρβάρας · Ο.Τ. 103-15
Εργοδότης: INTERKAT Α.Ε. · Κατασκευή: ARKAD Ι.Κ.Ε.

ΘΕΜΑ ΣΧΕΔΙΟΥ

ΑΠΟΧΕΤΕΥΣΗ – ΙΣΟΓΕΙΟ

Αποχετεύσεις λυμάτων · υδρορροές · κατά μηχανολογική μελέτη αδείας
ΙΣΟΓΕΙΟ – ΙΣ1, είσοδος κτιρίου, δίκτυο ομβρίων


ΒΑΣΗ

Μηχ. μελέτη αδείας Α-03 (ισόγειο) · τοιχοποιίες ισογείου R13

ΑΡ. ΣΧΕΔΙΟΥ

ΑΠ-02

Κλίμακα 1:60 · Α3
09/11/2026 · R00

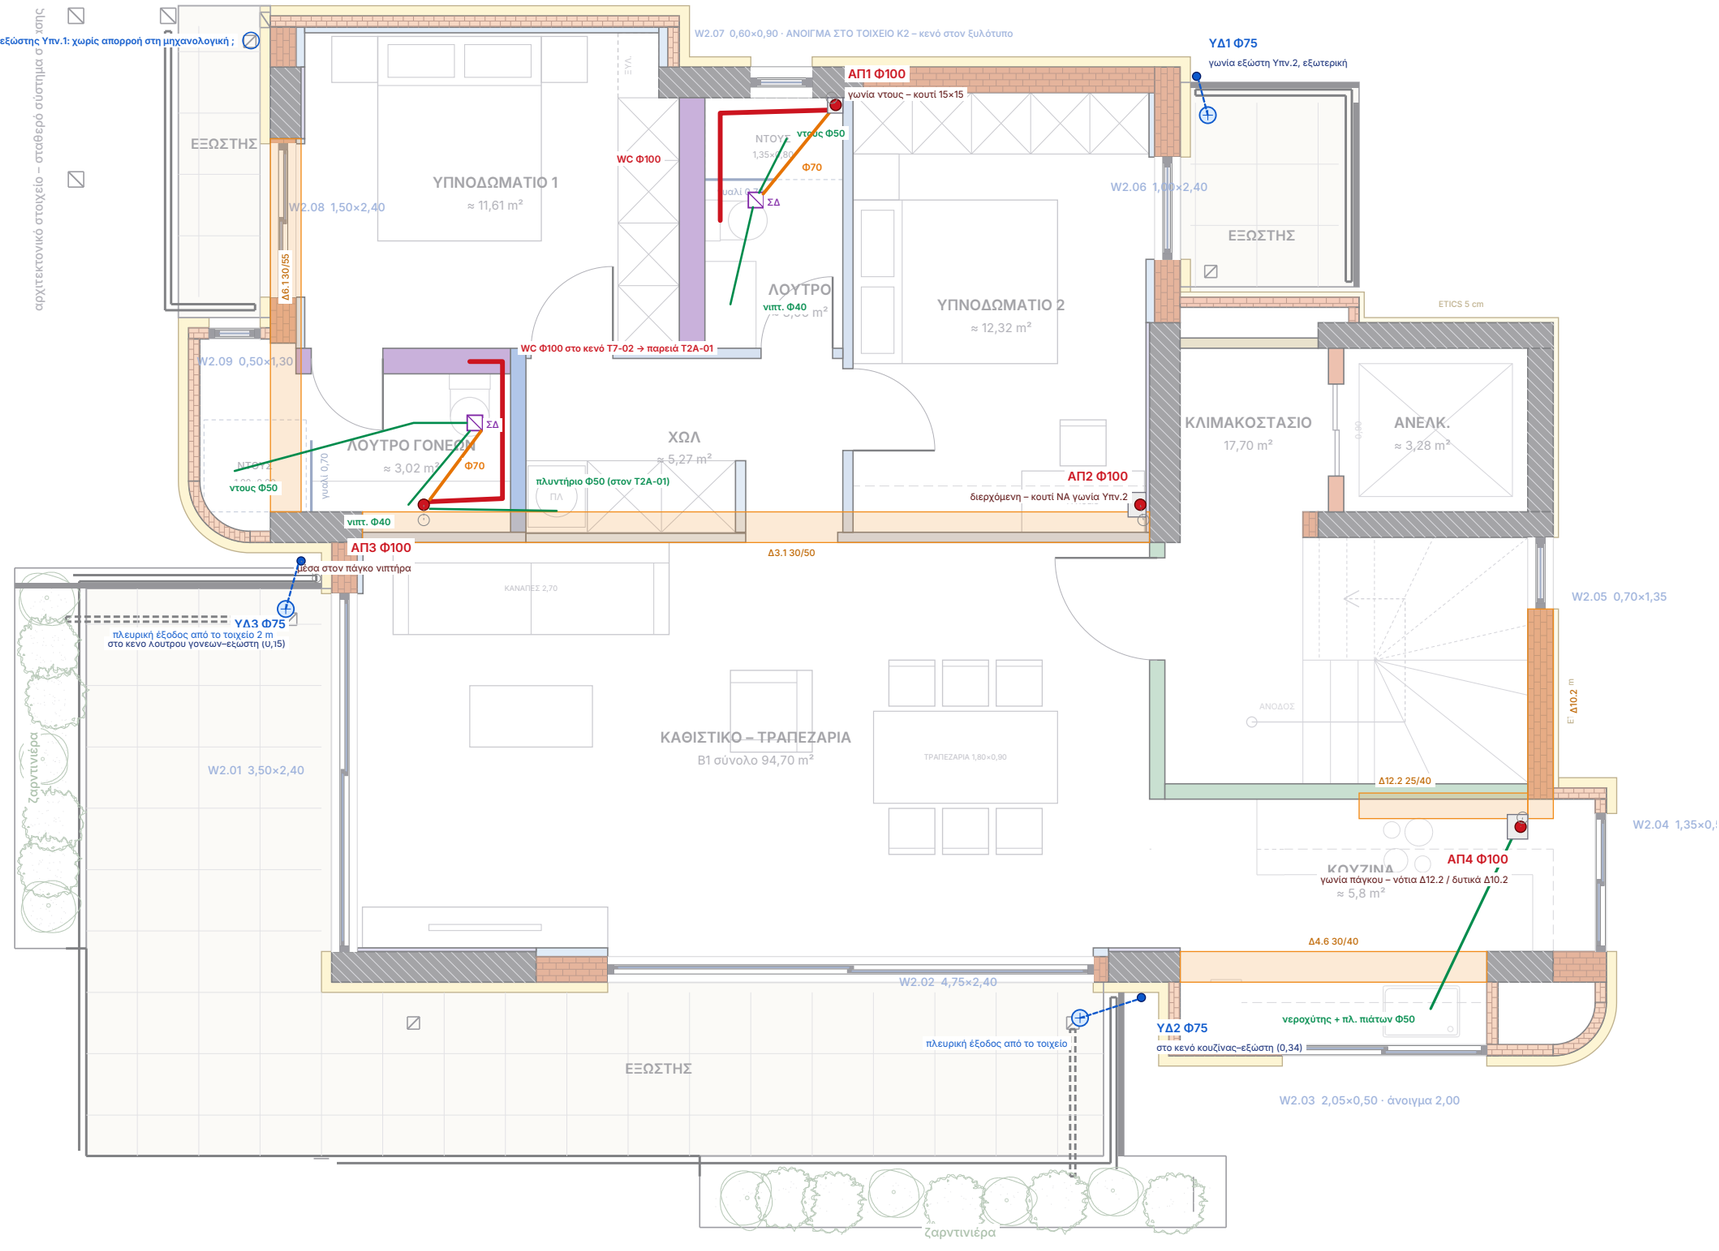


ΥΠΟΜΝΗΜΑ

- Στήλη λυμάτων ΑΠ Φ100 – U-PVC 6 atm, συνεχίζει ως αερισμός
- Θέση μηχανολόγου όπου μετακινήθηκε (διακεκομμένη)
- Λεκάνη → στήλη Φ100 (ή Φ90 όπου γράφεται)
- Σιφώνι δαπέδου → στήλη Φ70
- Ντους / πλυντήριο Φ50 · νιπτήρας Φ40 · νεροχύτης Φ50
- Σιφώνι δαπέδου (ΣΔ)
- Υδρορροή ΥΔ Φ75 – έξω από πλάκα / γέμισμα
- Σιφώνι ομβρίων εξώστη · διακεκ. = πλευρική έξοδος
- Δοκός (Σ4/Σ5) – καμία οπή

ΣΗΜΕΙΩΣΕΙΣ Α΄·Β΄·Γ΄ (ίδιοι)

1. Θέσεις και διατομές της μηχανολογικής (σχέδια Α-04/05/06): ΑΠ1 λουτρό, ΑΠ3 λουτρό γονέων, ΑΠ4 κουζίνα, ΑΠ2 διερχόμενη.
2. ΑΠ3 και ΑΠ2 μετακινήθηκαν 0,15 m βόρεια: η θέση του μηχανολόγου πέφτει πάνω στη Δ3.1 (y 4,85–5,15).
3. ΑΠ4 στη γωνία νότια της Δ12.2 και δυτικά της Δ10.2 (η θέση του μηχανολόγου έπεφτε στις δοκούς).
4. Λεκάνη γονέων: Φ100 στο κενό του Τ7-02 προς τα δεξιά και κατά μήκος του Τ2Α-01, όπως η μελέτη. Με γέμισμα 15 cm η κλίση στο δάπεδο να μην ξεπερνά 1,5% ή Φ90.
5. Σιφώνια δαπέδου δίπλα στις λεκάνες (θέσεις μηχανολόγου). Ντους γονέων Φ50 ~2,4 m στο γέμισμα.
6. Πλυντήριο: η νέα θέση στο χωλ είναι δίπλα στο λουτρό γονέων → Φ50 στην ΑΠ3 μέσα στον Τ2Α-01 (η μελέτη το πήγαινε στο σιφώνι του λουτρού).
7. Υδρορροές ΥΔ1–ΥΔ3 Φ75 εξωτερικές στις γωνίες/κενά των εξωστών, πλευρικά στόμια – χιτώνια στα τοιχεία πριν τη σκυροδέτηση (σημείωση Σ4).

ΕΡΓΟ	ΘΕΜΑ ΣΧΕΔΙΟΥ	ΒΑΣΗ	ΑΡ. ΣΧΕΔΙΟΥ
ΠΕΝΤΑΟΡΟΦΟ ΚΤΗΡΙΟ ΚΑΤΟΙΚΙΩΝ – ΑΡΓΥΡΟΥΠΟΛΗ Κωνσταντινουπόλεως 12 & Αγ. Βαρβάρας · Ο.Τ. 103-15 Εργοδότης: INTERKAT Α.Ε. · Κατασκευή: ARKAD Ι.Κ.Ε.	**ΑΠΟΧΕΤΕΥΣΗ – Α΄·Β΄·Γ΄ ΟΡΟΦΟΣ** Αποχετεύσεις λυμάτων · υδρορροές · κατά μηχανολογική μελέτη αδείας Α΄ · Β΄ · Γ΄ ΟΡΟΦΟΣ – τυπικός (Β1)	Μηχ. μελέτη αδείας Α-04/05/06 · τοιχοποιίες τυπικού R25 · Σ4/Σ5	**ΑΠ-03** **Κλίμακα 1:60 · Α3** 09/11/2026 · R00

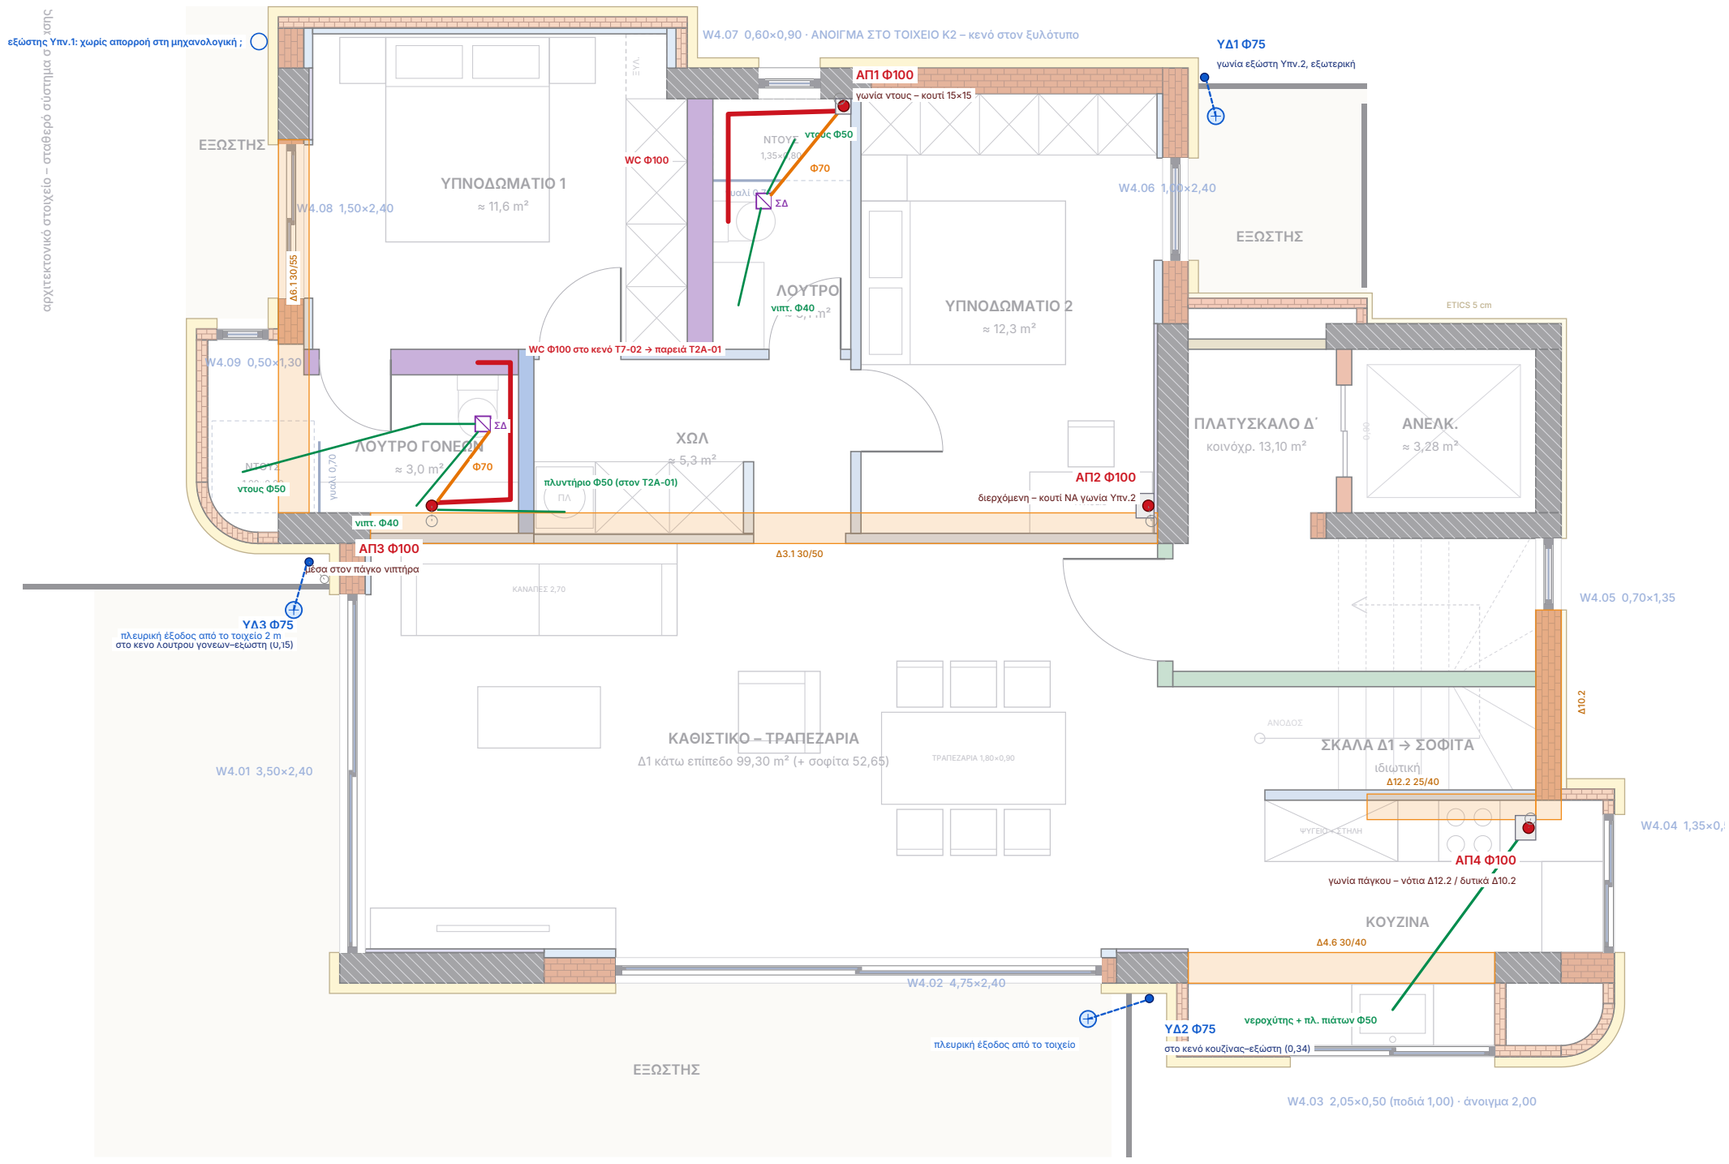

ΕΡΓΟ

ΠΕΝΤΑΟΡΟΦΟ ΚΤΗΡΙΟ ΚΑΤΟΙΚΙΩΝ – ΑΡΓΥΡΟΥΠΟΛΗ
Κωνσταντινουπόλεως 12 & Αγ. Βαρβάρας · Ο.Τ. 103-15
Εργοδότης: INTERKAT Α.Ε. · Κατασκευή: ARKAD Ι.Κ.Ε.

ΘΕΜΑ ΣΧΕΔΙΟΥ


ΑΠΟΧΕΤΕΥΣΗ – Δ΄ ΟΡΟΦΟΣ
Αποχετεύσεις λυμάτων · υδρορροές · κατά μηχανολογική μελέτη αδείας
Δ΄ ΟΡΟΦΟΣ – Δ1 κάτω επίπεδο μεζονέτας

ΒΑΣΗ

Μηχ. μελέτη αδείας Α-07 · τοιχοποιίες Δ΄ R04


ΑΡ. ΣΧΕΔΙΟΥ

ΑΠ-04
Κλίμακα 1:60 · Α3
09/11/2026 · R00

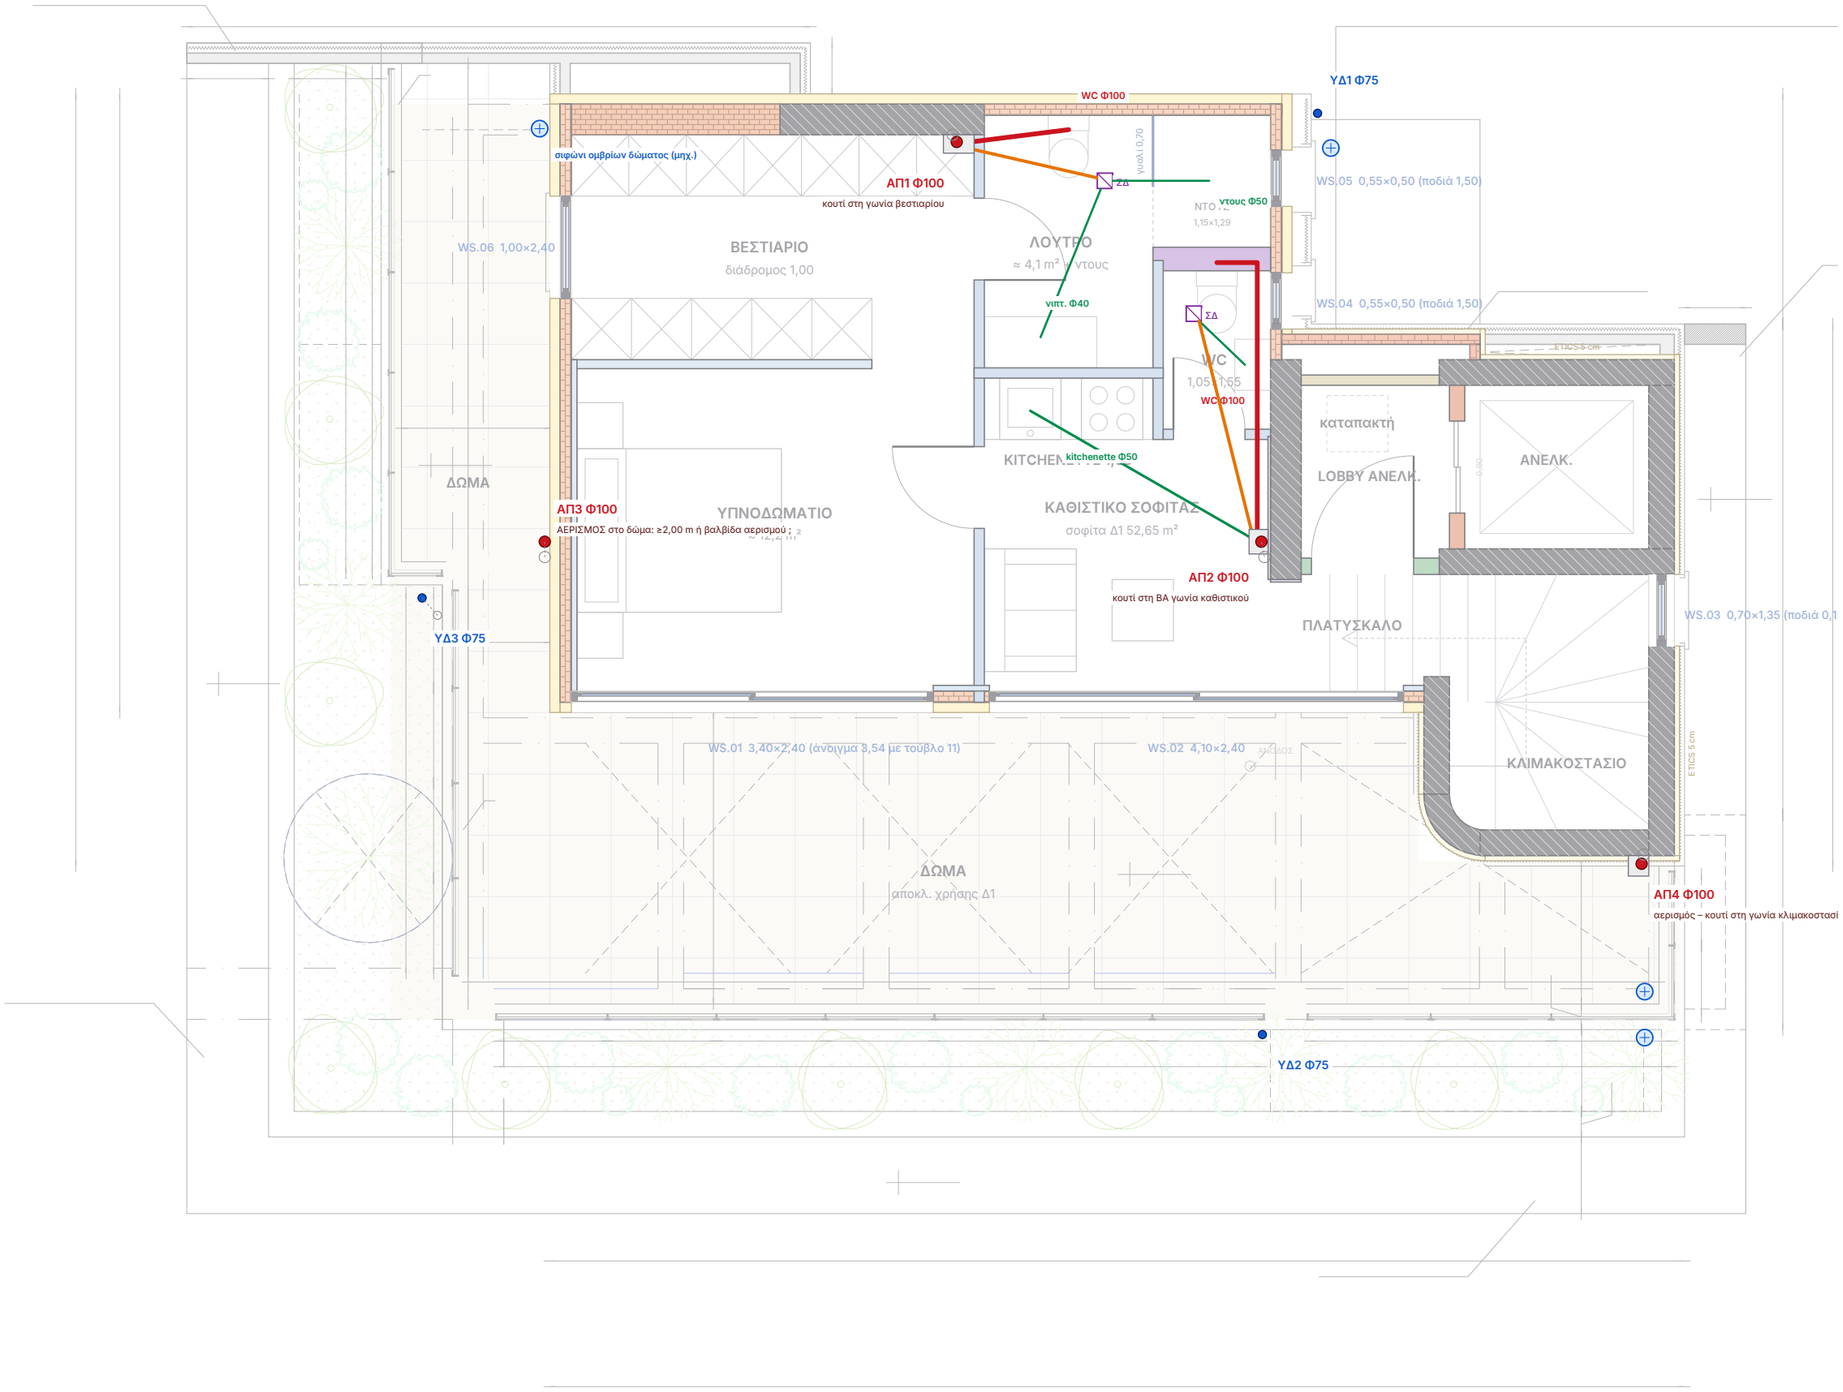

ΕΡΓΟ	ΘΕΜΑ ΣΧΕΔΙΟΥ	ΒΑΣΗ	ΑΡ. ΣΧΕΔΙΟΥ
ΠΕΝΤΑΟΡΟΦΟ ΚΤΗΡΙΟ ΚΑΤΟΙΚΙΩΝ – ΑΡΓΥΡΟΥΠΟΛΗ Κωνσταντινουπόλεως 12 & Αγ. Βαρβάρας · Ο.Τ. 103-15 Εργοδότης: INTERKAT Α.Ε. · Κατασκευή: ARKAD Ι.Κ.Ε.	**ΑΠΟΧΕΤΕΥΣΗ – ΣΟΦΙΤΑ** Αποχετεύσεις λυμάτων · υδρορροές · κατά μηχανολογική μελέτη αδείας ΣΟΦΙΤΑ – Δ1 πάνω επίπεδο · δώμα	Μηχ. μελέτη αδείας Α-08 · τοιχοποιίες σοφίτας R04	**ΑΠ-05** **Κλίμακα 1:60 · Α3** 09/11/2026 · R00

ΚΑΤΑΚΟΡΥΦΟ ΔΙΑΓΡΑΜΜΑ (σχηματικό) – κατά μηχανολογική Α-09

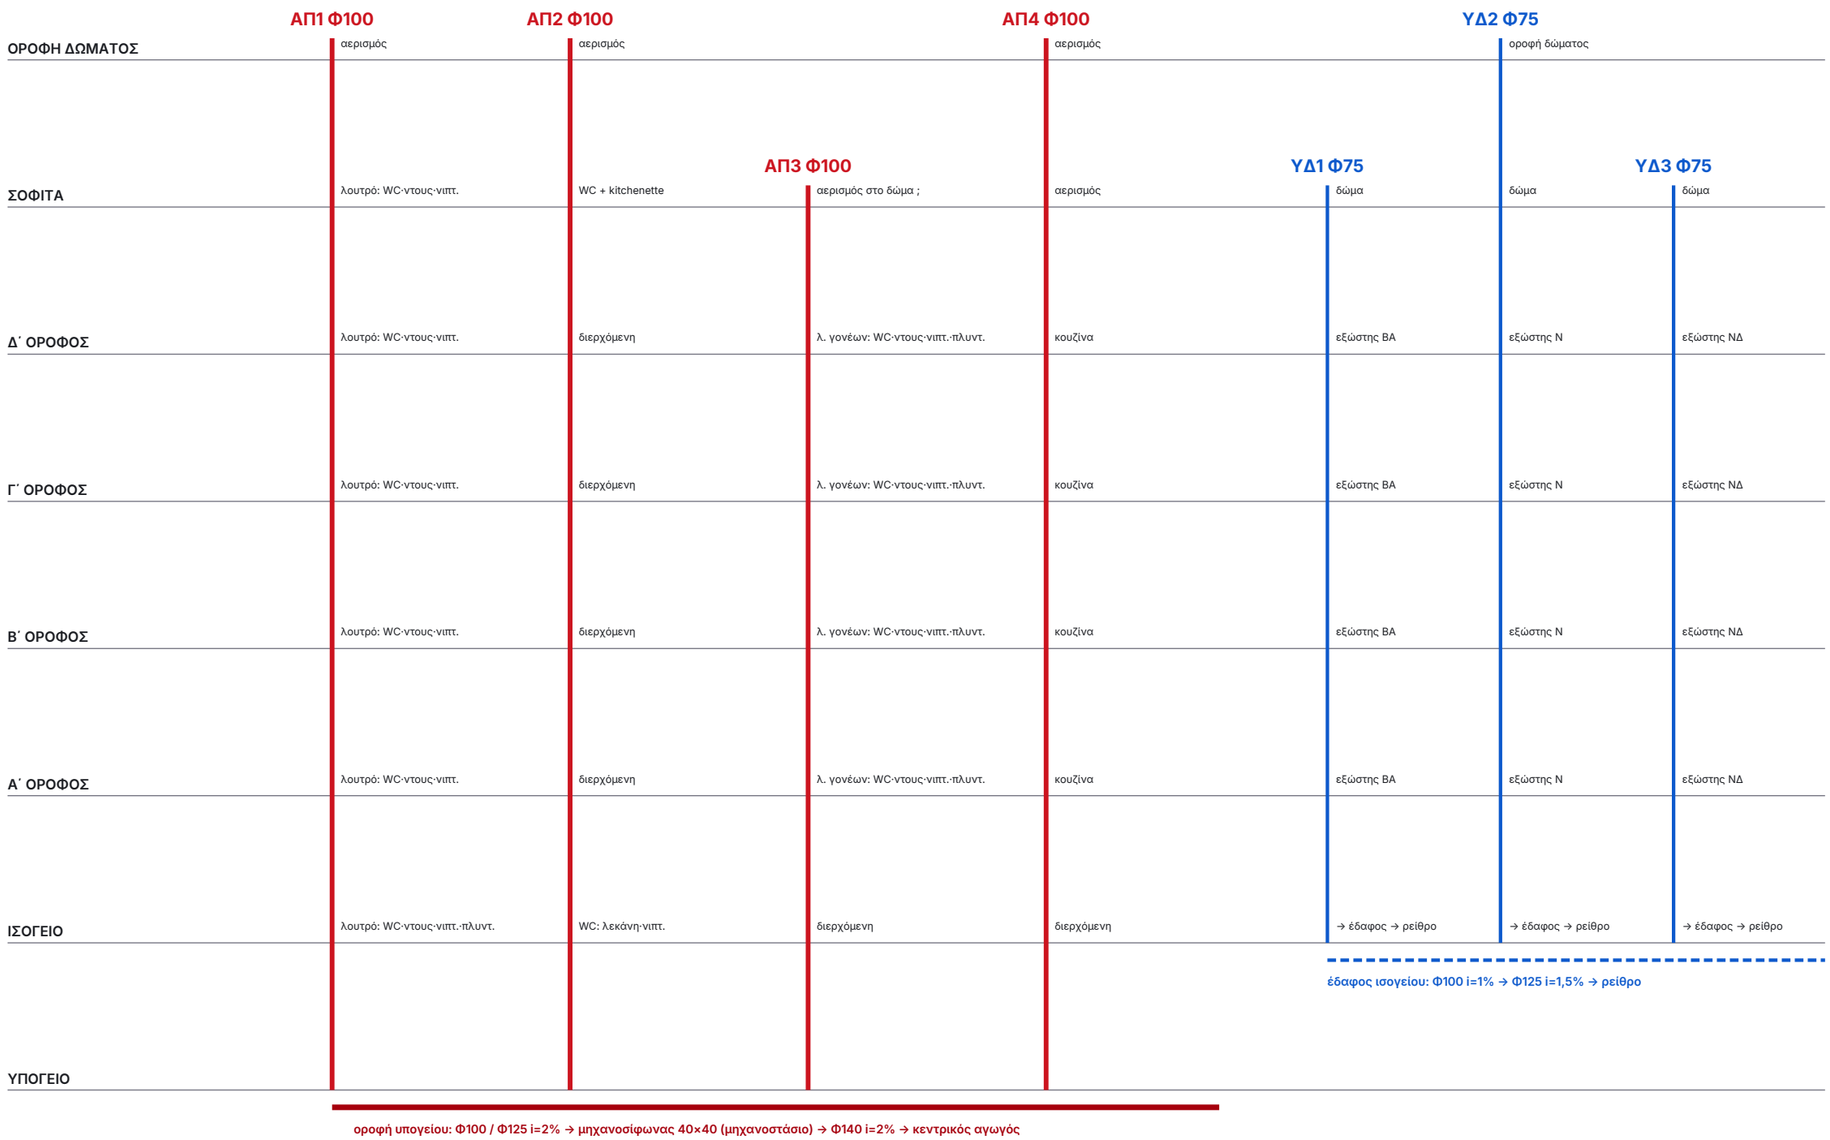

ΘΕΣΕΙΣ ΣΤΗΛΩΝ & ΑΛΛΑΓΕΣ ΣΕ ΣΧΕΣΗ ΜΕ ΤΗ ΜΕΛΕΤΗ

Στήλη	Μελέτη x/y	Τελική x/y	Λόγος
ΑΠ1	6,29 / 0,80	6,33 / 0,87	παρειά Κ2
ΑΠ2	9,34 / 4,93	9,31 / 4,78	πάνω στη Δ3.1
ΑΠ3	2,30 / 4,93	2,30 / 4,78	πάνω στη Δ3.1
ΑΠ4	13,05 / 7,84	13,03 / 7,93	γωνία Δ12.2/Δ10.2
ΥΔ1	9,86 / 0,59	9,86 / 0,59	–
ΥΔ2	9,33 / 9,59	9,32 / 9,60	–
ΥΔ3	1,25 / 5,50	1,10 / 5,33	μέσα στο τοιχείο 2 m
ΜΣ	14,16 / 8,97	12,55 / 8,95	υποσταθμός ΔΕΔΔΗΕ

ΕΚΚΡΕΜΟΤΗΤΕΣ – ΑΠΟΦΑΣΕΙΣ

1. Εξώστης Υπν.1 (Α΄–Δ΄): η μηχανολογική δεν δείχνει απορροή.
2. Εμπρός εξώστης: η μελέτη έχει 2 υδρορροές (ΥΔ2, ΥΔ3), όχι 3. Η τρίτη στο τοιχείο 2 m δεν υπάρχει στη μελέτη.
3. ΑΠ3 πάνω από τον Δ΄: αερισμός στο δώμα ή βαλβίδα αερισμού.
4. Γέμισμα 15 cm (+6,75 → +6,90): ελέγχεται η λεκάνη γονέων Φ100 (κλίση ≤1,5% ή Φ90) και το ντους γονέων Φ50 ~2,4 m.
5. Χιτώνια σε όλες τις πλάκες και στα τοιχεία των εξωστών πριν τη σκυροδέτηση· καμία οπή σε δοκό.
6. Ενημέρωση μηχανολόγου για: ΑΠ2/ΑΠ3/ΑΠ4/ΥΔ3, μηχανοσίφωνα + Φ140, πτώση νεροχύτη ισογείου, πλυντήριο → ΑΠ3.
7. Υλικά κατά τεύχος: U-PVC 6 atm στήλες/οριζόντια, 4 atm αερισμοί (ΤΟΤΕΕ 2412/86).

ΕΡΓΟ	ΘΕΜΑ ΣΧΕΔΙΟΥ	ΒΑΣΗ	ΑΡ. ΣΧΕΔΙΟΥ
ΠΕΝΤΑΟΡΟΦΟ ΚΤΗΡΙΟ ΚΑΤΟΙΚΙΩΝ – ΑΡΓΥΡΟΥΠΟΛΗ Κωνσταντινουπόλεως 12 & Αγ. Βαρβάρας · Ο.Τ. 103-15 Εργοδότης: INTERKAT Α.Ε. · Κατασκευή: ARKAD Ι.Κ.Ε.	**ΚΑΤΑΚΟΡΥΦΟ ΔΙΑΓΡΑΜΜΑ – ΠΙΝΑΚΑΣ ΣΤΗΛΩΝ** Λύματα ΑΠ1–ΑΠ4 · όμβρια ΥΔ1–ΥΔ3 · συλλεκτήριοι ΟΛΟ ΤΟ ΚΤΙΡΙΟ	Μηχ. μελέτη αδείας (πράξη 1928938) Α-02…Α-09 + τεύχος	**ΑΠ-06** **Χωρίς κλίμακα · Α3** 09/11/2026 · R00