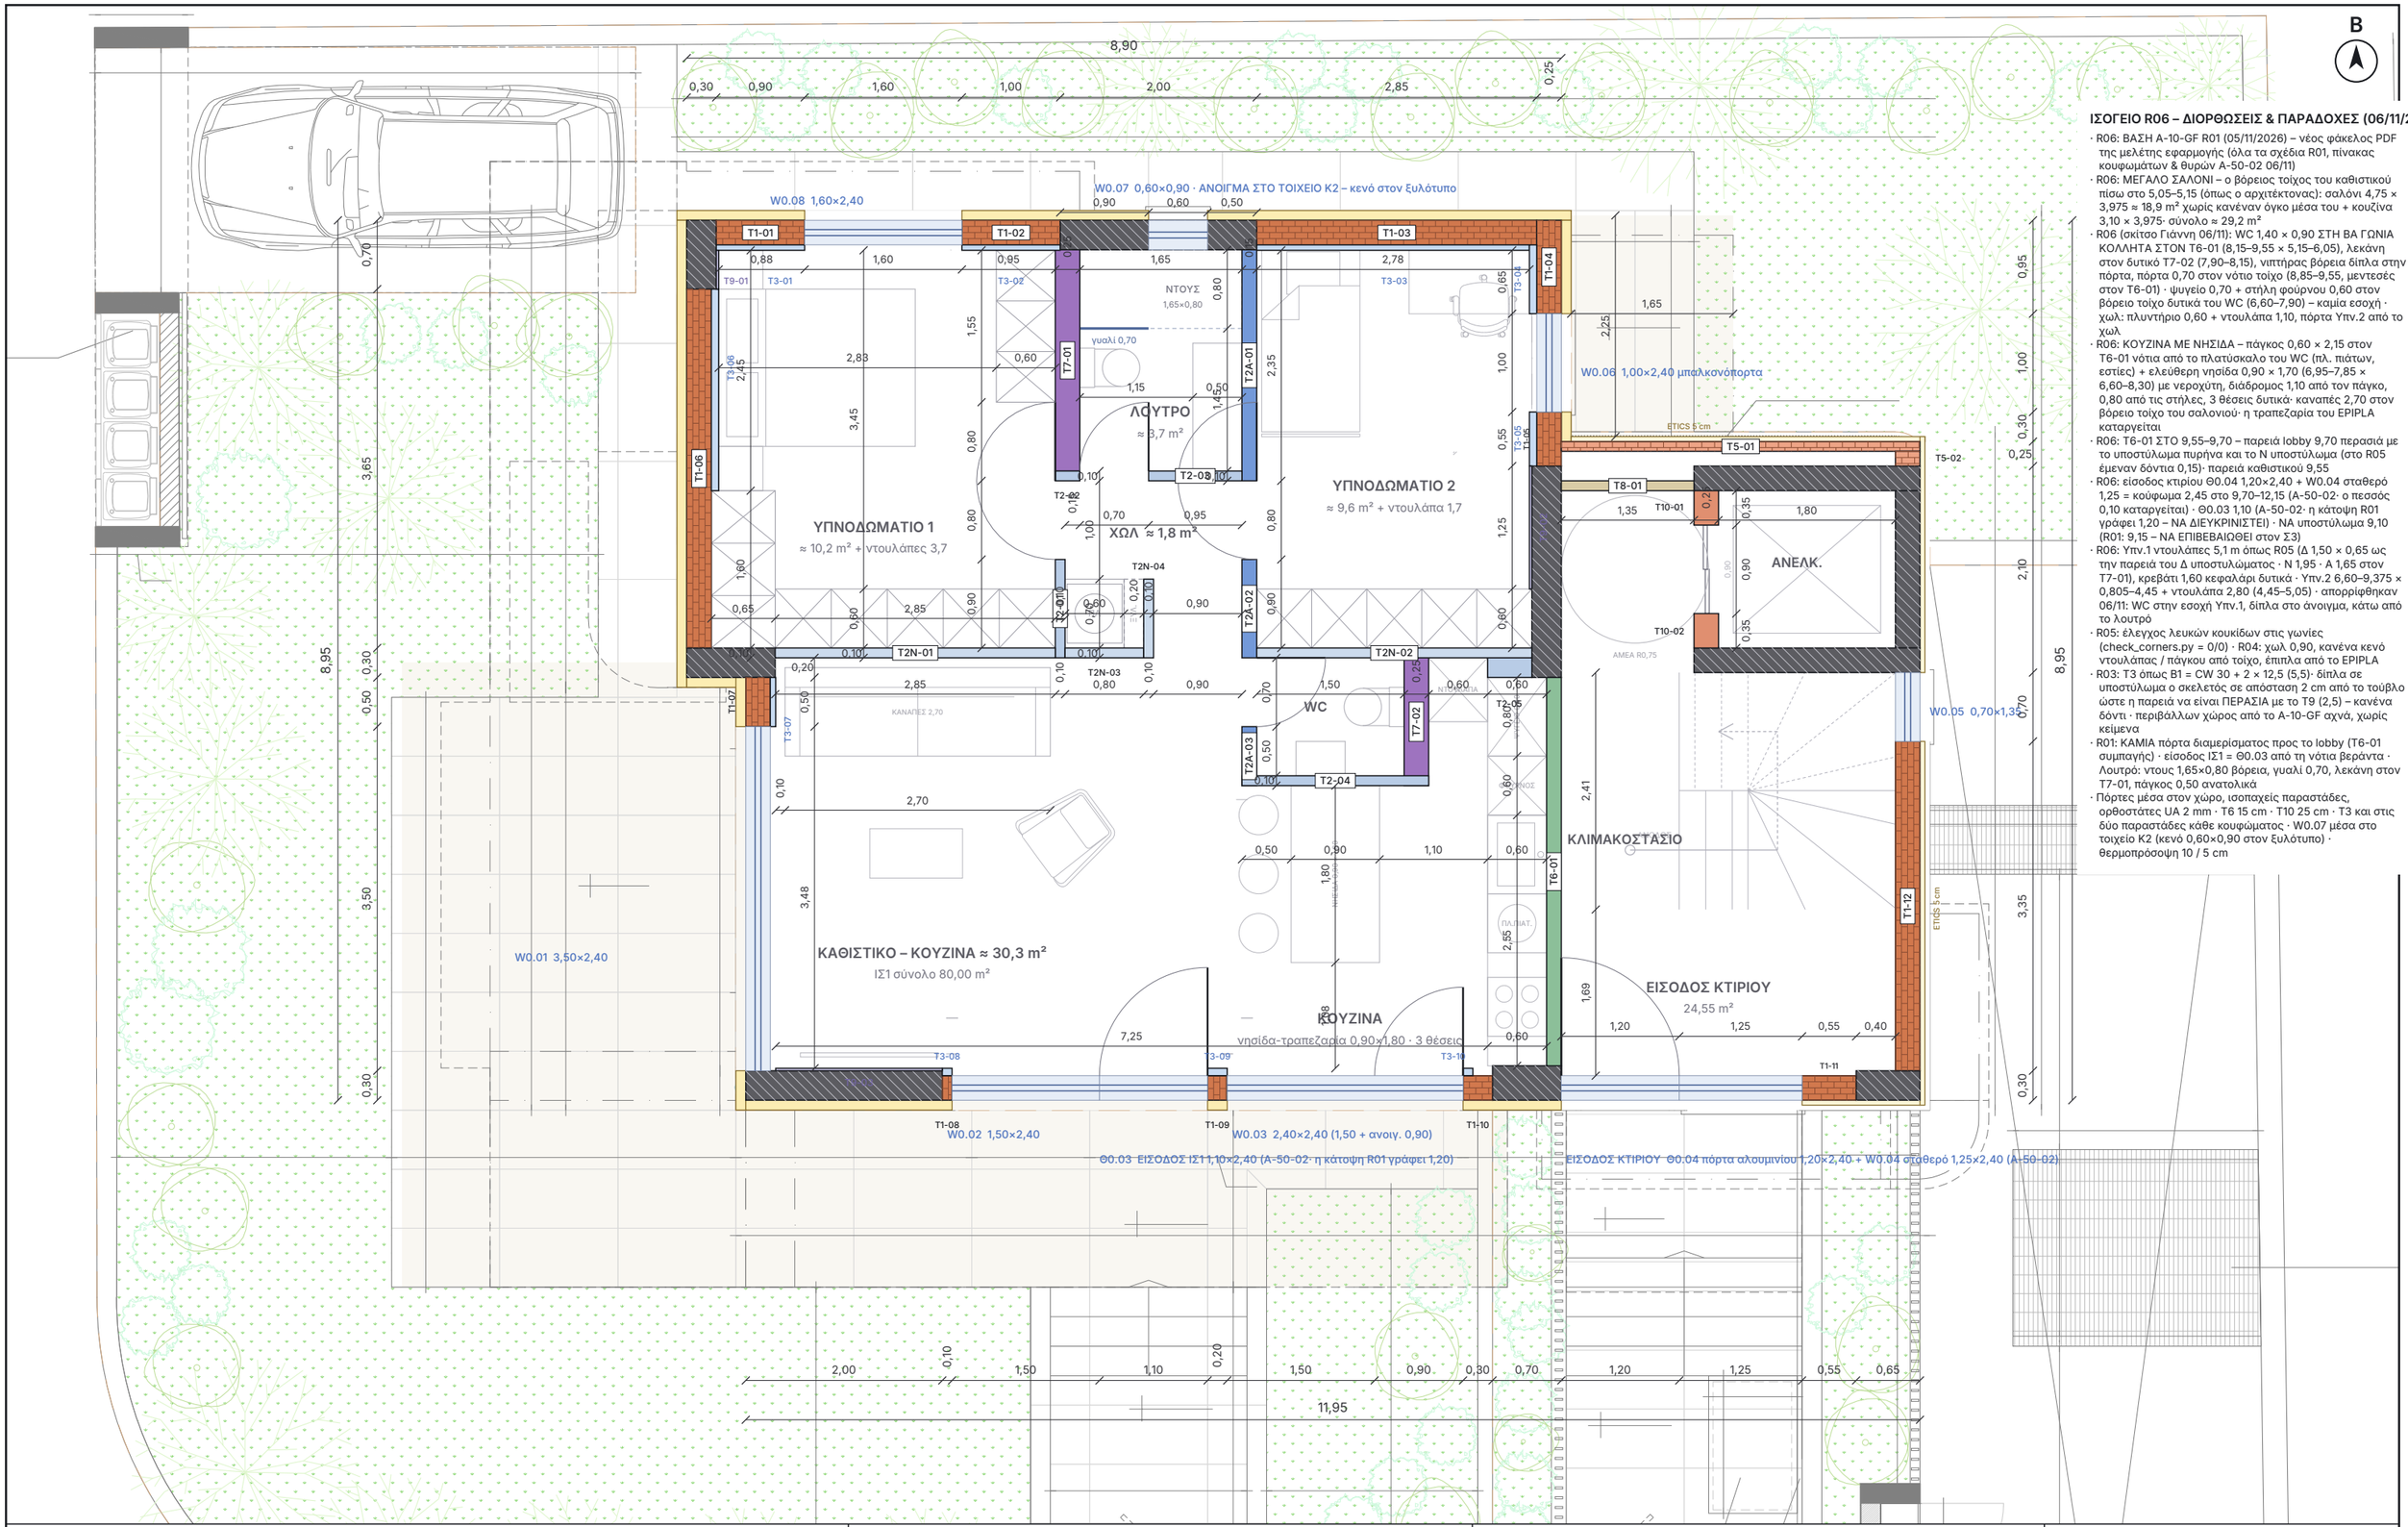


ΙΣΟΓΕΙΟ R06 – ΔΙΟΡΘΩΣΕΙΣ & ΠΑΡΑΔΟΧΕΣ (06/11/2026)


- R06: ΒΑΣΗ Α-10-GF R01 (05/11/2026) – νέος φάκελος PDF της μελέτης εφαρμογής (όλα τα σχέδια R01, πίνακας κουφωμάτων & θυρών Α-50-02 06/11)
- R06: ΜΕΓΑΛΟ ΣΑΛΟΝΙ – ο βόρειος τοίχος του καθιστικού πίσω στο 5,05–5,15 (όπως ο αρχιτέκτονας): σαλόνι 4,75 × 3,975 ≈ 18,9 m² χωρίς κανέναν όγκο μέσα του + κουζίνα 3,10 × 3,975· σύνολο ≈ 29,2 m²
- R06 (σκίτσο Γιάννη 06/11): WC 1,40 × 0,90 ΣΤΗ ΒΑ ΓΩΝΙΑ ΚΟΛΛΗΤΑ ΣΤΟΝ Τ6-01 (8,15–9,55 × 5,15–6,05), λεκάνη στον δυτικό Τ7-02 (7,90–8,15), νιπτήρας βόρεια δίπλα στην πόρτα, πόρτα 0,70 στον νότιο τοίχο (8,85–9,55, μεντεσές στον Τ6-01) · ψυγείο 0,70 + στήλη φούρνου 0,60 στον βόρειο τοίχο δυτικά του WC (6,60–7,90) – καμία εσοχή · χωλ: πλυντήριο 0,60 + ντουλάπα 1,10, πόρτα Υπν.2 από το χωλ
- R06: ΚΟΥΖΙΝΑ ΜΕ ΝΗΣΙΔΑ – πάγκος 0,60 × 2,15 στον Τ6-01 νότια από το πλατύσκαλο του WC (πλ. πιάτων, εστίες) + ελεύθερη νησίδα 0,90 × 1,70 (6,95–7,85 × 6,60–8,30) με νεροχύτη, διάδρομος 1,10 από τον πάγκο, 0,80 από τις στήλες, 3 θέσεις δυτικά· καναπές 2,70 στον βόρειο τοίχο του σαλονιού· η τραπεζαρία του EPIPLA καταργείται
- R06: Τ6-01 ΣΤΟ 9,55–9,70 – παρειά lobby 9,70 περασιά με το υποστύλωμα πυρήνα και το Ν υποστύλωμα (στο R05 έμεναν δόντια 0,15)· παρειά καθιστικού 9,55
- R06: είσοδος κτιρίου Θ0.04 1,20×2,40 + W0.04 σταθερό 1,25 = κούφωμα 2,45 στο 9,70–12,15 (Α-50-02· ο πεσσός 0,10 καταργείται) · Θ0.03 1,10 (Α-50-02· η κάτοψη R01 γράφει 1,20 – ΝΑ ΔΙΕΥΚΡΙΝΙΣΤΕΙ) · ΝΑ υποστύλωμα 9,10 (R01: 9,15 – ΝΑ ΕΠΙΒΕΒΑΙΩΘΕΙ στον Σ3)
- R06: Υπν.1 ντουλάπες 5,1 m όπως R05 (Δ 1,50 × 0,65 ως την παρειά του Δ υποστυλώματος · Ν 1,95 · Α 1,65 στον Τ7-01), κρεβάτι 1,60 κεφαλάρι δυτικά · Υπν.2 6,60–9,375 × 0,805–4,45 + ντουλάπα 2,80 (4,45–5,05) · απορρίφθηκαν 06/11: WC στην εσοχή Υπν.1, δίπλα στο άνοιγμα, κάτω από το λουτρό
- R05: έλεγχος λευκών κουκίδων στις γωνίες (check_corners.py = 0/0) · R04: χωλ 0,90, κανένα κενό ντουλάπας / πάγκου από τοίχο, έπιπλα από το EPIPLA
- R03: Τ3 όπως Β1 = CW 30 + 2 × 12,5 (5,5)· δίπλα σε υποστύλωμα ο σκελετός σε απόσταση 2 cm από το τούβλο ώστε η παρειά να είναι ΠΕΡΑΣΙΑ με το Τ9 (2,5) – κανένα δόντι · περιβάλλων χώρος από το Α-10-GF αχνά, χωρίς κείμενα
- R01: ΚΑΜΙΑ πόρτα διαμερίσματος προς το lobby (Τ6-01 συμπαγής) · είσοδος ΙΣ1 = Θ0.03 από τη νότια βεράντα · Λουτρό: ντους 1,65×0,80 βόρεια, γυαλί 0,70, λεκάνη στον Τ7-01, πάγκος 0,50 ανατολικά
- Πόρτες μέσα στον χώρο, ισοπαχείς παραστάδες, ορθοστάτες UA 2 mm · Τ6 15 cm · Τ10 25 cm · Τ3 και στις δύο παραστάδες κάθε κουφώματος · W0.07 μέσα στο τοιχείο Κ2 (κενό 0,60×0,90 στον ξυλότυπο) · θερμοπρόσοψη 10 / 5 cm

ΕΡΓΟ	ΘΕΜΑ ΣΧΕΔΙΟΥ	ΒΑΣΗ	ΑΡ. ΣΧΕΔΙΟΥ
ΠΕΝΤΑΟΡΟΦΟ ΚΤΗΡΙΟ ΚΑΤΟΙΚΙΩΝ – ΑΡΓΥΡΟΥΠΟΛΗ Κωνσταντινουπόλεως 12 & Αγ. Βαρβάρας · Ο.Τ. 103-15 Εργοδότης: INTERKAT Α.Ε. · Κατασκευή: ARKAD Ι.Κ.Ε.	**ΚΑΤΟΨΗ ΤΟΙΧΟΠΟΙΙΩΝ – ΙΣΟΓΕΙΟΥ** Είδη τοιχοποιιών · διαστάσεις χάραξης · κουφώματα · εξώστες ΙΣΟΓΕΙΟ – ΙΣ1	Βάση: Α-10-GF R01 (05/11/2026, Drive) · Σ3_ΕΦ · κανόνες Β1 R20	**Τ-01** **Κλίμακα 1:60 · Α3** 06/11/2026 · R06

T1 Εξωτερική οπτοπλινθοδομή

1:4

πάχος 25 cm

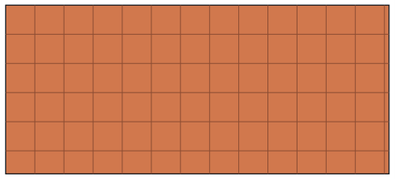

θερμομονωτικό τούβλο κάθετων οπών 25 cm · θερμοπρόσοψη 10 cm έξω · επένδυση T3 μέσα όπου σημειώνεται




Τοίχοι: T1-01, T1-02, T1-03, T1-04, T1-05, T1-06, T1-07, T1-08, T1-09, T1-10, T1-11, T1-12

Μήκος 15,10 m · επιφάνεια ≈ 45,3 m²


T5 Οπτοπλινθοδομή πυρήνα

1:4

πάχος 10 cm

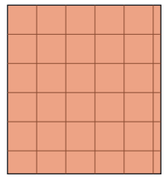

θερμομονωτικό τούβλο κάθετων οπών 10 cm · γύρω από τον πυρήνα (ανελκυστήρας – ηλεκτροστάσιο)

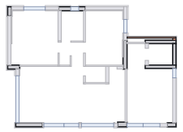


Τοίχοι: T5-01, T5-02

Μήκος 3,90 m · επιφάνεια ≈ 11,7 m²


T10 Μέτωπο ανελκυστήρα

1:4

πάχος 25 cm

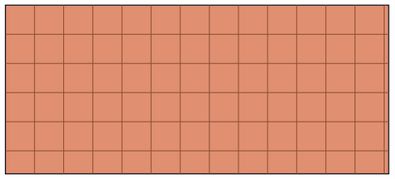

θερμομονωτικό τούβλο κάθετων οπών 25 cm · μέτωπο φρεατίου εκατέρωθεν της πόρτας 0,90 · ισοπαχές με τα τοιχεία 25 του φρεατίου (Σ5), περασιά και στις δύο παρειές, ώστε να κάθεται σωστά η κάσα της πόρτας ορόφου · θέση πόρτας προς επιβεβαίωση από τον προμηθευτή

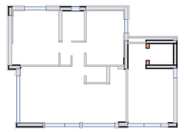


Τοίχοι: T10-01, T10-02

Μήκος 0,70 m · επιφάνεια ≈ 2,1 m²


T3 Επένδυση τοίχου

1:4

πάχος 5,5 cm

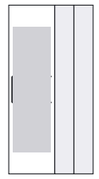

σκελετός 30 · 2 × γυψοσανίδα 12,5 · στις εσωτερικές παρειές των T1 – ΟΧΙ όπου πλακάκι ή ντουλάπα, ΟΧΙ στα έρκερ

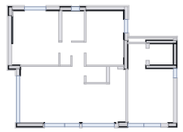

Τοίχοι: T3-01, T3-02, T3-03, T3-04, T3-05, T3-06, T3-07, T3-08, T3-09, T3-10

Μήκος 8,88 m · επιφάνεια ≈ 26,6 m²


T9 Επένδυση υποστυλώματος

1:4

πάχος 2,5 cm



κόλλα + 1 × γυψοσανίδα 12,5 (ένα φύλλο) · στις παρειές υποστυλωμάτων μέσα στα διαμερίσματα – ΟΧΙ όπου πλακάκι ή ντουλάπα

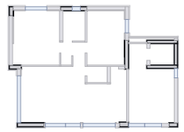


Τοίχοι: T9-01, T9-02, T9-03

Μήκος 3,34 m · επιφάνεια ≈ 10,0 m²


T2 Χώρισμα γυψοσανίδας

1:4

πάχος 10 cm

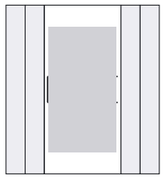

2 × γυψοσανίδα 12,5 · σκελετός CW 50 · 2 × γυψοσανίδα 12,5 · εσωτερικά χωρίσματα · ανθυγρή γυψοσανίδα στην πλευρά των λουτρών · ανοίγματα πορτών με ορθοστάτες UA 50 (2 mm)

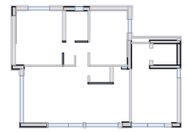


Τοίχοι: T2-01, T2-02, T2-03, T2-04, T2-05

Μήκος 4,55 m · επιφάνεια ≈ 13,7 m²


T2N Χώρισμα γυψ. – πλευρά ντουλάπας

1:4

πάχος 8,75 cm

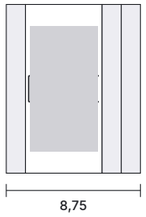

1 × γυψοσανίδα 12,5 (πλευρά ντουλάπας) · σκελετός CW 50 · 2 × γυψοσανίδα 12,5 · όπου η μία παρειά βλέπει σε ντουλάπα: ένα φύλλο αρκεί (κανόνας R15)

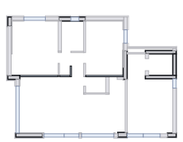


Τοίχοι: T2N-01, T2N-02, T2N-03, T2N-04

Μήκος 7,25 m · επιφάνεια ≈ 21,8 m²


T2A Χώρισμα γυψοσανίδας 15

1:4

πάχος 15 cm

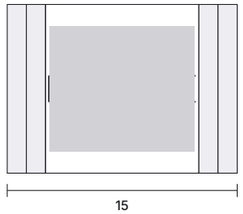

2 × γυψοσανίδα 12,5 · σκελετός CW 100 + πετροβάμβακας · 2 × γυψοσανίδα 12,5 · λουτρό γονέων / χωλ · υπνοδωμάτια · ανοίγματα πορτών με ορθοστάτες UA 100 (2 mm)

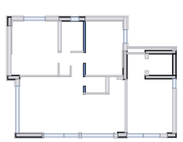


Τοίχοι: T2A-01, T2A-02, T2A-03

Μήκος 3,95 m · επιφάνεια ≈ 11,8 m²


T7 Τοίχος λεκάνης WC

1:4

πάχος 25 cm

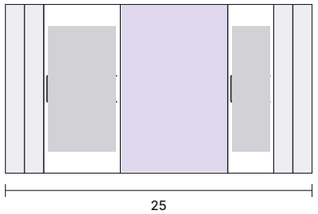

2 × γυψοσανίδα 12,5 · σκελετός CW 50 · κενό 12 cm (καζανάκι γυψοσανίδας στον σκελετό + κατακόρυφη στήλη Ø110, έξοδος Ø90) · σκελετός CW 30 · 2 × γυψοσανίδα 12,5 · ΟΛΟΙ οι τοίχοι λεκανών · ανθυγρή προς το λουτρό · στην πλευρά ντουλάπας 1 φύλλο · ανοίγματα πορτών με ορθοστάτες UA 50 (2 mm)

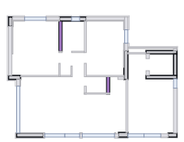


Τοίχοι: T7-01, T7-02

Μήκος 3,55 m · επιφάνεια ≈ 10,6 m²


T6 Τοίχος κλιμακοστασίου

1:4

πάχος 15 cm

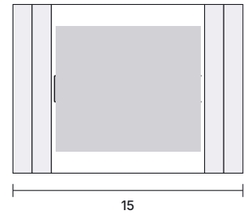

2 × γυψοσανίδα 12,5 πυράντοχη · σκελετός CW 100 + πετροβάμβακας · 2 × γυψοσανίδα 12,5 πυράντοχη · προς κοινόχρηστους χώρους · 15 cm · άνοιγμα πόρτας εισόδου (ασφαλείας) με ορθοστάτες UA 100 (2 mm) κατά Knauf

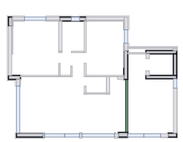


Τοίχοι: T6-01

Μήκος 3,95 m · επιφάνεια ≈ 11,8 m²


T8 Τοίχος shaft

1:4

πάχος 10 cm

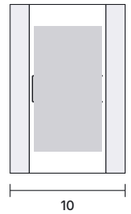

πλαίσιο + ανοιγόμενα φύλλα γυψοσανίδας · μέτωπο shaft ηλεκτρολογικών

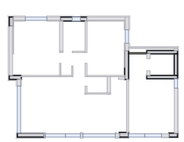

Τοίχοι: T8-01

Μήκος 1,35 m · επιφάνεια ≈ 4,1 m²

Επιφάνειες ενδεικτικές: μήκος × ύψος 3,00 m (τελικό δάπεδο – πλάκα) – οι τοίχοι ορίζονται μεταξύ ανοιγμάτων, χωρίς αφαίρεση κασών. T3 = επένδυση στην εσωτερική παρειά των T1 · T9 = περίμετρος υποστυλώματος × ύψος. R15: T2N = 1 φύλλο στην πλευρά ντουλάπας (T2N-01, T2N-02) · T7-01 1 φύλλο προς Υπν.1.

ΕΡΓΟ

ΠΕΝΤΑΟΡΟΦΟ ΚΤΗΡΙΟ ΚΑΤΟΙΚΙΩΝ – ΑΡΓΥΡΟΥΠΟΛΗ
Κωνσταντινουπόλεως 12 & Αγ. Βαρβάρας · Ο.Τ. 103-15
Εργοδότης: INTERKAT Α.Ε. · Κατασκευή: ARKAD Ι.Κ.Ε.

ΘΕΜΑ ΣΧΕΔΙΟΥ

ΕΙΔΗ ΤΟΙΧΟΠΟΙΙΩΝ – ΙΣΟΓΕΙΟΥ
Είδη τοιχοποιιών · ΙΣΟΓΕΙΟ – ΙΣ1
τομές 1:4 · μήκη – εμβαδά ανά είδος

ΒΑΣΗ

Βάση: κάτοψη τοιχοποιιών T-01 · κάτοψη A-10-GF

ΑΡ. ΣΧΕΔΙΟΥ

T-02
Κλίμακα 1:4 · A3
06/11/2026 · R06

ΠΡΟΜΕΤΡΗΣΗ ΤΟΙΧΟΠΟΙΙΩΝ – ΙΣΟΓΕΙΟ – ΙΣ1

τετραγωνικά ανά τυπολογία τοίχου · Η = 3,00 m (τελικό δάπεδο – κάτω παρειά πλάκας) · μήκη στον άξονα, χωρίς αφαίρεση κουφωμάτων · R06

	Τύπος	Περιγραφή	Πάχος cm	Τοίχοι	Μήκος m	Επιφάνεια m²
ΤΟΥΒΛΑ						
	T1	Εξωτερική οπτοπλινθοδομή	25	12	15,10	**45,3**
	T5	Οπτοπλινθοδομή πυρήνα	10	2	3,90	**11,7**
	T10	Μέτωπο ανελκυστήρα	25	2	0,70	**2,1**
	Σύνολο τουβλα					**59,1 m²**
ΧΩΡΙΣΜΑΤΑ ΓΥΨΟΣΑΝΙΔΑΣ						
	T2	Χώρισμα γυψοσανίδας	10	5	4,55	**13,7**
	T2N	Χώρισμα γυψ. – πλευρά ντουλάπας	8,8	4	7,25	**21,8**
	T2A	Χώρισμα γυψοσανίδας 15	15	3	3,95	**11,8**
	T7	Τοίχος λεκάνης WC	25	2	3,55	**10,6**
	T6	Τοίχος κλιμακοστασίου	15	1	3,95	**11,8**
	T8	Τοίχος shaft	10	1	1,35	**4,1**
	Σύνολο χωρισματα γυψοσανιδας					**73,8 m²**
ΕΠΕΝΔΥΣΕΙΣ						
	T3	Επένδυση τοίχου	5,5	10	8,88	**26,6**
	T9	Επένδυση υποστυλώματος	2,5	3	3,34	**10,0**
	Σύνολο επενδυσεις					**36,6 m²**
	ΣΥΝΟΛΟ ΤΟΙΧΟΠΟΙΙΩΝ ΙΣ1					**169,5 m²**

ΘΕΡΜΟΠΡΟΣΟΨΗ (ETICS)

10 cm στις όψεις των διαμερισμάτων · 5 cm στο κλιμακοστάσιο / πυρήνα · ύψος 3,20 m (με τη μετώπη πλάκας) · καθαρά = όψη − κουφώματα + λαμπάδες/ανώφλια

Ζώνη	Μήκος όψης m	Μικτά m²	Κουφώματα m²	Λαμπάδες m²	Καθαρά m²
ETICS 10 cm – διαμερίσματα	29,40	94,1	−27,2	+5,9	**72,8**
ETICS 5 cm – κλιμακοστάσιο / πυρήνας	14,05	45,0	−6,8	+2,0	**40,2**
Σύνολο ETICS					**113,0 m²**

ΣΗΜΕΙΩΣΕΙΣ ΚΑΤΟΨΗΣ

• Θέσεις τοίχων και ανοιγμάτων κατά την κάτοψη ισογείου A-10-GF R01 (EDGE, μελέτη εφαρμογής, αναθεώρηση R01 05/11/2026, φάκελος PDF της μελέτης εφαρμογής στο Drive του έργου) με τους κανόνες του B1 R20 και τις αλλαγές R01–R06 του Γιάννη. Διαστάσεις στο τούβλο / μπετό και στις παρειές της γυψοσανίδας, χωρίς τη θερμοπρόσοψη. Υποστυλώματα / τοιχεία από τα μαύρα γεμίσματα του A-10-GF, δοκοί από τον ξυλότυπο Σ3_ΕΦ (1:50, X0 868 / Y0 585 pt, 56,69 pt/m – Δ3.1 30/50 στο y 4,85–5,15)· το R01 δείχνει το N υποστύλωμα στο 9,15–9,45 αντί 9,10–9,45 – εδώ 9,10 όπως B1, να επιβεβαιωθεί.

• ΤΙ ΑΛΛΑΞΕ ΣΤΟ A-10-GF R01 (05/11/2026) σε σχέση με το R00 (23/07/2026): μόνο ετικέτες θυρών και μικρά στοιχεία – Θ0.03 γράφεται «1,20×2,40» (η γεωμετρία της κάτοψης και ο πίνακας A-50-02 λένε 1,10 → κρατήθηκε 1,10, ΝΑ ΔΙΕΥΚΡΙΝΙΣΤΕΙ), είσοδος κτιρίου Θ0.04 1,20 (ήταν 1,00) + W0.04 1,25 (ήταν 1,20), πύλες περίφραξης Θ0.02 / Θ0.04, γκαραζόπορτα Θ0.01 2,50×2,10, N υποστύλωμα 9,15, διακεκομμένες προβολές στο lobby και στη ΒΑ βεράντα. Οι τοίχοι του διαμερίσματος δεν άλλαξαν.

• Τ3 ΠΕΡΑΣΙΑ (R03, όπως B1): Τ3 = σκελετός CW 30 + 2 × γυψοσανίδα 12,5 (5,5 cm). Τα υποστυλώματα (30) προεξέχουν 5 cm από την εσωτερική παρειά του τούβλου (25) και παίρνουν κολλητή γυψοσανίδα Τ9 2,5 cm· όπου η Τ3 συνεχίζει δίπλα σε υποστύλωμα, ο σκελετός CW 30 στήνεται σε απόσταση 2 cm από το τούβλο ώστε η παρειά της γυψοσανίδας να είναι στο ίδιο επίπεδο με το Τ9: Τ3-06 (παρειά 1,125 = Τ9-01), Τ3-04/Τ3-05 (9,375 = Τ9-02), Τ3-08/09/10 (9,125 = Τ9-03). Αλλού η Τ3 κολλητά στο τούβλο: Β 0,805 · Δ καθιστικού 1,705. Όπου πλακάκι, ντουλάπα ή πάγκος: χωρίς Τ3 / Τ9 (γυμνό τούβλο / μπετό).

• ΒΟΡΕΙΟΣ ΤΟΙΧΟΣ ΚΑΘΙΣΤΙΚΟΥ ΣΤΗΝ ΑΛΛΗ ΠΛΕΥΡΑ ΤΟΥ ΔΟΚΑΡΙΟΥ (R06 – Γιάννης: «τον T2N-01/02/03 μετακίνησέ τον στην άλλη μεριά του δοκαριού»): κατά τον ξυλότυπο Σ3_ΕΦ η δοκός Δ3.1 30/50 τρέχει στο y 4,85–5,15 από το Δ υποστύλωμα (0,80–1,70 × 4,85–5,15) ως το υποστύλωμα πυρήνα (9,40–9,70 × 3,00–5,15). Οι T2N-01 (1,70–4,55), T2N-03 (4,65–5,45), T2N-02 (6,60–9,40) μπαίνουν στο 4,85–4,95, κάτω από τη βόρεια παρειά της δοκού· η νότια παρειά της (5,15) προεξέχει 0,20 στο καθιστικό με σοφίτα +2,50 από Τ.Δ. – η ψευδοροφή της βόρειας ζώνης του καθιστικού θα πάει περασιά. Τα δύο υποστυλώματα προεξέχουν 0,20 στις γωνίες (Δ: 1,40–1,70 × 4,95–5,15 γυμνό, παρειά 1,70 ≈ Τ3-07 1,705 · πυρήνα: 9,40–9,55 × 4,95–5,15, ο πεσσός Τ2-05 8,95–9,40 × 4,95–5,15 κλείνει τη γωνία πίσω από το ψυγείο). Παρειά καθιστικού 4,95 σε μία ευθεία από 1,70 ως 9,40: σαλόνι 1,705–6,45 × 4,95–9,125 = 4,75 × 4,175 ≈ 19,8 m² (μπροστά στο W0.01 3,50 και το W0.02), χωρίς κανέναν όγκο μέσα του· κουζίνα 6,45–9,55 × 4,175 με το WC στη ΒΑ γωνία της· σύνολο ≈ 30,3 m².

• WC ΣΤΗ ΒΑ ΓΩΝΙΑ ΤΗΣ ΖΩΝΗΣ ΚΑΘΙΣΤΙΚΟΥ-ΚΟΥΖΙΝΑΣ (R06, θέση αρχιτέκτονα – Γιάννης: «δούλεψε έτσι τώρα το WC όσο καλύτερα μπορείς»): WC 6,60–8,10 × 4,95–6,15 (1,50 × 1,20 = 1,8 m² – κέρδισε 0,20 βάθος από τη μετακίνηση του T2N-02). Πόρτα 0,70 γωνιακή στον δυτικό τοίχο (y 4,95–5,65), από το καθιστικό δίπλα στο άνοιγμα του χωλ, μεντεσές βόρεια 4,95, ανοίγει μέσα και διπλώνει στον βόρειο τοίχο (όπως A-10-GF)· παραστάδες ισοπαχείς 15/15 (Τ2A-02 βόρεια, Τ2A-03 0,60 νότια). Νιπτήρας 0,50 × 0,35 στον νότιο τοίχο Τ2-04 κοντά στην πόρτα (7,00–7,50, έξω από το τόξο της πόρτας), λεκάνη στον Τ7-02 ανατολικά στο βάθος (25, 8,10–8,35 × 4,95–6,25, άξονας y 5,45, λεκάνη 7,53–8,10) – χωριστά, χωρίς επικάλυψη. Στην εσοχή 8,35–8,95 (0,60) δίπλα στον Τ7-02 ΝΤΟΥΛΑΠΑ 0,60 × 0,65 με πόρτα προς την κουζίνα (αντικαθιστά τη ντουλάπα 1,10 του χωλ που χάθηκε – ο Γιάννης: ψυγείο και φούρνος ΔΕΝ χωράνε στην εσοχή). Όλοι οι τοίχοι του WC ανθυγρή γυψοσανίδα από μέσα (Τ7-02, Τ2-04, Τ2A-03, Τ2N-02 προς WC).

• ΒΟΡΕΙΑ ΖΩΝΗ (R06 – Γιάννης: «μίκρυνε λίγο το μπάνιο για να έχω χωλ · τον Τ2-01 τον φέρνεις περασιά με του λουτρού και γυρνάς την πόρτα δωματίου σε αυτόν · το πλυντήριο βγάλ' το πάλι στο χωλ»): ΛΟΥΤΡΟ 1,65 × 2,25 (4,80–6,45 × 0,80–3,05 ≈ 3,7 m², νότιος τοίχος στο 3,05–3,15)· ντους 1,65 × 0,80 βόρεια με γυαλί 0,70 στο y 1,60, λεκάνη στον Τ7-01 (y 2,00), πάγκος 0,50 ανατολικά 1,75–3,05 (1,30), πόρτα 0,70 στο 4,80–5,50 (μεντεσές 5,50). ΧΩΛ 1,80 × 1,00 (4,65–6,45 × 3,15–4,15 ≈ 1,8 m²): δυτικά πόρτα Υπν.1 (y 3,15–3,95, στον Τ2-01), βόρεια πόρτα λουτρού (4,80–5,50), ανατολικά πόρτα Υπν.2 (y 3,15–3,95, στον Τ2A), νότια εσοχή 0,70 (y 4,15–4,85): πλυντήριο 0,60 (4,65–5,25) + ξυλουργικό ράφια 0,20 (5,25–5,45, κανένα κενό), Τ2N-04 επιστροφή 5,45–5,55, άνοιγμα προς καθιστικό 5,55–6,45 (0,90, διάδρομος 0,80 ως την παρειά 4,95). Τοίχοι που βλέπουν σε ντουλάπα / πλυντήριο: 1 φύλλο (Τ2N-01…04).

• ΚΟΥΖΙΝΑ ΜΕ ΝΗΣΙΔΑ-ΤΡΑΠΕΖΑΡΙΑ (R06 – Γιάννης: «κενό νησίδα–κουζίνα τουλάχιστον 1,10, νησίδα 1,80 και κάτω, βάλε τον καναπέ · το ψυγείο και ο φούρνος να μην μπαίνουν στην εσοχή»): ζώνη 6,45–9,55 × 4,95–9,125. Στη γραμμή του πάγκου (x 8,95–9,55) από βορρά: ψυγείο 0,80 × 0,60 (5,15–5,95, κάτω από τον πεσσό Τ2-05), στήλη φούρνου 0,60 (5,95–6,55), πάγκος 0,60 × 2,55 (6,55–9,10): νεροχύτης 0,80, πλυντήριο πιάτων 0,60, πάγκος 0,25, εστίες 0,60 (8,20–8,80, απορροφητήρας στον Τ6-01), πάγκος 0,30. ΝΗΣΙΔΑ-ΧΕΡΣΟΝΗΣΟΣ 0,90 × 1,80 (x 6,95–7,85, y 6,25–8,05) από τον νότιο τοίχο του WC προς τα νότια: διάδρομος εργασίας 1,10 (7,85–8,95), ανοιχτός προς νότο (1,075 ως τον τοίχο), 3 θέσεις δυτικά (βήμα 0,60) = η νησίδα είναι και η τραπεζαρία. Σαλόνι: καναπές 2,70 × 0,90 στον βόρειο τοίχο (1,80–4,50 × 5,05–5,95) απέναντι από την TV, πολυθρόνα και τραπεζάκι του EPIPLA. Η τραπεζαρία + 6 καρέκλες του EPIPLA καταργείται· ύψος νησίδας / θέση συσκευών τελικά από τον μελετητή κουζίνας. Πίσω από τον πάγκο χωρίς επένδυση (Τ6-01 γυψοσανίδα, N υποστύλωμα γυμνό)· η Τ3-10 μόνο στην παραστάδα του W0.03 (8,70–8,80).

• Τ6-01 ΣΤΟ 9,55–9,70 (R06 – Γιάννης: «δες καλύτερα τον τοίχο Τ6-01, τον έχεις βάλει σε λάθος θέση»): ο αρχιτέκτονας έχει τοίχο 30 στο 9,40–9,70· ο Τ6 15 cm (R01) είχε μπει στο 9,40–9,55 με σταθερή την παρειά του διαμερίσματος και άφηνε στο lobby δύο δόντια 0,15 (υποστύλωμα πυρήνα 9,70 στο 3,00–5,15, τοίχος 9,55, N υποστύλωμα 9,70 στο 9,10–9,45). Τώρα στο 9,55–9,70: η παρειά του lobby 9,70 είναι μία ευθεία από το φρεάτιο ως την είσοδο, και η παρειά του καθιστικού 9,55 είναι επίσης ευθεία (το υποστύλωμα πυρήνα τελειώνει στο 5,15 = γραμμή του βόρειου τοίχου, το N υποστύλωμα από 9,10 μέσα στον νότιο τοίχο). Το διαμέρισμα κερδίζει 0,15 (πάγκος κουζίνας 8,95–9,55).

• Υπν.1 (R06 – «περασιά ο Τ2-01 με του λουτρού, η πόρτα πάνω του, άρα μεγαλώνει η ντουλάπα»): ορθογώνιο 1,125–4,55 × 0,805–4,85 (3,425 × 4,045 ≈ 13,9 m² μικτά, ≈ 10,2 m² ελεύθερα + ντουλάπες 3,7 m²). Ο Τ2-01 (4,55–4,65 × 3,95–4,95) είναι περασιά με τον Τ7-01 (παρειά Υπν.1 4,55 ενιαία από 0,805 ως 4,85)· πάνω του η πόρτα 0,80 από το χωλ (y 3,15–3,95, βόρεια παραστάδα ο Τ2-02, μεντεσές βόρεια 3,15, ανοίγει μέσα και διπλώνει στον Τ7-01 στο y 2,35–3,15). Ντουλάπες 0,60 χωνευτές, 6,0 m: ΔΥΤΙΚΗ 1,05–1,70 × 3,25–4,85 (1,60, βάθος 0,65 από το γυμνό τούβλο ως την παρειά 1,70 του Δ υποστυλώματος), ΝΟΤΙΑ 1,70–4,55 × 4,25–4,85 (2,85, από το υποστύλωμα ως τον Τ2-01), ΑΝΑΤΟΛΙΚΗ 3,95–4,55 × 0,805–2,35 (1,55 στον Τ7-01, ως το ανοιχτό φύλλο της πόρτας). Κρεβάτι 1,60 × 2,00 με κεφαλάρι στη δυτική επένδυση (στον βόρειο τοίχο είναι το W0.08), y 1,20–2,80, κομοδίνα 0,45 × 0,395 / 0,45 × 0,45· ελεύθερη λωρίδα 1,45 ανάμεσα στο κρεβάτι και τη νότια ντουλάπα. Η Τ3-06 ως 3,25 (πίσω από τη δυτική ντουλάπα γυμνό τούβλο).

• Υπν.2 (6,60–9,375 × 0,805–4,25 ≈ 9,6 m²): ντουλάπα 6,60–9,40 × 4,25–4,85 (2,80), πόρτα 0,80 από το χωλ στο y 3,15–3,95 (Τ2A-01 / Τ2A-02, μεντεσές βόρεια 3,15, διπλώνει στον Τ2A-01), W0.06 1,00×2,40 μπαλκονόπορτα προς τη ΒΑ βεράντα. Τ9-02 στο υποστύλωμα πυρήνα 3,00–4,25 περασιά με την Τ3-05. W0.07 0,60×0,90 μέσα στο τοιχείο Κ2 (x 5,50–6,10): κενό στον ξυλότυπο από τώρα (ποδιά +1,50).


• ΚΑΘΙΣΤΙΚΟ: δυτικός τοίχος Τ1-07 1,40–1,65 + Τ3-07 ως 1,705 περασιά με το ΝΔ τοιχείο (1,40) και την ανατολική παρειά του Δ υποστυλώματος (1,70)· W0.01 3,50×2,40 στο 5,65–9,15· Τ9-03 στο ΝΔ τοιχείο (παρειά 9,125) περασιά με Τ3-08 / Τ3-09. Καναπές, πολυθρόνα (0,45 δυτικότερα), τραπεζάκι, έπιπλο TV από το EPIPLA.

• ΠΥΡΗΝΑΣ: Τ5-01 10 cm σε όλο το μήκος 9,70–13,35 (A-10-GF) με επιστροφή Τ5-02 στο φρεάτιο· shaft Η/Μ εκτός Σ.Δ. στο y 2,85–3,15 × 9,70–11,05 (βάθος 0,30 όπως B1 – ο αρχιτέκτονας δείχνει μέτωπο 25 στο 3,00–3,25). Μέτωπο ανελκυστήρα Τ10-01/Τ10-02 25 cm, πόρτα 0,90 στο y 3,60–4,50. Κύκλος περιστροφής ΑΜΕΑ R0,75 (1,50) στο 9,70–11,20. Σκάλα 16 ριχτιών όπως B1. ΕΙΣΟΔΟΣ ΚΤΙΡΙΟΥ (R06, A-50-02 06/11): ενιαίο κούφωμα αλουμινίου 2,45 στο 9,70–12,15 = πόρτα Θ0.04 1,20×2,40 (9,70–10,90, μεντεσές δυτικά, ανοίγει μέσα) + σταθερό W0.04 1,25×2,40 (10,90–12,15)· ο πεσσός τούβλου 0,10 του R01 καταργείται (παραστάδα = N υποστύλωμα 9,70). Καμία πόρτα διαμερίσματος προς το lobby.

• ΚΟΥΦΩΜΑΤΑ (A-50-02 06/11/2026 + A-10-GF R01): W0.08 1,60×2,40 (2,00–3,60) · W0.07 0,60×0,90 (ποδιά 1,50) · W0.06 1,00×2,40 (1,45–2,45) · W0.01 3,50×2,40 δίφυλλο επάλληλο (5,65–9,15) · W0.02 1,45 σταθερό (3,50–5,00 – ο πίνακας λέει 145, η κάτοψη 1,50) · Θ0.03 πόρτα ΙΣ1 1,10×2,40 (5,00–6,10 – ο πίνακας 110, η ετικέτα της κάτοψης R01 1,20: ΝΑ ΔΙΕΥΚΡΙΝΙΣΤΕΙ) · W0.03 2,40 = 1,50 σταθερό + 0,90 ανοιγοανακλινόμενο (6,30–8,70) · Θ0.04 1,20 + W0.04 1,25 · W0.05 0,70×1,35. Πεσσοί 0,10 (3,40–3,50), 0,20 (6,10–6,30), 0,30 (8,70–9,00) όπως ο αρχιτέκτονας – ΠΡΟΣ ΑΠΟΦΑΣΗ αν ο 0,10 ενσωματωθεί στο κούφωμα. Τ3 και στις δύο παραστάδες.

• ΘΕΡΜΟΠΡΟΣΟΨΗ: 10 cm στο διαμέρισμα, 5 cm στον πυρήνα / είσοδο κτιρίου (Τ5-01, φρεάτιο, Τ1-12, Τ1-11). ΥΨΟΣ ισογείου 3,00 (πλάκα οροφής +3,65 κατά Σ3) – επιφάνειες Τ-03 με Η = 3,00.

ΕΡΓΟ	ΘΕΜΑ ΣΧΕΔΙΟΥ	ΒΑΣΗ	ΑΡ. ΣΧΕΔΙΟΥ
ΠΕΝΤΑΟΡΟΦΟ ΚΤΗΡΙΟ ΚΑΤΟΙΚΙΩΝ – ΑΡΓΥΡΟΥΠΟΛΗ Κωνσταντινουπόλεως 12 & Αγ. Βαρβάρας · Ο.Τ. 103-15 Εργοδότης: INTERKAT Α.Ε. · Κατασκευή: ARKAD Ι.Κ.Ε.	**ΠΡΟΜΕΤΡΗΣΗ ΤΟΙΧΟΠΟΙΙΩΝ – ΙΣΟΓΕΙΟΥ** Τετραγωνικά ανά τυπολογία τοίχου · θερμοπρόσοψη 10 / 5 cm ΙΣΟΓΕΙΟ – ΙΣ1	Βάση: κάτοψη τοιχοποιιών Τ-01 · είδη Τ-02	**Τ-03** — · **A3** 06/11/2026 · R06

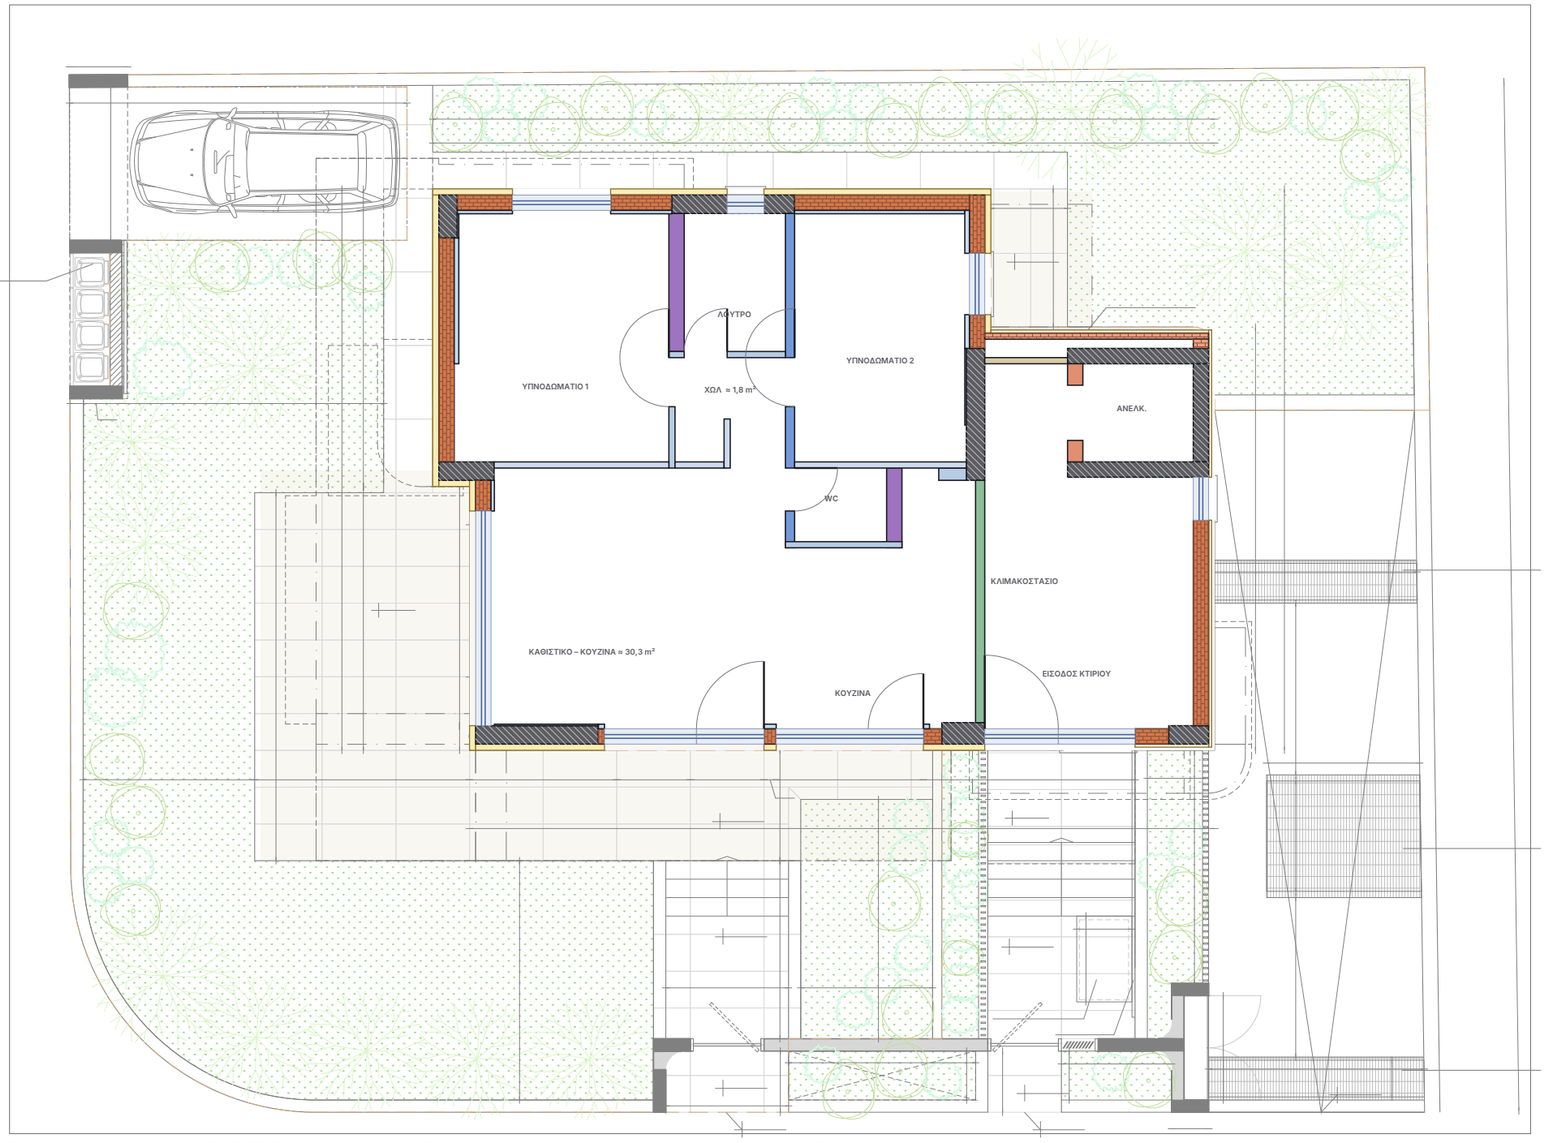

Περιβάλλων χώρος: γεωμετρία A-10-GF (EDGE, μελέτη εφαρμογής 23/07/2026) 1:100, αχνά, χωρίς κείμενα / διαστάσεις · τοιχοποιίες από το T-01 R06 · συντεταγμένες μοντέλου σε m

B

ΠΕΡΙΒΑΛΛΩΝ ΧΩΡΟΣ ΙΣΟΓΕΙΟΥ – όπως τον έχει ο αρχιτέκτονας (A-10-GF)

Το φύλλο δείχνει το οικόπεδο ολόκληρο με τον κήπο, τις βεράντες, τις εισόδους και τη ράμπα όπως τα έχει ο αρχιτέκτονας στο A-10-GF (μόνο η γεωμετρία, χωρίς τα κείμενά του), για να φαίνεται πώς δένουν οι τοιχοποιίες του ισογείου με τον περιβάλλοντα χώρο. Δεν είναι σχέδιο κατασκευής κήπου: για διαστάσεις, στάθμες και φυτεύσεις ισχύουν τα A-10-GF / A-14-GF και η μελέτη περιβάλλοντος χώρου.

ΚΗΠΟΣ ΙΣ1
Χώρος αποκλειστικής χρήσης ΙΣ1 κατοικίας 182,08 m² (σημεία 1…23 του A-10-GF): δυτικά και νότια του κτιρίου, βεράντα ισογείου δυτικά +0,40 (κλίση 1 %) και νότια +0,45 με σκαλιά 1–4 προς −0,30 · προβολές εξώστη / έρκερ με διακεκομμένη.

ΕΙΣΟΔΟΣ ΙΣ1
Από τη νότια περίφραξη: πύλη Θ 1,00/2,20 (x ≈ 5,2–6,2), σκαλιά −0,30 → +0,45, βεράντα, πόρτα Θ0.03 1,10×2,40 (5,00–6,10).

ΣΤΑΘΜΕΥΣΗ
Θ.Σ.Ι.1 13,75 m² στη ΒΔ γωνία του οικοπέδου (θέση στάθμευσης ισογείου), πλάτος 2,50 · μήκος 5,50.

ΦΥΤΕΜΕΝΟΙ ΧΩΡΟΙ
Φ.Χ.1 37,69 m² (βόρεια) · Φ.Χ.2 68,46 (νοτιοδυτικά) · Φ.Χ.3 8,39 · Φ.Χ.4 2,82 · Φ.Χ.5 3,76 · Φ.Χ.6 1,42 · Φ.Χ.7 2,44 m².

ΕΙΣΟΔΟΣ ΚΤΙΡΙΟΥ
Νότια: πύλη πεζών Θ 1,00/2,20 (x ≈ 9,85–10,85) στο −0,45, σκάλα 5 ριχτιών 2,40 (x 9,75–12,15) ως το πλατύσκαλο +0,45 (9,50–12,95 × 9,45–10,25), αναδιπλούμενη πλατφόρμα αναβατορίου ΑΜΕΑ 0,90×1,40 με οδηγό x 8,85–9,75, πόρτα αλουμινίου 1,00×2,40 + σταθερό W0.04 1,20 στο lobby (24,55 m²).

ΒΑ ΒΕΡΑΝΤΑ
Βεράντα ισογείου +0,45, 9,80–11,45 × 0,45–2,70, από την μπαλκονόπορτα W0.06 του Υπν.2 · ανατολικά της φυτεμένος χώρος.

ΟΧΗΜΑΤΑ / ΥΠΟΣΤΑΘΜΟΣ
Ράμπα Ι.Χ. κλίσης 16,12 % στη ΝΑ γωνία (είσοδος – έξοδος οχημάτων, −0,55), μετρητές ΔΕΔΔΗΕ, εσχάρες υποσταθμού: εξαερισμού Ι-Κ-Λ-Μ 3,40×0,60 = 2,04 m² (ανατολικά του lobby) και Ρ-Σ-Τ-Υ 3,52×0,60 = 2,11 m², καταπακτής Ν-Ξ-Ο-Π 2,80×1,80 = 5,02 m² (βλ. A-30-01).

ΕΡΓΟ	ΘΕΜΑ ΣΧΕΔΙΟΥ	ΒΑΣΗ	ΑΡ. ΣΧΕΔΙΟΥ
ΠΕΝΤΑΟΡΟΦΟ ΚΤΗΡΙΟ ΚΑΤΟΙΚΙΩΝ – ΑΡΓΥΡΟΥΠΟΛΗ Κωνσταντινουπόλεως 12 & Αγ. Βαρβάρας · Ο.Τ. 103-15 Εργοδότης: INTERKAT Α.Ε. · Κατασκευή: ARKAD Ι.Κ.Ε.	**ΠΕΡΙΒΑΛΛΩΝ ΧΩΡΟΣ – ΙΣΟΓΕΙΟ** Κήπος ΙΣ1 · βεράντες · είσοδοι · ράμπα κατά A-10-GF ΙΣΟΓΕΙΟ – ΙΣ1	Βάση: γεωμετρία περιβάλλοντος χώρου A-10-GF · τοιχοποιίες T-01	**T-04** **Κλίμακα 1:100 · A3** 06/11/2026 · R06