ΑΛΛΑΓΕΣ R15 / R16 (05/11/2026)

- Ντουλάπες χωνευτές: δωματίων 0,60 · πλυντηρίου 0,70
- Τ1-05 ως 1,38 (+0,03 περιθώριο) · Τ3-06 μένει (ισοπαχείς λαμπάδες) · W2.06 → 1,38–2,38
- Υπν.1: χωρίς κουτί – ξυλουργικό συνέχεια ντουλάπας ως τον β. τοίχο
- Τ2-05 → Τ2Ν-02 (1 φύλλο προς ντουλάπα) · διάδρομος χωλ 1,00
- Λουτρά: πάγκος 0,50 · λεκάνη · γυάλινο διαχωριστικό 0,70 · ντους 0,70–1,00
- Αλουμίνια στη μέση του τοίχου: Τ3 και στις δύο παραστάδες
- Πόρτες: ανοίγουν μέσα στον χώρο (Υπν.1, λουτρά, Υπν.2)
- W2.07 μέσα στο τοιχείο Κ2: κενό 0,60×0,90 στον ξυλότυπο (ποδιά +1,50)
- Αλυσίδες διαστάσεων μέσα στους χώρους · φύλλο χάραξης Τ-01Α

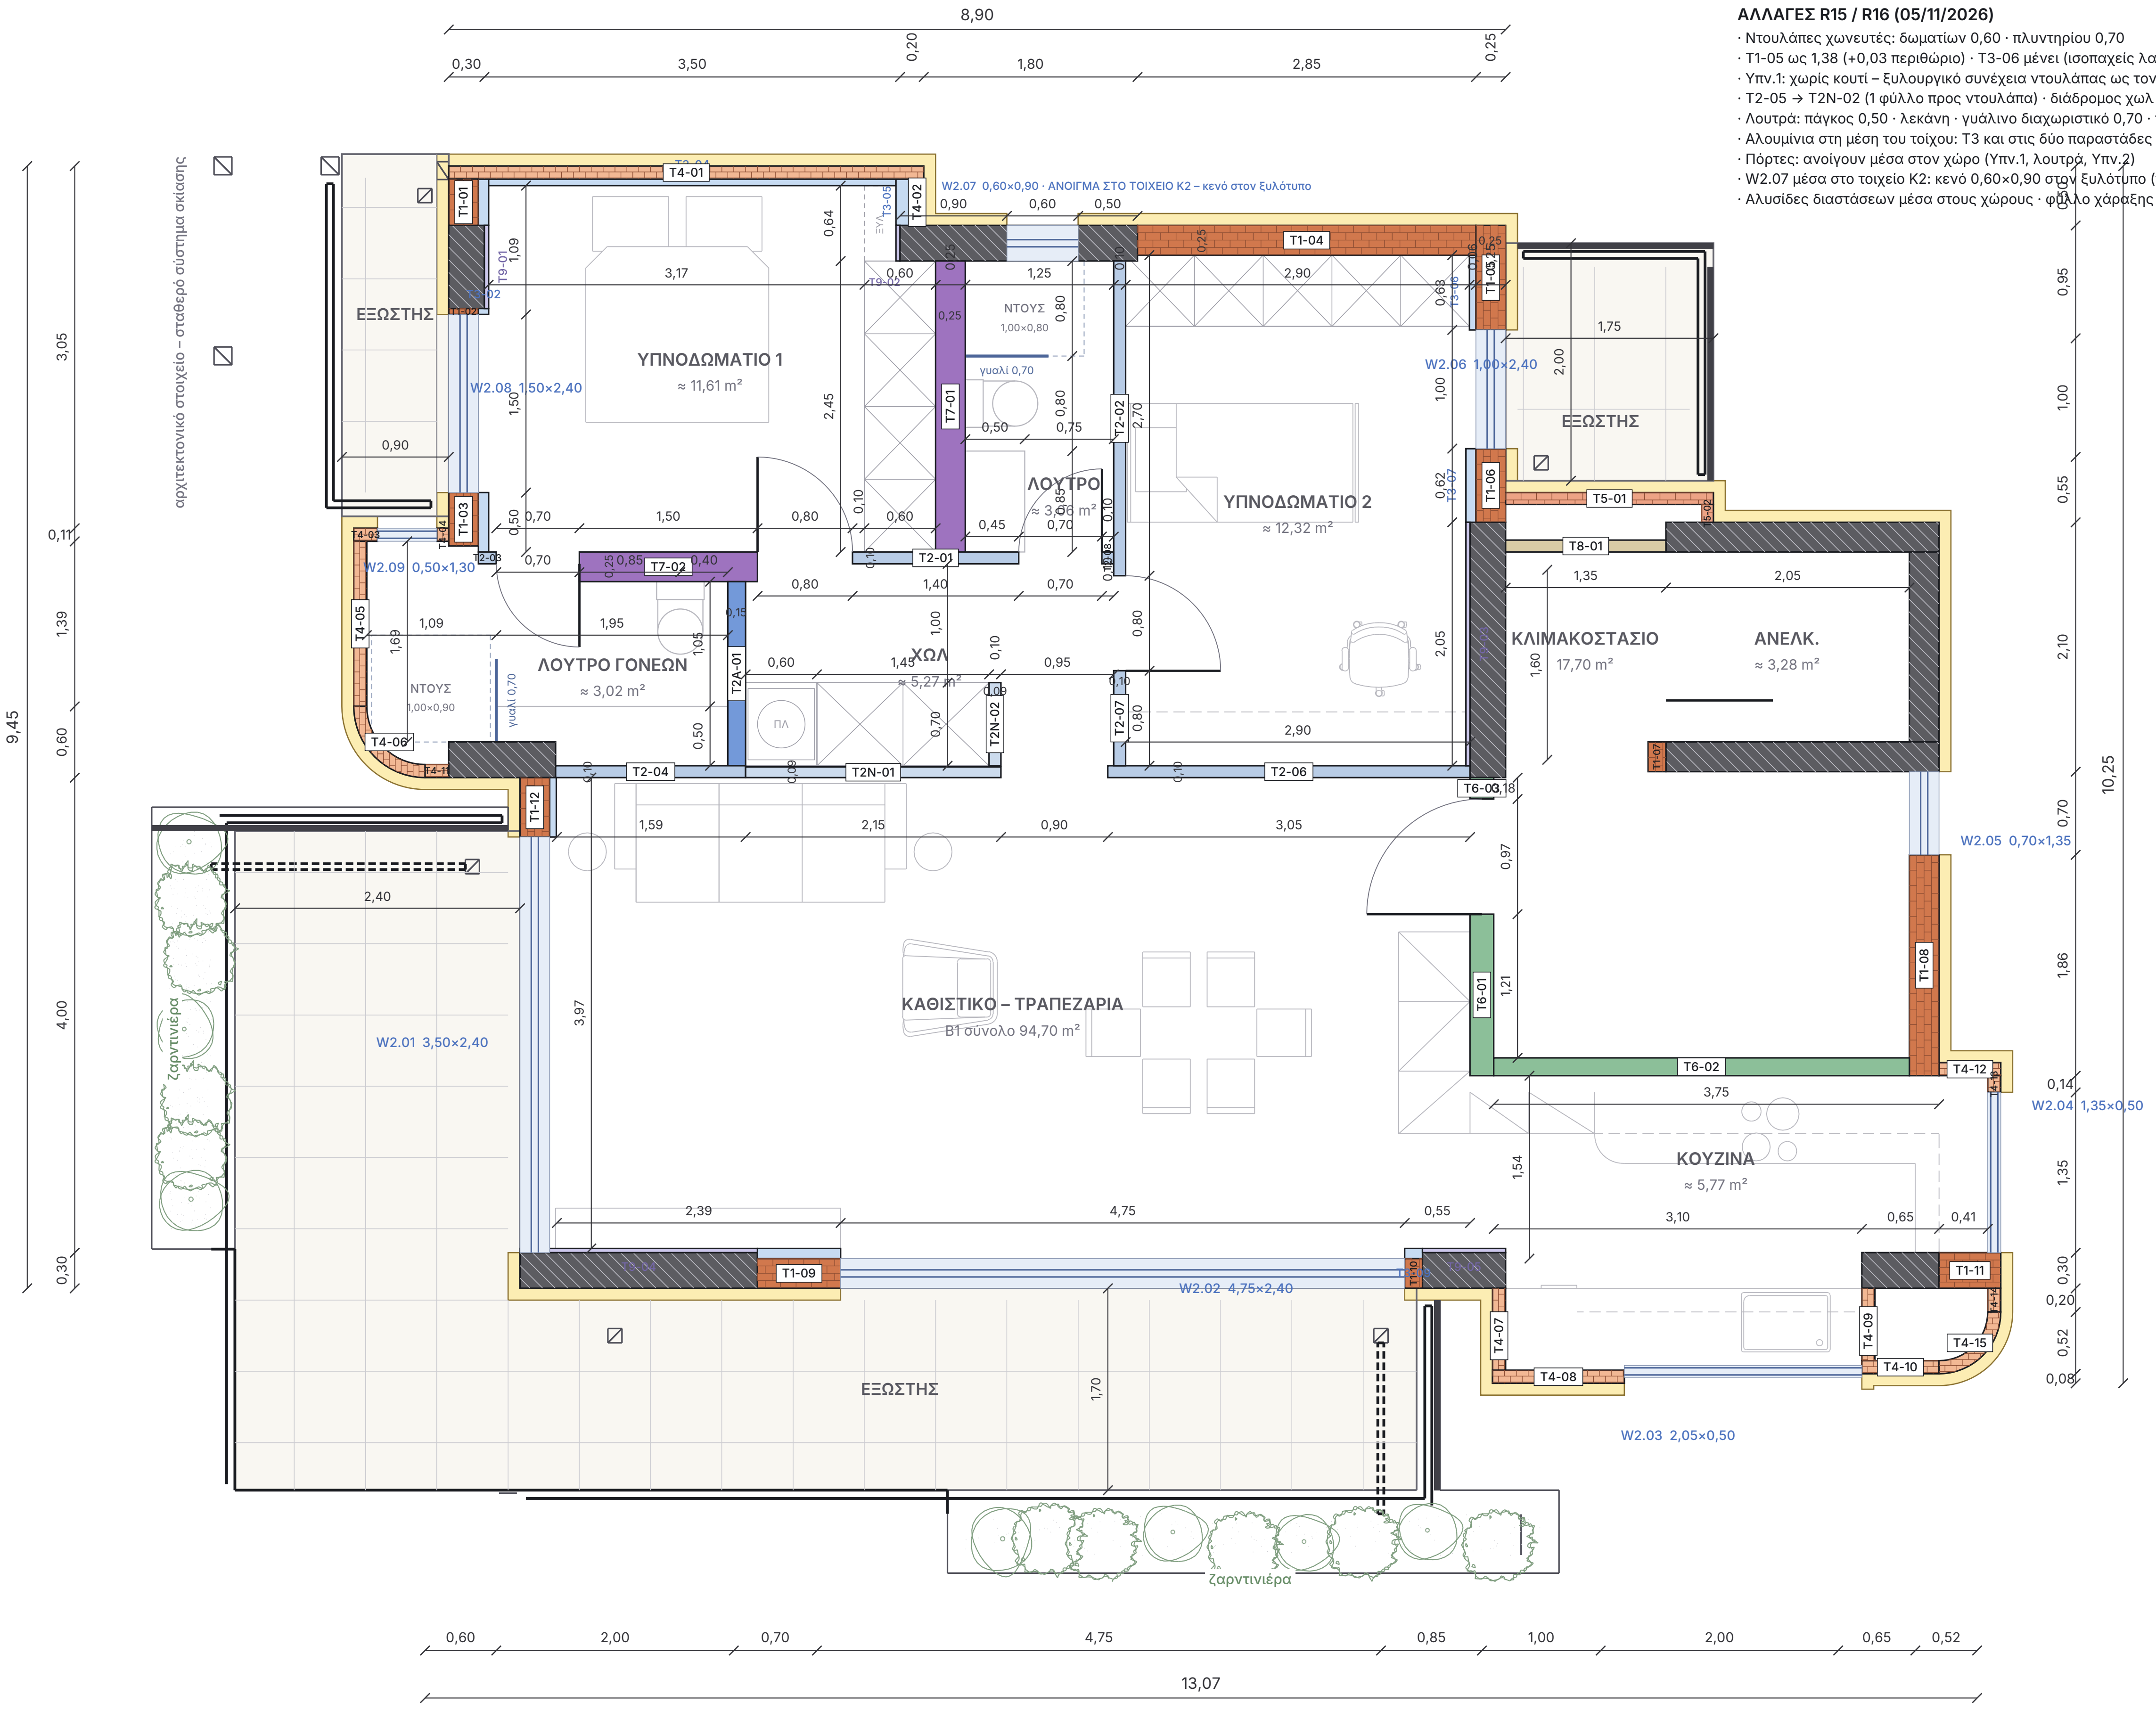
Β
8,90
0,30
3,50
0,20
1,80
2,85
0,25
ΕΞΩΣΤΗΣ
αρχιτεκτονικό στοιχείο – σταθερό σύστημα σκίασης
ΥΠΝΟΔΩΜΑΤΙΟ 1
≈ 11,61 m²
W2.08 1,50×2,40
W2.07 0,60×0,90 · ΑΝΟΙΓΜΑ ΣΤΟ ΤΟΙΧΕΙΟ Κ2 – κενό στον ξυλότυπο
Τ4-01
Τ1-01
Τ9-01
Τ3-02
Τ1-02
Τ3-05
Τ4-02
Τ9-02
Τ7-01
ΝΤΟΥΣ
1,00×0,80
γυαλί 0,70
ΛΟΥΤΡΟ
≈ 3,06 m²
Τ2-01
Τ2-02
Τ1-04
Τ1-05
Τ3-06
W2.06 1,00×2,40
ΕΞΩΣΤΗΣ
ΥΠΝΟΔΩΜΑΤΙΟ 2
≈ 12,32 m²
Τ1-06
Τ3-07
Τ5-01
Τ5-02
Τ8-01
Τ9-03
ΚΛΙΜΑΚΟΣΤΑΣΙΟ
17,70 m²
ΑΝΕΛΚ.
≈ 3,28 m²
Τ1-07
Τ1-03
Τ4-03
Τ4-04
Τ2-03
W2.09 0,50×1,30
Τ7-02
Τ4-05
ΝΤΟΥΣ
1,00×0,90
γυαλί 0,70
ΛΟΥΤΡΟ ΓΟΝΕΩΝ
≈ 3,02 m²
Τ2Α-01
ΠΛ
ΧΩΛ
≈ 5,27 m²
Τ2Ν-02
Τ2-07
Τ4-06
Τ4-11
Τ2-04
Τ2Ν-01
Τ2-06
Τ6-03
Τ1-12
W2.05 0,70×1,35
ΚΑΘΙΣΤΙΚΟ – ΤΡΑΠΕΖΑΡΙΑ
Β1 σύνολο 94,70 m²
W2.01 3,50×2,40
Ζαρντινιέρα
Τ6-01
Τ6-02
Τ1-08
Τ4-12
Τ4-13
W2.04 1,35×0,50
ΚΟΥΖΙΝΑ
≈ 5,77 m²
Τ1-09
W2.02 4,75×2,40
Τ1-10
Τ3-09
Τ9-05
Τ4-07
Τ4-08
Τ4-09
Τ4-10
Τ1-11
Τ4-14
Τ4-15
W2.03 2,05×0,50
ΕΞΩΣΤΗΣ
Ζαρντινιέρα
9,45
3,05
0,11
1,39
0,60
4,00
0,30
10,25
0,95
1,00
0,55
2,10
0,70
1,86
0,14
1,35
0,30
0,20
0,52
0,08
0,60
2,00
0,70
4,75
0,85
1,00
2,00
0,65
0,52
13,07

ΕΡΓΟ

ΠΕΝΤΑΟΡΟΦΟ ΚΤΗΡΙΟ ΚΑΤΟΙΚΙΩΝ – ΑΡΓΥΡΟΥΠΟΛΗ
Κωνσταντινουπόλεως 12 & Αγ. Βαρβάρας · Ο.Τ. 103-15
Εργοδότης: INTERKAT Α.Ε. · Κατασκευή: ARKAD Ι.Κ.Ε.

ΘΕΜΑ ΣΧΕΔΙΟΥ

ΚΑΤΟΨΗ ΤΟΙΧΟΠΟΙΙΩΝ – Β΄ ΟΡΟΦΟΣ

Είδη τοιχοποιιών · διαστάσεις χάραξης · κουφώματα · εξώστες
Β΄ ΟΡΟΦΟΣ – Β1

ΒΑΣΗ

Βάση: κάτοψη Α-10-2F (μελέτη εφαρμογής) · ξυλότυποι Σ · R14 + αλλαγές 05/11

ΑΡ. ΣΧΕΔΙΟΥ

Τ-01

Κλίμακα 1:60 · Α3
05/11/2026 · R16

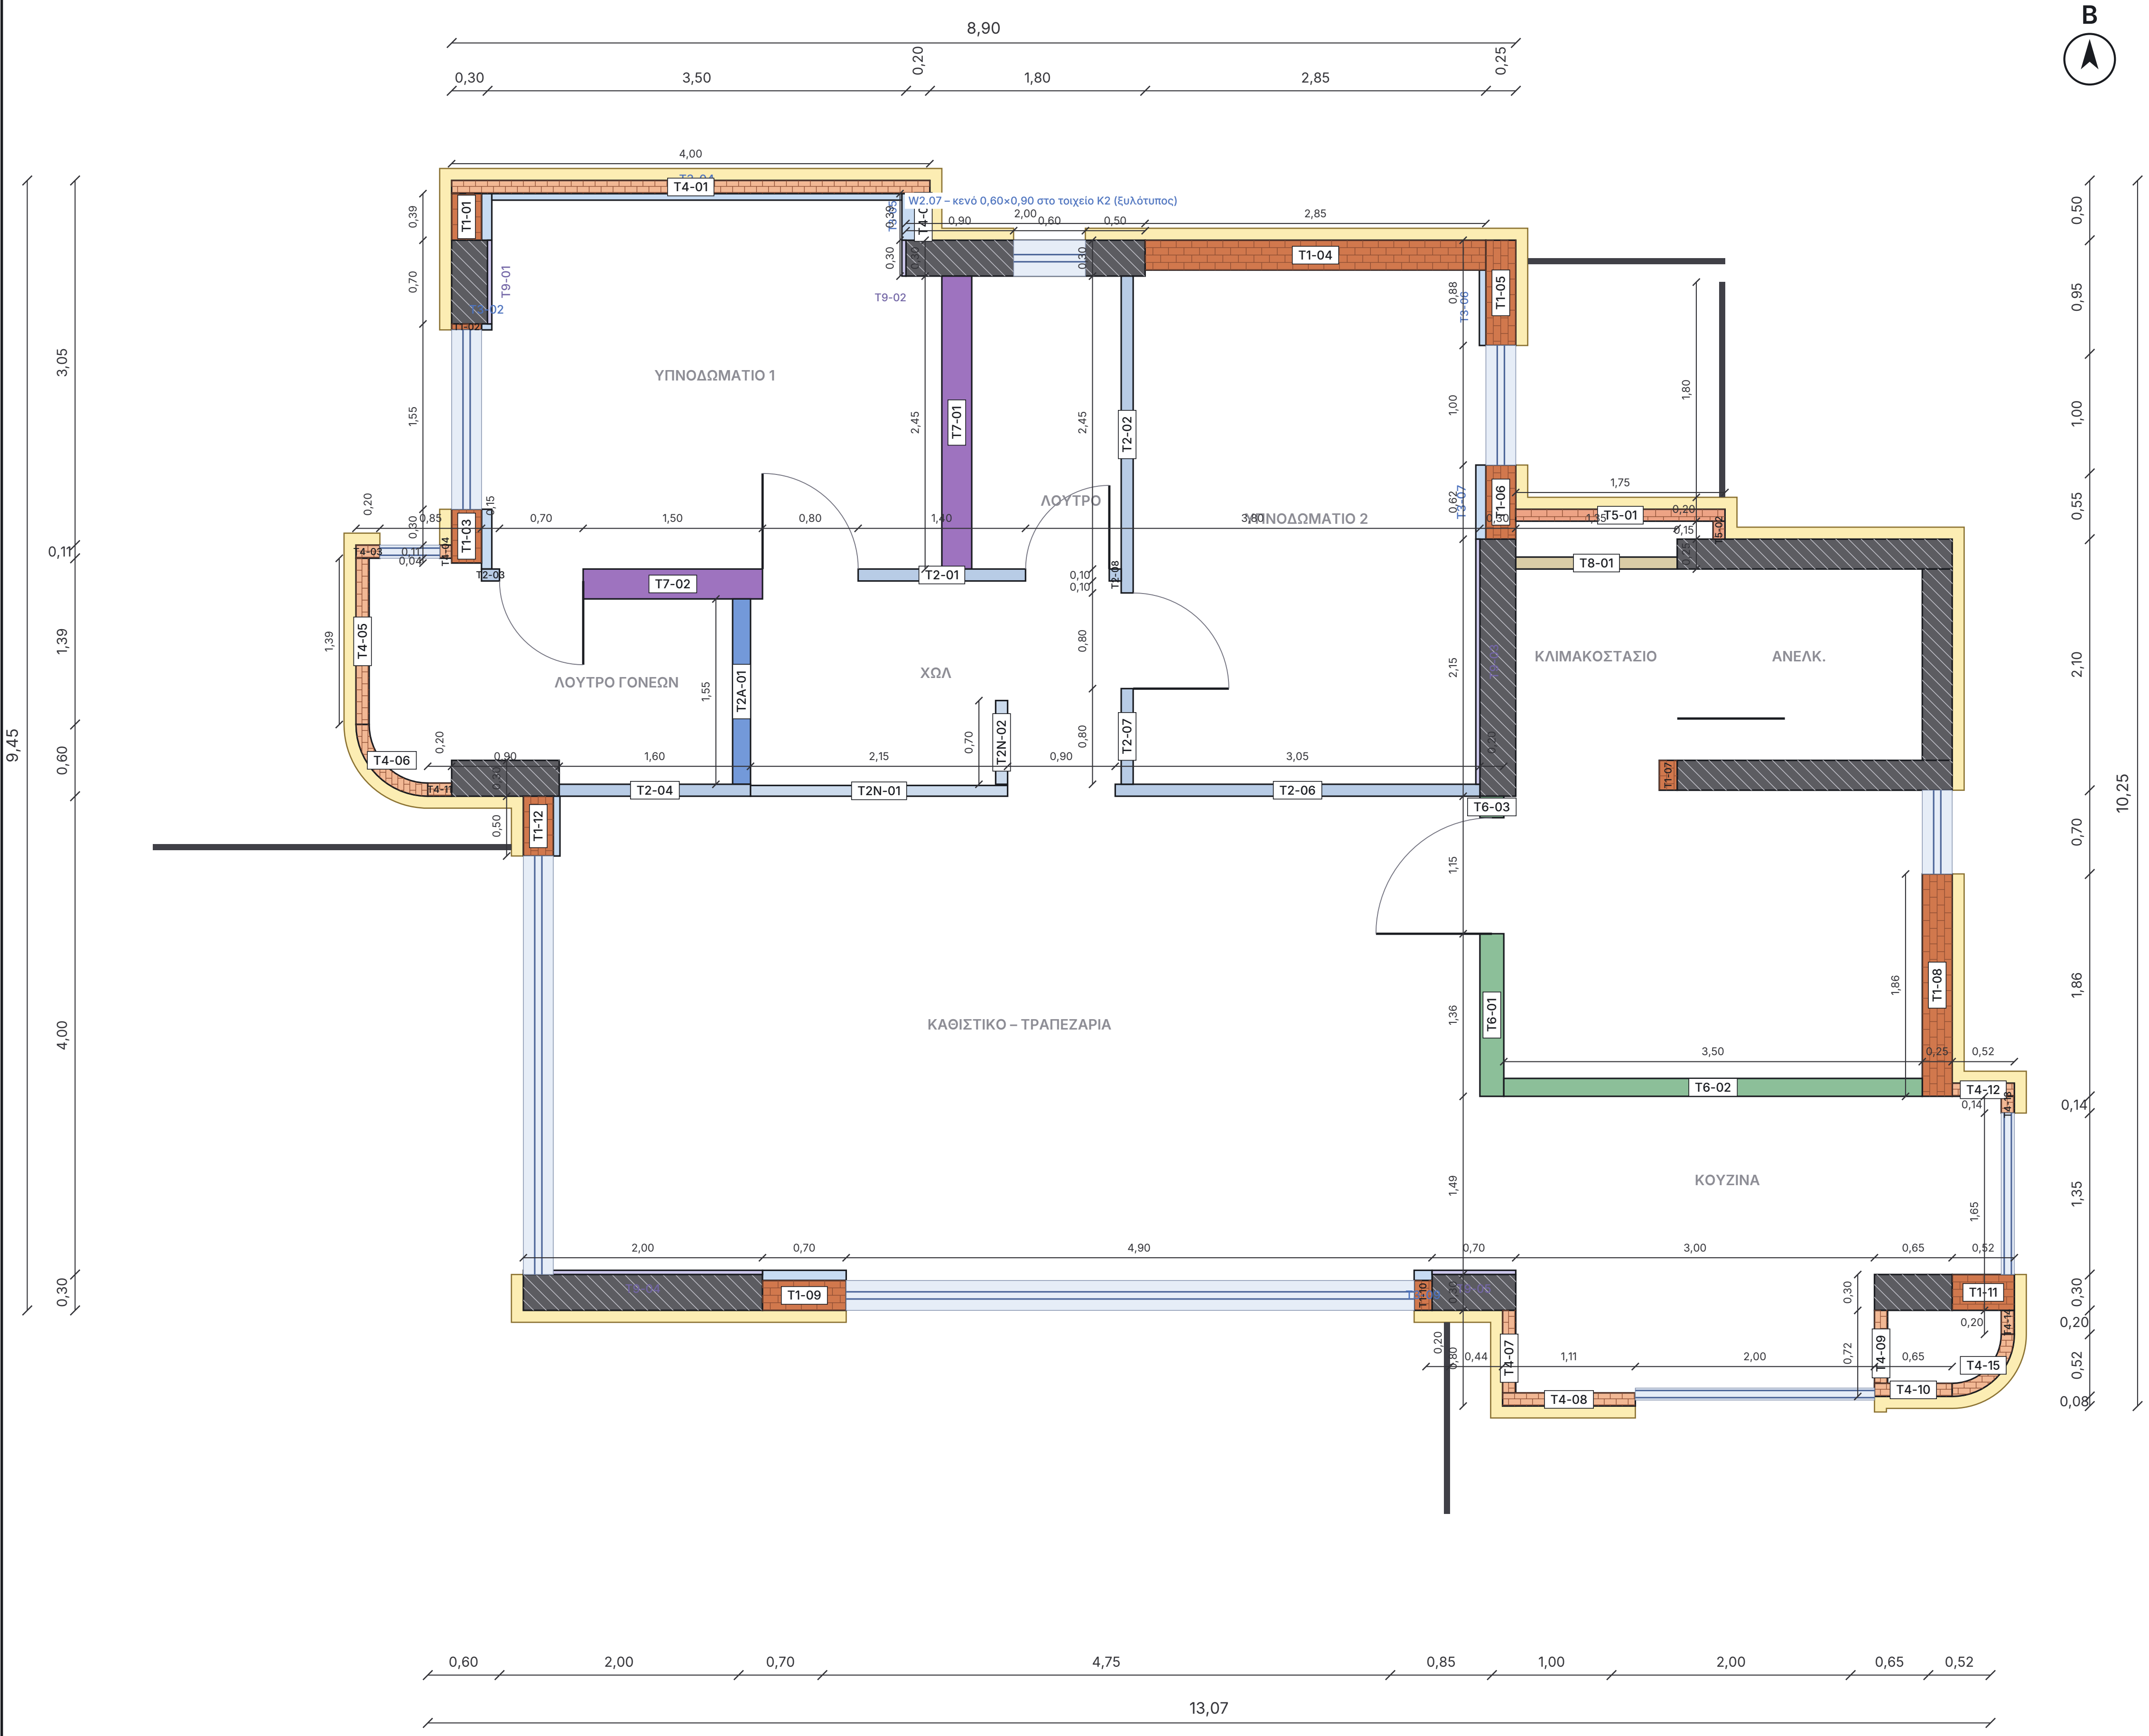
B
8,90
0,30
3,50
0,20
1,80
2,85
0,25
4,00
T4-01
T1-01
W2.07 – κενό 0,60×0,90 στο τοιχείο K2 (ξυλότυπος)
T9-01
T9-02
T1-04
T1-05
T7-01
T2-02
ΥΠΝΟΔΩΜΑΤΙΟ 1
ΛΟΥΤΡΟ
ΥΠΝΟΔΩΜΑΤΙΟ 2
T1-06
T5-01
T8-01
T1-03
T2-03
T2-01
T7-02
T4-05
ΛΟΥΤΡΟ ΓΟΝΕΩΝ
ΧΩΛ
T2A-01
T2N-02
T2-07
ΚΛΙΜΑΚΟΣΤΑΣΙΟ
ΑΝΕΛΚ.
T1-07
T4-06
T2-04
T2N-01
T2-06
T6-03
T1-12
ΚΑΘΙΣΤΙΚΟ – ΤΡΑΠΕΖΑΡΙΑ
T6-01
T1-08
T6-02
T4-12
ΚΟΥΖΙΝΑ
T1-09
T1-11
T4-07
T4-08
T4-09
T4-10
T4-15
0,60
2,00
0,70
4,75
0,85
1,00
2,00
0,65
0,52
13,07
3,05
0,11
1,39
0,60
4,00
0,30
9,45
0,50
0,95
1,00
0,55
2,10
0,70
1,86
0,14
1,35
0,30
0,20
0,52
0,08
10,25

ΣΥΝΤΕΤΑΓΜΕΝΕΣ ΠΑΡΕΙΩΝ ΤΟΙΧΩΝ (m)

x από την εξωτ. Δ παρειά T4-05 (→ ανατολή) · y από την εξωτ. Β παρειά T4-01 (→ νότο) · χωρίς θερμοπρόσοψη
επενδύσεις T3 / T9 δεν χαράσσονται: ακολουθούν τον τοίχο / την κολόνα που ντύνουν

Τοίχος	πάχ.	x από	x έως	y από	y έως	μήκος
T1-01	25	0,80	1,05	0,11	0,50	0,39
T1-02	25	0,80	1,05	1,20	1,25	0,25
T1-03	25	0,80	1,05	2,75	3,20	0,45
T1-04	25	6,60	9,45	0,50	0,75	2,85
T1-05	25	9,45	9,70	0,50	1,38	0,88
T1-06	25	9,45	9,70	2,38	3,00	0,62
T1-07	25	10,90	11,05	4,85	5,10	0,25
T1-08	25	13,10	13,35	5,80	7,66	1,86
T1-09	25	3,40	4,10	9,20	9,45	0,70
T1-10	25	8,85	9,00	9,20	9,45	0,25
T1-11	25	13,35	13,87	9,15	9,45	0,52
T1-12	25	1,40	1,65	5,15	5,65	0,50
T4-01	11	0,80	4,80	-0,00	0,11	4,00
T4-02	11	4,69	4,80	0,11	0,50	0,39
T4-03	11	-0,00	0,20	3,05	3,16	0,20
T4-04	11	0,70	0,80	3,05	3,16	0,11
T4-05	11	-0,00	0,11	3,16	4,55	1,39
T4-06	11	-0,00	0,60	4,55	5,15	0,86*
T4-07	11	9,59	9,70	9,45	10,25	0,80
T4-08	11	9,59	10,70	10,14	10,25	1,11
T4-09	11	12,70	12,81	9,45	10,17	0,72
T4-10	11	12,70	13,35	10,06	10,17	0,65
T4-11	11	0,60	0,80	5,04	5,15	0,20
T4-12	11	13,35	13,87	7,55	7,66	0,52
T4-13	11	13,76	13,87	7,66	7,80	0,14
T4-14	11	13,76	13,87	9,45	9,65	0,20
T4-15	11	13,35	13,87	9,65	10,17	0,73*
T5-01	10	9,70	11,45	2,75	2,85	1,75
T5-02	10	11,35	11,45	2,85	3,00	0,15
T2-01	10	4,20	5,60	3,25	3,35	1,40
T2-02	10	6,40	6,50	0,80	3,45	2,65
T2-03	10	1,05	1,20	3,25	3,35	0,15
T2-04	10	1,70	3,30	5,05	5,15	1,60
T2-06	10	6,35	9,40	5,05	5,15	3,05
T2-07	10	6,40	6,50	4,25	5,05	0,80
T2-08	10	6,30	6,40	3,25	3,35	0,10
T2N-01	8,8	3,30	5,45	5,06	5,15	2,15
T2N-02	8,8	5,35	5,45	4,35	5,05	0,70
T2A-01	15	3,15	3,30	3,50	5,05	1,55
T7-01	25	4,90	5,15	0,80	3,25	2,45
T7-02	25	1,90	3,40	3,25	3,50	1,50
T6-01	15	9,40	9,60	6,30	7,66	1,36
T6-02	15	9,60	13,10	7,51	7,66	3,50
T6-03	15	9,40	9,60	5,15	5,33	0,20
T8-01	10	9,70	11,05	3,15	3,25	1,35

* καμπύλο τμήμα (έρκερ): μήκος στον μέσο άξονα του τόξου · T6-01: δύο τμήματα (πόρτα εισόδου 5,33–6,30)
Οι αλυσίδες της κάτοψης δίνουν, σε κάθε γραμμή τοίχου, τα άκρα των τοίχων και τις παρειές των υποστυλωμάτων ώστε η χάραξη να γίνεται με μετροταινία από τα μπετά. Ανοχή ±1 cm.

ΕΡΓΟ

ΠΕΝΤΑΟΡΟΦΟ ΚΤΗΡΙΟ ΚΑΤΟΙΚΙΩΝ – ΑΡΓΥΡΟΥΠΟΛΗ
Κωνσταντινουπόλεως 12 & Αγ. Βαρβάρας · Ο.Τ. 103-15
Εργοδότης: INTERKAT A.E. · Κατασκευή: ARKAD I.K.E.

ΘΕΜΑ ΣΧΕΔΙΟΥ

ΧΑΡΑΞΗ ΤΟΙΧΟΠΟΙΙΩΝ – Β΄ ΟΡΟΦΟΣ

Αλυσίδες κατά μήκος κάθε γραμμής τοίχου · συντεταγμένες παρειών
Β΄ ΟΡΟΦΟΣ – Β1 · χωρίς έπιπλα

ΒΑΣΗ

Βάση: κάτοψη τοιχοποιιών Τ-01 · ξυλότυποι Σ (υποστυλώματα)

ΑΡ. ΣΧΕΔΙΟΥ

T-01A

Κλίμακα 1:60 · A3
05/11/2026 · R16

🟧 T1 Εξωτερική οπτοπλινθοδομή 1:4

πάχος 25 cm

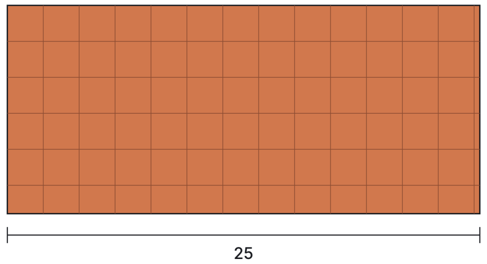

θερμομονωτικό τούβλο κάθετων οπών 25 cm · θερμοπρόσοψη 10 cm έξω · επένδυση T3 μέσα όπου σημειώνεται

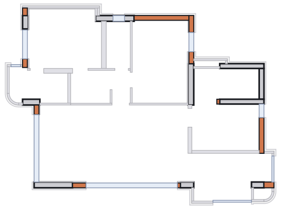

Τοίχοι: T1-01, T1-02, T1-03, T1-04, T1-05, T1-06, T1-07, T1-08, T1-09, T1-10, T1-11, T1-12

Μήκος 9,52 m · επιφάνεια ≈ 27,6 m²

🟧 T4 Έρκερ – απλή οπτοπλινθοδομή 1:4

πάχος 11 cm

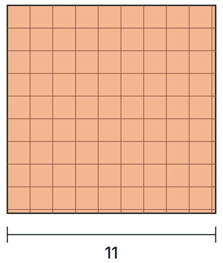

απλό τούβλο 6οπο 9 × 12 × 19 δρομικό ≈ 11 cm · σταθερή η εξωτερική παρειά · θερμοπρόσοψη 10 cm έξω

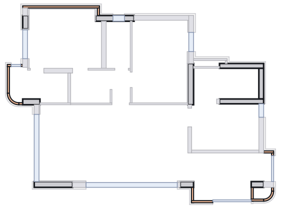

Τοίχοι: T4-01, T4-02, T4-03, T4-04, T4-05, T4-06, T4-07, T4-08, T4-09, T4-10, T4-11, T4-12, T4-13, T4-14, T4-15

Μήκος 12,02 m · επιφάνεια ≈ 34,8 m²

🟧 T5 Οπτοπλινθοδομή πυρήνα 1:4

πάχος 10 cm

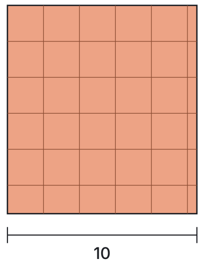

θερμομονωτικό τούβλο κάθετων οπών 10 cm · γύρω από τον πυρήνα (ανελκυστήρας – ηλεκτροστάσιο)

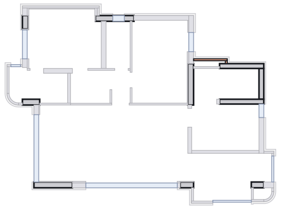

Τοίχοι: T5-01, T5-02

Μήκος 1,90 m · επιφάνεια ≈ 5,5 m²

🟦 T3 Επένδυση τοίχου 1:4

πάχος 5,5 cm

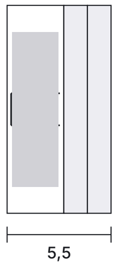

σκελετός 30 · 2 × γυψοσανίδα 12,5 · στις εσωτερικές παρειές των T1 – ΟΧΙ όπου πλακάκι ή ντουλάπα, ΟΧΙ στα έρκερ

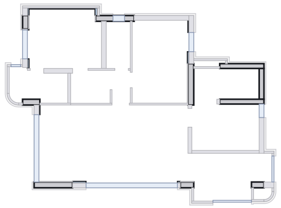

Τοίχοι: T3-01, T3-02, T3-03, T3-04, T3-05, T3-06, T3-07, T3-08, T3-09, T3-10

Μήκος 7,40 m · επιφάνεια ≈ 21,4 m²

🟪 T9 Επένδυση υποστυλώματος 1:4

πάχος 2,5 cm

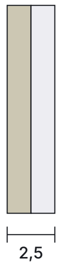

κόλλα + 1 × γυψοσανίδα 12,5 (ένα φύλλο) · στις παρειές υποστυλωμάτων μέσα στα διαμερίσματα – ΟΧΙ όπου πλακάκι ή ντουλάπα

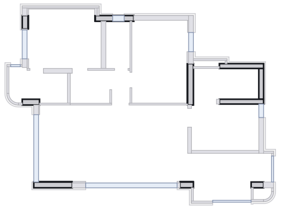

Τοίχοι: T9-01, T9-02, T9-03, T9-04, T9-05

Μήκος 5,75 m · επιφάνεια ≈ 16,7 m²

🟦 T2 Χώρισμα γυψοσανίδας 1:4

πάχος 10 cm

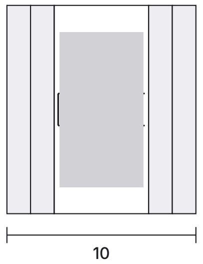

2 × γυψοσανίδα 12,5 · σκελετός CW 50 · 2 × γυψοσανίδα 12,5 · εσωτερικά χωρίσματα · ανθυγρή γυψοσανίδα στην πλευρά των λουτρών

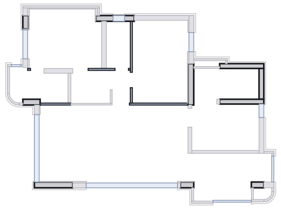

Τοίχοι: T2-01, T2-02, T2-03, T2-04, T2-06, T2-07, T2-08

Μήκος 9,75 m · επιφάνεια ≈ 28,3 m²

🟦 T2N Χώρισμα γυψ. – πλευρά ντουλάπας 1:4

πάχος 8,75 cm

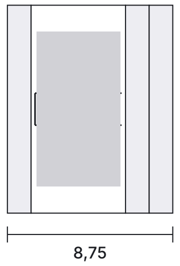

1 × γυψοσανίδα 12,5 (πλευρά ντουλάπας) · σκελετός CW 50 · 2 × γυψοσανίδα 12,5 · όπου η μία παρειά βλέπει σε ντουλάπα: ένα φύλλο αρκεί (κανόνας R15)

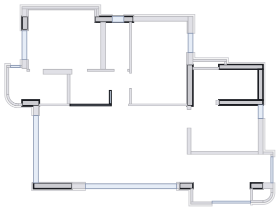

Τοίχοι: T2N-01, T2N-02

Μήκος 2,85 m · επιφάνεια ≈ 8,3 m²

🟦 T2A Χώρισμα γυψοσανίδας 15 1:4

πάχος 15 cm

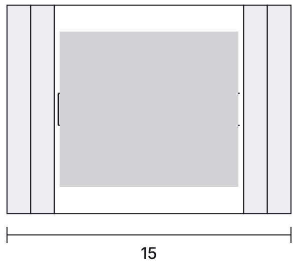

2 × γυψοσανίδα 12,5 · σκελετός CW 100 + πετροβάμβακας · 2 × γυψοσανίδα 12,5 · λουτρό γονέων / χωλ · υπνοδωμάτια

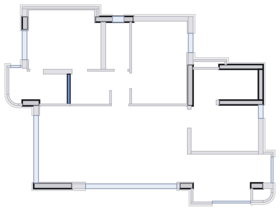

Τοίχοι: T2A-01

Μήκος 1,55 m · επιφάνεια ≈ 4,5 m²

🟪 T7 Τοίχος λεκάνης WC 1:4

πάχος 25 cm

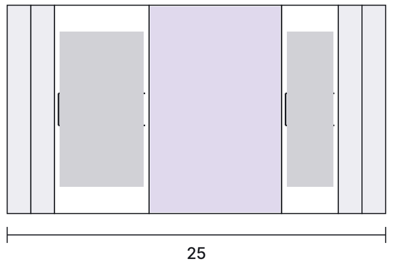

2 × γυψοσανίδα 12,5 · σκελετός CW 50 · κενό 12 cm (καζανάκι γυψοσανίδας στον σκελετό + κατακόρυφη στήλη Ø110, έξοδος Ø90) · σκελετός CW 30 · 2 × γυψοσανίδα 12,5 · ΟΛΟΙ οι τοίχοι λεκανών · ανθυγρή προς το λουτρό · στην πλευρά ντουλάπας 1 φύλλο

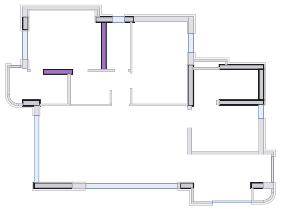

Τοίχοι: T7-01, T7-02

Μήκος 3,95 m · επιφάνεια ≈ 11,5 m²

🟩 T6 Τοίχος κλιμακοστασίου 1:4

πάχος 15 cm

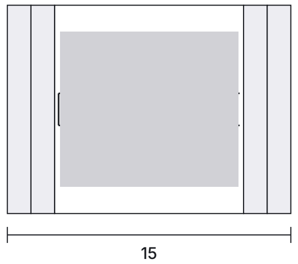

2 × γυψοσανίδα 12,5 πυράντοχη · σκελετός CW 100 + πετροβάμβακας · 2 × γυψοσανίδα 12,5 πυράντοχη · προς κοινόχρηστους χώρους · T6-01 (πόρτα εισόδου) μένει όπως η κάτοψη

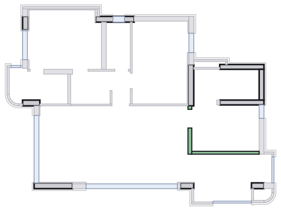

Τοίχοι: T6-01, T6-02, T6-03

Μήκος 5,06 m · επιφάνεια ≈ 14,7 m²

🟨 T8 Τοίχος shaft 1:4

πάχος 10 cm

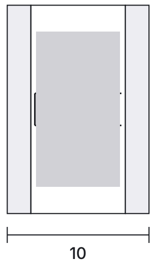

πλαίσιο + ανοιγόμενα φύλλα γυψοσανίδας · μέτωπο shaft ηλεκτρολογικών

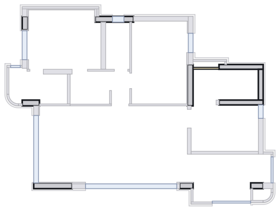

Τοίχοι: T8-01

Μήκος 1,35 m · επιφάνεια ≈ 3,9 m²

Επιφάνειες ενδεικτικές: μήκος × ύψος 2,90 m (τελικό δάπεδο – πλάκα) – οι τοίχοι ορίζονται μεταξύ ανοιγμάτων, χωρίς αφαίρεση κασών. T3 = επένδυση στην εσωτερική παρειά των T1 · T9 = περίμετρος υποστυλώματος × ύψος. R15: T2N = 1 φύλλο στην πλευρά ντουλάπας (T2N-01, T2N-02) · T7-01 1 φύλλο προς Υπν.1.

ΕΡΓΟ

ΠΕΝΤΑΟΡΟΦΟ ΚΤΗΡΙΟ ΚΑΤΟΙΚΙΩΝ – ΑΡΓΥΡΟΥΠΟΛΗ
Κωνσταντινουπόλεως 12 & Αγ. Βαρβάρας · Ο.Τ. 103-15
Εργοδότης: INTERKAT A.E. · Κατασκευή: ARKAD I.K.E.

ΘΕΜΑ ΣΧΕΔΙΟΥ

ΕΙΔΗ ΤΟΙΧΟΠΟΙΙΩΝ – Β΄ ΟΡΟΦΟΣ
Είδη τοιχοποιιών · Β΄ ΟΡΟΦΟΣ – Β1
τομές 1:4 · μήκη – εμβαδά ανά είδος

ΒΑΣΗ

Βάση: κάτοψη τοιχοποιιών T-01 · κάτοψη A-10-2F

ΑΡ. ΣΧΕΔΙΟΥ

T-02
Κλίμακα 1:4 · A3
05/11/2026 · R16

ΠΡΟΜΕΤΡΗΣΗ ΥΛΙΚΩΝ ΤΟΙΧΟΠΟΙΙΩΝ – Β΄ ΟΡΟΦΟΣ – Β1

από την κάτοψη Τ-01 · H = 2,90 m (δάπεδο πλάκας – κάτω παρειά πλάκας) · μήκη στον άξονα κάθε τοίχου, χωρίς αφαίρεση κουφωμάτων (οι τοίχοι ορίζονται μεταξύ ανοιγμάτων) · R15

Είδος	Περιγραφή	Τοίχοι	Μήκος m	Επιφ. m²	Γυψοσ. κοινή m²	Γυψοσ. ανθυγρή m²	Γυψοσ. πυράντ. m²	Σκελετός CW m	Οδηγός UW m	Πετροβάμβ. m²	Θερμοτούβλα τεμ.	Κονίαμα m³	Κόλλα kg
🟧 **T1**	Εξωτερική οπτοπλινθοδομή · 25 cm T1-01, T1-02, T1-03, T1-04, T1-05, T1-06, T1-07, T1-08, T1-09, T1-10, T1-11, T1-12	12	9,52	27,61	–	–	–	–	–	–	461	0,41	–
🟧 **T4**	Έρκερ – απλή οπτοπλινθοδομή · 11 cm T4-01, T4-02, T4-03, T4-04, T4-05, T4-06, T4-07, T4-08, T4-09, T4-10, T4-11, T4-12, T4-13, T4-14, T4-15	15	12,02	34,85	–	–	–	–	–	–	1.342	0,69	–
🟧 **T5**	Οπτοπλινθοδομή πυρήνα · 10 cm T5-01, T5-02	2	1,90	5,51	–	–	–	–	–	–	92	0,03	–
🟦 **T3**	Επένδυση τοίχου · 5,5 cm T3-01, T3-02, T3-03, T3-04, T3-05, T3-06, T3-07, T3-08, T3-09, T3-10	10	7,40	21,45	42,9	–	–	81,2	14,8	–	–	–	–
🟪 **T9**	Επένδυση υποστυλώματος · 2,5 cm T9-01, T9-02, T9-03, T9-04, T9-05	5	5,75	16,68	16,7	–	–	–	–	–	–	–	66,7
🟦 **T2**	Χώρισμα γυψοσανίδας · 10 cm T2-01, T2-02, T2-03, T2-04, T2-06, T2-07, T2-08	7	9,75	30,38	87,3	34,2	–	81,2	19,5	–	–	–	–
🟦 **T2N**	Χώρισμα γυψ, – πλευρά ντουλάπας · 8,75 cm T2N-01, T2N-02	2	2,85	8,27	24,8	–	–	23,2	5,7	–	–	–	–
🟦 **T2A**	Χώρισμα γυψοσανίδας 15 · 15 cm T2A-01	1	1,55	4,49	9,0	9,0	–	11,6	3,1	4,5	–	–	–
🟪 **T7**	Τοίχος λεκάνης WC · 25 cm T7-01, T7-02	2	3,95	11,46	15,8	22,9	–	58,0	15,8	–	–	–	–
🟩 **T6**	Τοίχος κλιμακοστασίου · 15 cm T6-01, T6-02, T6-03	3	5,06	15,35	–	–	61,4	37,7	10,1	15,4	–	–	–
🟨 **T8**	Τοίχος shaft · 10 cm T8-01	1	1,35	3,91	7,8	–	–	11,6	2,7	–	–	–	–

ΛΙΣΤΑ ΠΑΡΑΓΓΕΛΙΑΣ (με φύρα: γυψοσανίδες +10 %, προφίλ +5 %)

Γυψοσανίδα κοινή 12,5 mm 1,20 × 3,00	**224,7 m²**	63 φύλλα
Γυψοσανίδα ανθυγρή (H2) 12,5 mm 1,20 × 3,00 – λουτρά: τοίχοι + οροφές (6,1 m² οροφές)	**79,4 m²**	23 φύλλα
Γυψοσανίδα πυράντοχη (F) 12,5 mm 1,20 × 3,00 – κλιμακοστάσιο	**67,6 m²**	19 φύλλα
Προφίλ CW50 (3,00 m)	**152,2 m**	51 τεμ.
Προφίλ CW30 (3,00 m)	**115,7 m**	39 τεμ.
Προφίλ CW100 (3,00 m)	**51,8 m**	18 τεμ.
Προφίλ UW50 (3,00 m)	**37,6 m**	13 τεμ.
Προφίλ UW30 (3,00 m)	**23,8 m**	8 τεμ.
Προφίλ UW100 (3,00 m)	**13,9 m**	5 τεμ.
Προφίλ CD60 (3,00 m) – ψευδοροφές λουτρών	**20,4 m**	7 τεμ.
Προφίλ UD28 (3,00 m) – ψευδοροφές λουτρών	**15,1 m**	6 τεμ.
Πετροβάμβακας 50 / 100 mm (T2A, T6)	**19,8 m²**	
Γυψόκολλα για κολλητή γυψοσανίδα (T9) ≈ 4 kg/m²	**66,7 kg**	3 σακιά 25 kg
Βίδες γυψοσανίδας TN 25 / 35 ≈ 22 τεμ/m² φύλλου	**7.434 τεμ.**	8 κουτιά 1.000
Στόκος αρμών ≈ 0,45 kg/m² τελικής επιφάνειας	**76,0 kg**	4 σακιά 25 kg
Ταινία αρμών ≈ 1,6 m/m² τελικής επιφάνειας	**270,3 m**	4 ρολά 90 m
Αναρτήσεις ψευδοροφής λουτρών (≈ 1,3 / m²)	**8 τεμ.**	
Θερμοτούβλο κάθετων οπών 25 (30 × 25 × 19) – T1	**484 τεμ.**	+5 % σπασίματα
Απλό τούβλο 6οπο 9 × 12 × 19 – T4 έρκερ	**1.409 τεμ.**	+5 % σπασίματα
Θερμοτούβλο κάθετων οπών 10 (30 × 10 × 19) – T5 πυρήνα	**97 τεμ.**	+5 % σπασίματα
Κονίαμα δόμησης	**1,14 m³**	

ΣΗΜΕΙΩΣΕΙΣ ΚΑΤΟΨΗΣ

- Θέσεις τοίχων και ανοιγμάτων όπως η κάτοψη A-10-2F (Rev.11). Διαστάσεις στο τούβλο / μπετό, χωρίς τη θερμοπρόσοψη (κίτρινη λωρίδα 10 cm).
- ΝΤΟΥΛΑΠΕΣ ΧΩΝΕΥΤΕΣ (R15/R16): δωματίων βάθος 0,60 · πλυντηρίου 0,70. Οι τοίχοι / πεσσοί που τις πλαισιώνουν έχουν ακριβώς το βάθος της ντουλάπας (T2N-02 0,70)· μόνο στον T1-05 περιθώριο +0,03 (ως 1,38). Πίσω και δίπλα σε ντουλάπα καμία επένδυση T3 / T9, ΕΚΤΟΣ παραστάδων κουφωμάτων.
- ΚΟΥΦΩΜΑΤΑ ΑΛΟΥΜΙΝΙΟΥ (R16): τοποθετούνται στη μέση του τοίχου· οι λαμπάδες πρέπει να είναι ισοπαχείς και από τις δύο πλευρές → επένδυση γυψοσανίδας T3 και στις δύο παραστάδες κάθε κουφώματος (T3-06 στον T1-05 μένει, δίπλα στη ντουλάπα).
- T1-05: κόπηκε στο 1,38 (ντουλάπα Υπν.2 0,60 + 0,03). Το W2.06 (1,00×2,40) μετατοπίζεται 7 cm βόρεια: 1,38–2,38 (εγκρίθηκε από τον ιδιοκτήτη 05/11 – να ενημερωθεί ο αρχιτέκτονας).
- Υπν.1: ντουλάπα 0,60 (x 4,30–4,90, y 0,80–3,25) ανάμεσα στον T2-01 και την K2. Το κενό προς τον βόρειο τοίχο (x 4,30–4,57 × y 0,165–0,80) ΔΕΝ κτίζεται: γεμίζει με ξυλουργικό που συνεχίζει τη ντουλάπα (βιβλιοθήκη / κομοδίνο). Πόρτα 3,40–4,20.
- ΤΟΙΧΟΙ ΠΟΥ ΒΛΕΠΟΥΝ ΣΕ ΝΤΟΥΛΑΠΑ: 1 φύλλο γυψοσανίδας στην πλευρά της ντουλάπας (T2N-01, T2N-02 · T7-01 πλευρά Υπν.1).
- ΛΟΥΤΡΑ: σχεδιάζονται μόνο πάγκος νιπτήρα βάθους 0,50, λεκάνη και ένα γυάλινο διαχωριστικό ντους 0,70. Ντους 0,70–1,00 (λουτρό 1,00×0,80 · λουτρό γονέων 1,00×0,90). Λουτρό: ντους βόρεια (0,80), γυαλί 0,70 στο y 1,60 από τον T7-01. Λουτρό γονέων: ντους στη δυτική εσοχή (W2.09), γυαλί 0,70 στο x 1,20 από τον νότιο τοίχο.
- ΤΟΙΧΟΙ ΛΕΚΑΝΗΣ T7: 2 γυψ. + CW 50 (καζανάκι γυψοσανίδας) + κενό 12 + CW 30 + 2 γυψ. = 25 cm. T7-01: σταθερή η παρειά του λουτρού. T7-02: σταθερή η παρειά του Υπν.1.
- ΟΠΟΥ ΠΛΑΚΑΚΙ Ή ΝΤΟΥΛΑΠΑ: χωρίς γυψοσανίδα σε τούβλο / μπετό. Επενδύσεις T3 / T9 σε ενιαίο επίπεδο, χωρίς δόντια.
- W2.07 (λουτρό, 0,60×0,90, ποδιά +1,50 από Τ.Δ.): το παράθυρο βρίσκεται ΜΕΣΑ στο τοιχείο K2 (x 5,50–6,10). Το κενό 0,60 × 0,90 κρατιέται ΑΠΟ ΤΩΡΑ στον ξυλότυπο του τοιχείου (στάθμες +1,50 … +2,40 από το τελικό δάπεδο Β΄, δηλ. ≈ +8,40 … +9,30). Να ενημερωθεί ο στατικός (Κόγιας) για την οπή στο τοιχείο.
- ΠΟΡΤΕΣ (R16): ανοίγουν μέσα στον χώρο που εξυπηρετούν. Υπν.1 μεντεσές δυτικά (3,40), λουτρό μεντεσές ανατολικά (6,30), λουτρό γονέων μεντεσές ανατολικά (1,90) ώστε να μένει ελεύθερη η είσοδος του ντους, Υπν.2 μεντεσές νότια (4,25).
- T5-01 κόβεται στην άκρη του εξώστη (x 11,45) με επιστροφή T5-02 στο τοιχείο του ασανσέρ. Υποστυλώματα (σκούρο γκρι) κατά Σ5. Εξώστες από την κάτοψη A-10-2F.

ΠΑΡΑΔΟΧΕΣ

- Γυψοσανίδες 12,5 mm σε φύλλα 1,20 × 3,00 (ένα φύλλο καθ' ύψος για H = 2,90). Ανθυγρή όπου η πλευρά βλέπει λουτρό / WC, πυράντοχη στον T6.
- Ορθοστάτες CW ανά 60 cm (+1 ανά τοίχο), οδηγοί UW δάπεδο + οροφή. T7: δύο σκελετοί (CW 50 + CW 30). T3: σκελετός 3άρι μίας πλευράς. T9: χωρίς σκελετό, σε γυψόκολλα.
- R15/R16: στην πλευρά ντουλάπας ένα φύλλο (T2N-01, T2N-02, T7-01 προς Υπν.1) – αφαιρέθηκε από τα m² γυψοσανίδας.
- Υπέρθυρα πάνω από τις πόρτες (H – 2,20) προστέθηκαν στο είδος του τοίχου της πόρτας: 5 πόρτες.
- Τούβλα: T1 / T5 θερμομονωτικά κάθετων οπών (30 × 19 → ≈ 16,7 τεμ/m²) · T4 έρκερ απλό τούβλο 6οπο 9 × 12 × 19 δρομικό (≈ 38,5 τεμ/m²). ΠΡΟΣ ΕΠΙΒΕΒΑΙΩΣΗ οι διαστάσεις του προμηθευτή.
- ΛΟΥΤΡΑ: ό,τι είναι μέσα στο λουτρό (τοίχοι και οροφή) με ανθυγρή. Ψευδοροφές λουτρών: 1 × ανθυγρή 12,5 σε CD 60 / UD 28 (Λουτρό 3,06 m² · Λουτρό Γονέων 3,02 m²). Λοιπές ψευδοροφές στο τεύχος ανόψεων.
- Δεν περιλαμβάνονται: σοβάδες, πλακάκια, γωνιόκρανα γυψοσανίδας, κάσες / πρέκια, ηχομονωτικές ταινίες περιμέτρου.
- Όπου πλακάκι ή ντουλάπα: χωρίς γυψοσανίδα σε τούβλο / μπετό – ήδη εξαιρέθηκαν από την προμέτρηση.

ΘΕΡΜΟΠΡΟΣΟΨΗ (ETICS) 10 cm

ύψος ορόφου 3,10 m (με τη μετώπη πλάκας) · ύψη κουφωμάτων από τα label · όπως R14 (τα κουφώματα δεν άλλαξαν)

Περίμετρος όψεων	**47,76 m**
Κουφώματα (9 ανοίγματα)	**−29,61 m²**
Λαμπάδες + ανώφλια (βάθος ≈ 0,15)	**+6,63 m²**
ΚΑΘΑΡΗ ΕΠΙΦΑΝΕΙΑ	**125,1 m²**
Πλάκα EPS γραφιτούχο 10 cm (+5 %) · 263 πλ. 1,00×0,50	**131,3 m²**
Κόλλα – βασικός σοβάς ≈ 9 kg/m² · 46 σακιά	**1.126 kg**
Υαλόπλεγμα 160 g ≈ 1,15 m²/m² · 3 ρολά 50 m²	**143,8 m²**
Βύσματα ETICS ≈ 6 / m²	**750 τεμ.**
Γωνιόκρανα με πλέγμα (κουφώματα)	**46,4 m**
Αστάρι ≈ 0,25 kg/m²	**31 kg**
Τελικός σοβάς ≈ 2,5 kg/m²	**313 kg**

ΕΡΓΟ

ΠΕΝΤΑΟΡΟΦΟ ΚΤΗΡΙΟ ΚΑΤΟΙΚΙΩΝ – ΑΡΓΥΡΟΥΠΟΛΗ
Κωνσταντινουπόλεως 12 & Αγ. Βαρβάρας · Ο.Τ. 103-15
Εργοδότης: INTERKAT A.E. · Κατασκευή: ARKAD I.K.E.

ΘΕΜΑ ΣΧΕΔΙΟΥ

ΠΡΟΜΕΤΡΗΣΗ ΥΛΙΚΩΝ – Β΄ ΟΡΟΦΟΣ
Γυψοσανίδες · σκελετοί · τούβλα · αναλώσιμα
Β΄ ΟΡΟΦΟΣ – Β1

ΒΑΣΗ

Βάση: κάτοψη τοιχοποιιών Τ-01 · είδη Τ-02

ΑΡ. ΣΧΕΔΙΟΥ

T-03
— · A3
05/11/2026 · R16