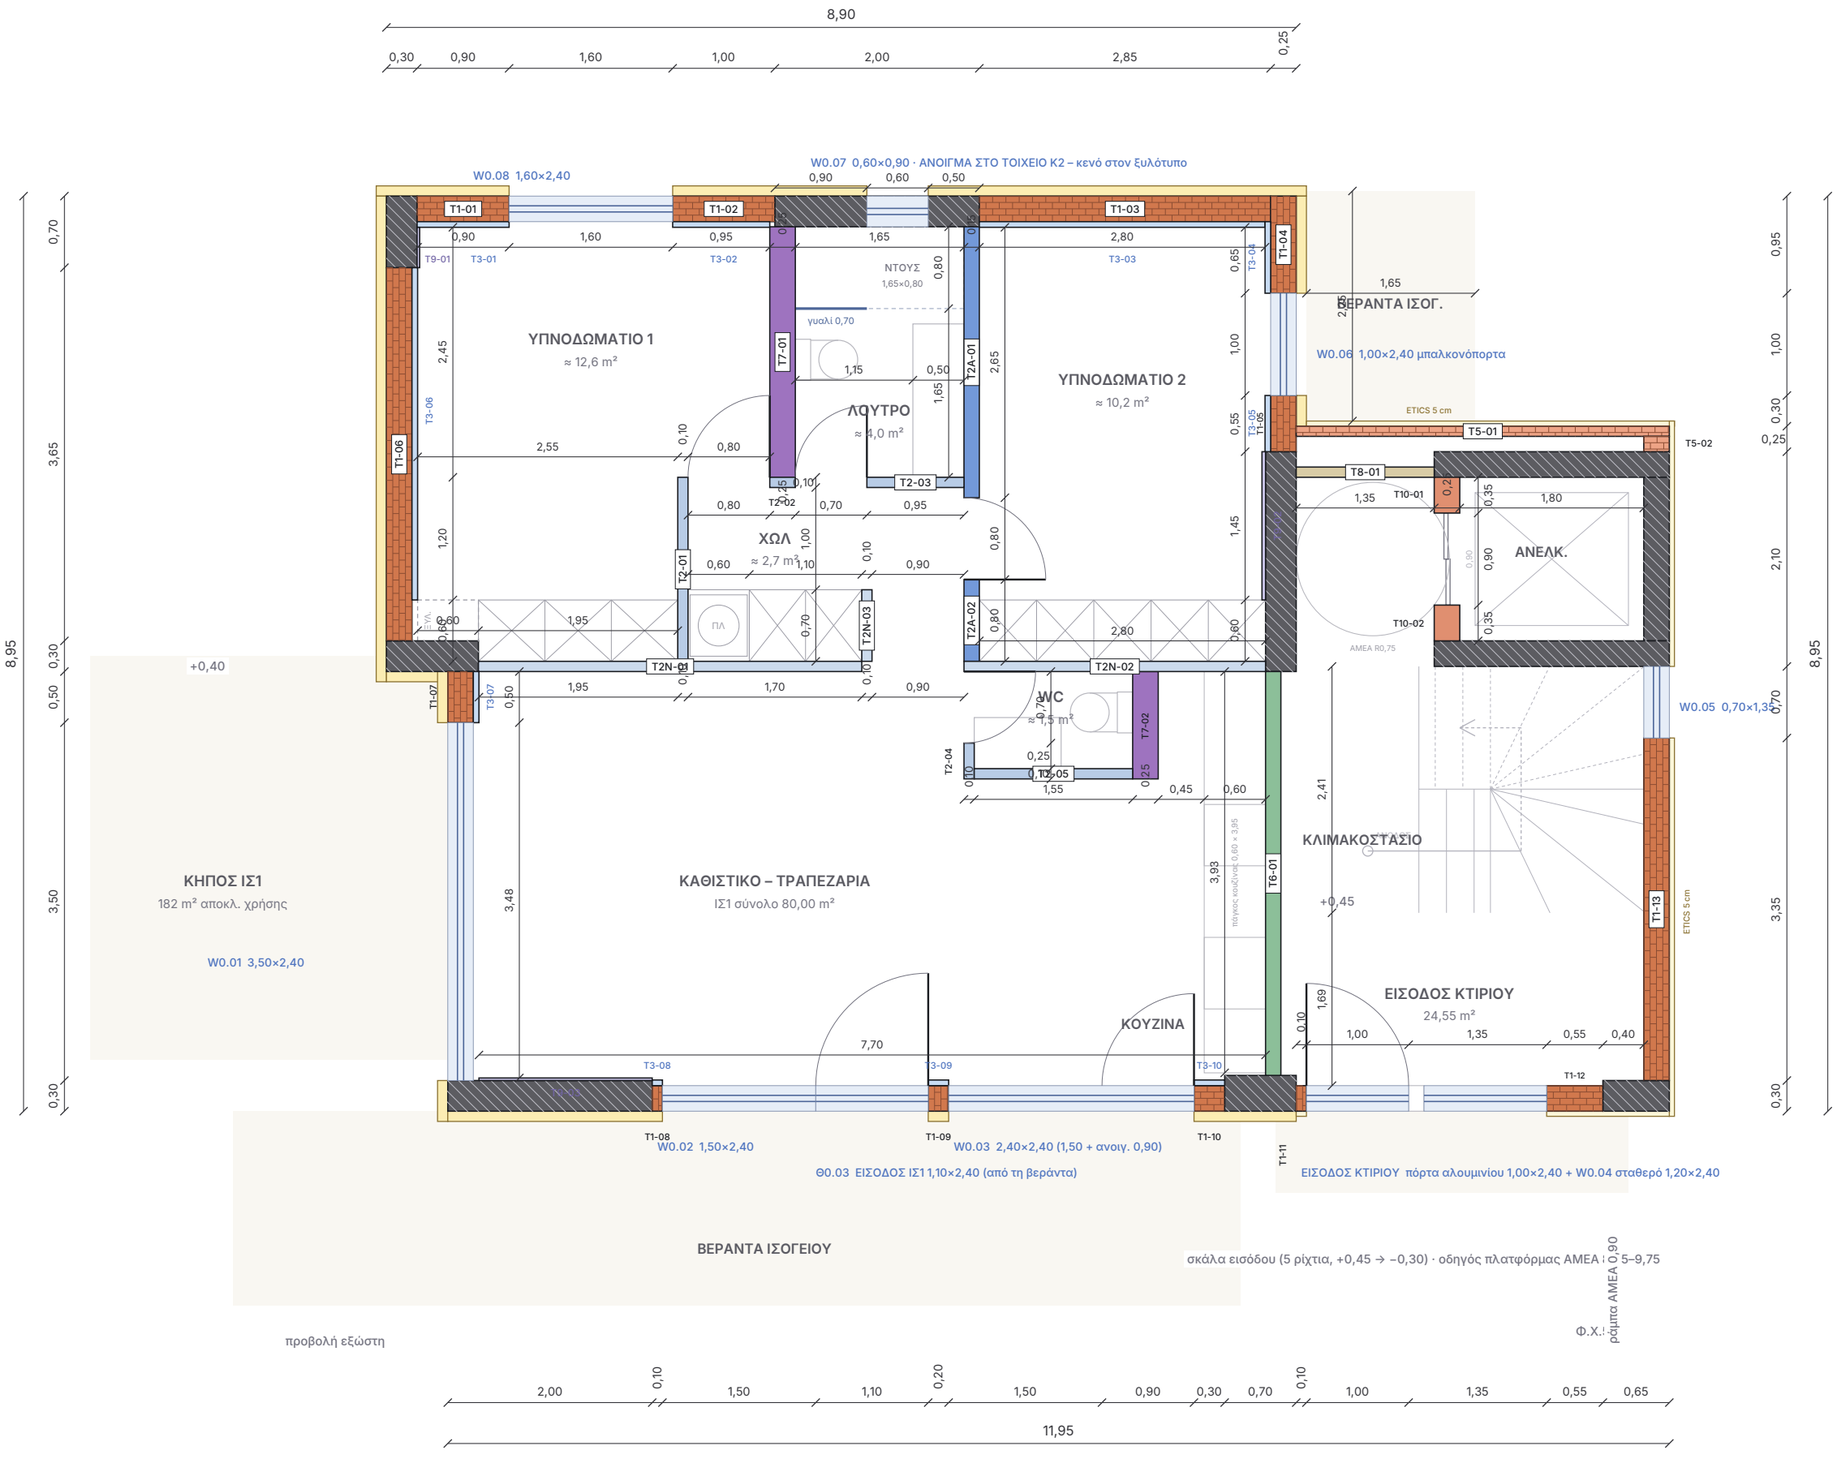


ΙΣΟΓΕΙΟ R01 – ΔΙΟΡΘΩΣΕΙΣ & ΠΑΡΑΔΟΧΕΣ (05/11/2026)


- R01: ΕΙΣΟΔΟΣ ΚΤΙΡΙΟΥ = πόρτα αλουμινίου 1,00×2,40 στον νότιο τοίχο του lobby (9,80–10,80, μεντεσές δυτικά, ανοίγει μέσα) + σταθερό W0.04 1,20 (10,95–12,15), ενιαίο κούφωμα
- R01: ΚΑΜΙΑ πόρτα διαμερίσματος προς το lobby (T6-01 συμπαγής 5,15–9,10, πάγκος κουζίνας 3,95 κατά A-10-GF) · είσοδος ΙΣ1 = Θ0.03 1,10 από τη νότια βεράντα
- R01: δυτικός τοίχος καθιστικού 1,40–1,70 (T1-07 + W0.01 5,65–9,15, περασιά με το ΝΔ τοιχείο και το Δ υποστύλωμα) · θερμοπρόσοψη στο 1,30–1,40
- R01: T5-01 σε όλο το μήκος 9,70–13,35 + T5-02 επιστροφή · shaft Η/Μ 2,85–3,15 · κύκλος AMEA R0,75 (όχι αναβατόριο) · T2A στο 6,45–6,60 · WC 1,55 · πόρτα Υπν.1 μεντεσές 4,55
- Οι δύο «Αποθήκες εκτός Σ.Δ.» γίνονται ντουλάπες 0,60 χωνευτές (Γιάννης 05/11): Υπν.1 1,95 + ξυλουργικό 0,40 · Υπν.2 2,80 · πλυντήριο 0,60 + ντουλάπα 1,10 (0,70)
- Λουτρό: ντους 1,65×0,80 βόρεια, γυαλί 0,70 · λεκάνη στον T7-01 · πάγκος 0,50 ανατολικά · WC: λεκάνη στον T7-02, πάγκος 0,50 νότια
- Πόρτες μέσα στον χώρο, ισοπαχείς παραστάδες, ορθοστάτες UA 2 mm · T6 15 cm · T10 25 cm · T3 και στις δύο παραστάδες κάθε κουφώματος
- W0.07 μέσα στο τοιχείο Κ2: κενό 0,60×0,90 στον ξυλότυπο (ποδιά +1,50) · θερμοπρόσοψη 10 cm διαμέρισμα · 5 cm είσοδος / πυρήνας

ΕΡΓΟ	ΘΕΜΑ ΣΧΕΔΙΟΥ	ΒΑΣΗ	ΑΡ. ΣΧΕΔΙΟΥ
ΠΕΝΤΑΟΡΟΦΟ ΚΤΗΡΙΟ ΚΑΤΟΙΚΙΩΝ – ΑΡΓΥΡΟΥΠΟΛΗ Κωνσταντινουπόλεως 12 & Αγ. Βαρβάρας · Ο.Τ. 103-15 Εργοδότης: INTERKAT Α.Ε. · Κατασκευή: ARKAD Ι.Κ.Ε.	**ΚΑΤΟΨΗ ΤΟΙΧΟΠΟΙΙΩΝ – ΙΣΟΓΕΙΟΥ** Είδη τοιχοποιιών · διαστάσεις χάραξης · κουφώματα · εξώστες ΙΣΟΓΕΙΟ – ΙΣ1	Βάση: κάτοψη A-10-GF (μελέτη εφαρμογής) · ξυλότυπος Σ3_ΕΦ · κανόνες Β1 R26	**Τ-01** **Κλίμακα 1:60 · Α3** 05/11/2026 · R01

T1 Εξωτερική οπτοπλινθοδομή

1:4

πάχος 25 cm

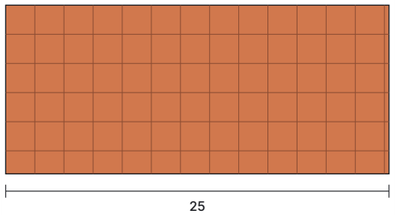

θερμομονωτικό τούβλο κάθετων οπών 25 cm · θερμοπρόσοψη 10 cm έξω · επένδυση Τ3 μέσα όπου σημειώνεται




Τοίχοι: T1-01, T1-02, T1-03, T1-04, T1-05, T1-06, T1-07, T1-08, T1-09, T1-10, T1-11, T1-12, T1-13

Μήκος 15,35 m · επιφάνεια ≈ 46,0 m²


T5 Οπτοπλινθοδομή πυρήνα

1:4

πάχος 10 cm

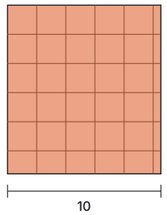

θερμομονωτικό τούβλο κάθετων οπών 10 cm · γύρω από τον πυρήνα (ανελκυστήρας – ηλεκτροστάσιο)

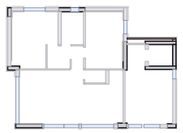


Τοίχοι: T5-01, T5-02

Μήκος 3,90 m · επιφάνεια ≈ 11,7 m²


T10 Μέτωπο ανελκυστήρα

1:4

πάχος 25 cm

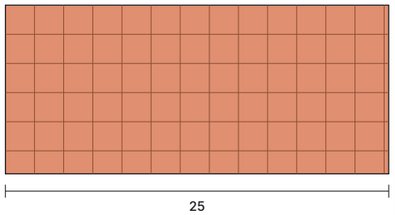

θερμομονωτικό τούβλο κάθετων οπών 25 cm · μέτωπο φρεατίου εκατέρωθεν της πόρτας 0,90 · ισοπαχές με τα τοιχεία 25 του φρεατίου (Σ5), περασιά και στις δύο παρειές, ώστε να κάθεται σωστά η κάσα της πόρτας ορόφου · θέση πόρτας προς επιβεβαίωση από τον προμηθευτή

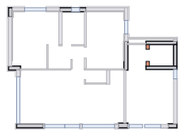


Τοίχοι: T10-01, T10-02

Μήκος 0,70 m · επιφάνεια ≈ 2,1 m²


T3 Επένδυση τοίχου

1:4

πάχος 5,5 cm

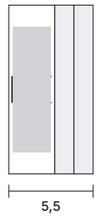

σκελετός 30 · 2 × γυψοσανίδα 12,5 · στις εσωτερικές παρειές των Τ1 – ΟΧΙ όπου πλακάκι ή ντουλάπα, ΟΧΙ στα έρκερ

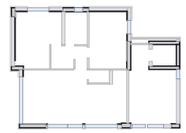


Τοίχοι: T3-01, T3-02, T3-03, T3-04, T3-05, T3-06, T3-07, T3-08, T3-09, T3-10

Μήκος 10,25 m · επιφάνεια ≈ 30,7 m²

T9 Επένδυση υποστυλώματος

1:4

πάχος 2,5 cm

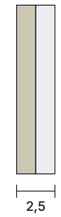

κόλλα + 1 × γυψοσανίδα 12,5 (ένα φύλλο) · στις παρειές υποστυλωμάτων μέσα στα διαμερίσματα – ΟΧΙ όπου πλακάκι ή ντουλάπα




Τοίχοι: T9-01, T9-02, T9-03

Μήκος 3,54 m · επιφάνεια ≈ 10,6 m²


T2 Χώρισμα γυψοσανίδας

1:4

πάχος 10 cm

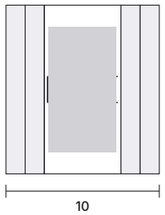

2 × γυψοσανίδα 12,5 · σκελετός CW 50 · 2 × γυψοσανίδα 12,5 · εσωτερικά χωρίσματα · ανθυγρή γυψοσανίδα στην πλευρά των λουτρών · ανοίγματα πορτών με ορθοστάτες UA 50 (2 mm)

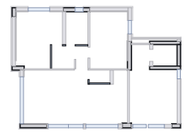


Τοίχοι: T2-01, T2-02, T2-03, T2-04, T2-05

Μήκος 4,90 m · επιφάνεια ≈ 14,7 m²


T2N Χώρισμα γυψ. – πλευρά ντουλάπας

1:4

πάχος 8,75 cm

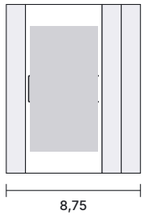

1 × γυψοσανίδα 12,5 (πλευρά ντουλάπας) · σκελετός CW 50 · 2 × γυψοσανίδα 12,5 · όπου η μία παρειά βλέπει σε ντουλάπα: ένα φύλλο αρκεί (κανόνας R15)

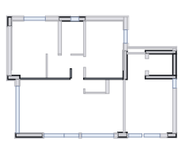


Τοίχοι: T2N-01, T2N-02, T2N-03

Μήκος 7,40 m · επιφάνεια ≈ 22,2 m²


T2A Χώρισμα γυψοσανίδας 15

1:4

πάχος 15 cm

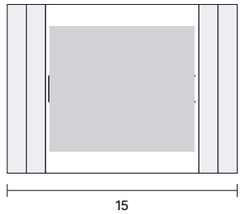

2 × γυψοσανίδα 12,5 · σκελετός CW 100 + πετροβάμβακας · 2 × γυψοσανίδα 12,5 · λουτρό γονέων / χωλ · υπνοδωμάτια · ανοίγματα πορτών με ορθοστάτες UA 100 (2 mm)

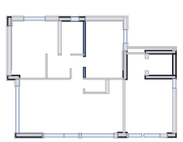


Τοίχοι: T2A-01, T2A-02

Μήκος 3,45 m · επιφάνεια ≈ 10,4 m²


T7 Τοίχος λεκάνης WC

1:4

πάχος 25 cm

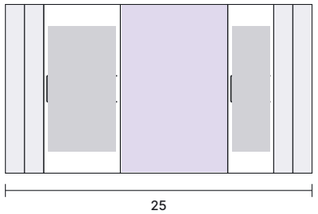

2 × γυψοσανίδα 12,5 · σκελετός CW 50 · κενό 12 cm (καζανάκι γυψοσανίδας στον σκελετό + κατακόρυφη στήλη Ø110, έξοδος Ø90) · σκελετός CW 30 · 2 × γυψοσανίδα 12,5 · ΟΛΟΙ οι τοίχοι λεκανών · ανθυγρή προς το λουτρό · στην πλευρά ντουλάπας 1 φύλλο · ανοίγματα πορτών με ορθοστάτες UA 50 (2 mm)

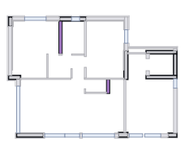


Τοίχοι: T7-01, T7-02

Μήκος 3,50 m · επιφάνεια ≈ 10,5 m²


T6 Τοίχος κλιμακοστασίου

1:4

πάχος 15 cm

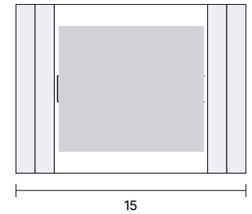

2 × γυψοσανίδα 12,5 πυράντοχη · σκελετός CW 100 + πετροβάμβακας · 2 × γυψοσανίδα 12,5 πυράντοχη · προς κοινόχρηστους χώρους · 15 cm · άνοιγμα πόρτας εισόδου (ασφαλείας) με ορθοστάτες UA 100 (2 mm) κατά Knauf

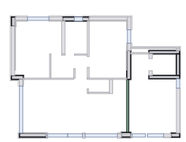


Τοίχοι: T6-01

Μήκος 3,95 m · επιφάνεια ≈ 11,8 m²


T8 Τοίχος shaft

1:4

πάχος 10 cm

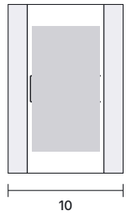

πλαίσιο + ανοιγόμενα φύλλα γυψοσανίδας · μέτωπο shaft ηλεκτρολογικών

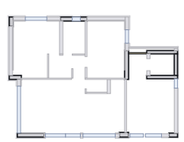

Τοίχοι: T8-01

Μήκος 1,35 m · επιφάνεια ≈ 4,1 m²

Επιφάνειες ενδεικτικές: μήκος × ύψος 3,00 m (τελικό δάπεδο – πλάκα) – οι τοίχοι ορίζονται μεταξύ ανοιγμάτων, χωρίς αφαίρεση κασών. Τ3 = επένδυση στην εσωτερική παρειά των Τ1 · Τ9 = περίμετρος υποστυλώματος × ύψος. R15: T2N = 1 φύλλο στην πλευρά ντουλάπας (T2N-01, T2N-02) · T7-01 1 φύλλο προς Υπν.1.

ΕΡΓΟ

ΠΕΝΤΑΟΡΟΦΟ ΚΤΗΡΙΟ ΚΑΤΟΙΚΙΩΝ – ΑΡΓΥΡΟΥΠΟΛΗ
Κωνσταντινουπόλεως 12 & Αγ. Βαρβάρας · Ο.Τ. 103-15
Εργοδότης: INTERKAT Α.Ε. · Κατασκευή: ARKAD Ι.Κ.Ε.

ΘΕΜΑ ΣΧΕΔΙΟΥ

ΕΙΔΗ ΤΟΙΧΟΠΟΙΙΩΝ – ΙΣΟΓΕΙΟΥ
Είδη τοιχοποιιών · ΙΣΟΓΕΙΟ – ΙΣ1
τομές 1:4 · μήκη – εμβαδά ανά είδος

ΒΑΣΗ

Βάση: κάτοψη τοιχοποιιών Τ-01 · κάτοψη Α-10-GF

ΑΡ. ΣΧΕΔΙΟΥ

Τ-02
Κλίμακα 1:4 · Α3
05/11/2026 · R01

ΠΡΟΜΕΤΡΗΣΗ ΤΟΙΧΟΠΟΙΙΩΝ – ΙΣΟΓΕΙΟ – ΙΣ1

τετραγωνικά ανά τυπολογία τοίχου · Η = 3,00 m (τελικό δάπεδο – κάτω παρειά πλάκας) · μήκη στον άξονα, χωρίς αφαίρεση κουφωμάτων · R01

	Τύπος	Περιγραφή	Πάχος cm	Τοίχοι	Μήκος m	Επιφάνεια m²
ΤΟΥΒΛΑ						
	T1	Εξωτερική οπτοπλινθοδομή	25	13	15,35	**46,0**
	T5	Οπτοπλινθοδομή πυρήνα	10	2	3,90	**11,7**
	T10	Μέτωπο ανελκυστήρα	25	2	0,70	**2,1**
	Σύνολο τουβλα					**59,9 m²**
ΧΩΡΙΣΜΑΤΑ ΓΥΨΟΣΑΝΙΔΑΣ						
	T2	Χώρισμα γυψοσανίδας	10	5	4,90	**14,7**
	T2N	Χώρισμα γυψ. – πλευρά ντουλάπας	8,8	3	7,40	**22,2**
	T2A	Χώρισμα γυψοσανίδας 15	15	2	3,45	**10,4**
	T7	Τοίχος λεκάνης WC	25	2	3,50	**10,5**
	T6	Τοίχος κλιμακοστασίου	15	1	3,95	**11,8**
	T8	Τοίχος shaft	10	1	1,35	**4,1**
	Σύνολο χωρισματα γυψοσανιδας					**73,7 m²**
ΕΠΕΝΔΥΣΕΙΣ						
	T3	Επένδυση τοίχου	5,5	10	10,25	**30,7**
	T9	Επένδυση υποστυλώματος	2,5	3	3,54	**10,6**
	Σύνολο επενδυσεις					**41,4 m²**
	ΣΥΝΟΛΟ ΤΟΙΧΟΠΟΙΙΩΝ ΙΣ1					**174,9 m²**

ΘΕΡΜΟΠΡΟΣΟΨΗ (ETICS)

10 cm στις όψεις των διαμερισμάτων · 5 cm στο κλιμακοστάσιο / πυρήνα · ύψος 3,20 m (με τη μετώπη πλάκας) · καθαρά = όψη − κουφώματα + λαμπάδες/ανώφλια

Ζώνη	Μήκος όψης m	Μικτά m²	Κουφώματα m²	Λαμπάδες m²	Καθαρά m²
ETICS 10 cm – διαμερίσματα	29,40	94,1	−27,2	+5,9	**72,8**
ETICS 5 cm – κλιμακοστάσιο / πυρήνας	13,90	44,5	−6,2	+2,0	**40,2**
Σύνολο ETICS					**113,1 m²**

ΣΗΜΕΙΩΣΕΙΣ ΚΑΤΟΨΗΣ

• Θέσεις τοίχων και ανοιγμάτων κατά την κάτοψη ισογείου Α-10-GF (EDGE 23/07/2026) με τους κανόνες του Β1 R20. Διαστάσεις στο τούβλο / μπετό, χωρίς τη θερμοπρόσοψη. Υποστυλώματα / τοιχεία από τα μαύρα γεμίσματα του Α-10-GF – ταυτίζονται με τον ξυλότυπο Σ3 (να επιβεβαιωθούν στον Σ3 πριν τη χάραξη).

• ΕΙΣΟΔΟΣ ΚΤΙΡΙΟΥ (R01): στον νότιο τοίχο του lobby, ενιαίο κούφωμα αλουμινίου 2,35: πόρτα 1,00×2,40 στο 9,80–10,80 (μεντεσές δυτικά 9,80, ανοίγει μέσα, διπλώνει στον πεσσό / Ν υποστύλωμα) + κολωνάκι 0,15 + σταθερό W0.04 1,20×2,40 στο 10,95–12,15. Πεσσοί τούβλου Τ1-11 9,70–9,80 (0,10) και Τ1-12 12,15–12,70. Έξω: πλατύσκαλο +0,45 (9,50–12,95 × 9,45–10,25), σκάλα 5 ριχτιών προς το πεζοδρόμιο, ράμπα / πλατφόρμα ΑΜΕΑ.

• ΔΙΑΜΕΡΙΣΜΑ ΙΣ1 – ΚΑΜΙΑ ΠΟΡΤΑ ΠΡΟΣ ΤΟ LOBBY (R01): ο αρχιτέκτονας δεν έχει πόρτα στον τοίχο 9,40–9,70 (ο πάγκος κουζίνας 0,60 τρέχει 5,15–9,10). Ο Τ6-01 (15 cm, πυράντοχος) είναι συμπαγής ως το Ν υποστύλωμα. Είσοδος του ΙΣ1 = Θ0.03 1,10×2,40 από τη νότια βεράντα (μεντεσές 6,10, ανοίγει μέσα), πρόσβαση από τον κήπο αποκλειστικής χρήσης (182 m²). Αν ο Γιάννης θέλει πόρτα από το lobby, μπαίνει μόνο στον Τ6-01 κόβοντας τον πάγκο.

• ΑΠΟΘΗΚΕΣ → ΝΤΟΥΛΑΠΕΣ (Γιάννης 05/11): η αποθήκη του Υπν.1 (1,10–3,55 × 3,80–5,00, άνοιγμα 1,95–2,70) και η αποθήκη του Υπν.2 (6,60–9,40 × 3,00–5,00, άνοιγμα 7,45–8,60) καταργούνται· τα δωμάτια μεγαλώνουν ως το y 4,45 και παίρνουν ντουλάπα 0,60 χωνευτή στο y 4,45–5,05. Οι εσωτερικοί τοίχοι τους (y 3,65–3,80 και y 2,85–3,00) δεν κτίζονται.

• Υπν.1 (1,105–4,55 × 0,805–4,45): ντουλάπα 1,70–3,65 (1,95) ανάμεσα στο Δ υποστύλωμα (0,80–1,70 × 4,85–5,15) και τον Τ2-01. Μπροστά από το υποστύλωμα (x 1,105–1,70) ξυλουργικό βάθους 0,40 που συνεχίζει τη ντουλάπα (ως το γυμνό μπετό, χωρίς Τ9). Πόρτα 0,80 στο 3,75–4,55 (τοίχος 10 cm και στις δύο παραστάδες: Τ2-01 / Τ2-02), μεντεσές ανατολικά 4,55 όπως ο αρχιτέκτονας – διπλώνει στον Τ7-01.

• ΧΩΛ 2,70 × 1,00 (y 3,35–4,35) με ντουλάπα πλυντηρίου 0,70 στο y 4,35–5,05 (πλυντήριο 3,75–4,35 + ντουλάπα 4,35–5,45), Τ2N-03 επιστροφή 5,45–5,55, άνοιγμα προς καθιστικό 5,55–6,45 (0,90, όπως Α-10-GF). Τοίχοι που βλέπουν σε ντουλάπα: 1 φύλλο (Τ2N-01, Τ2N-02, Τ2N-03).

• ΛΟΥΤΡΟ 1,65 × 2,45 (x 4,80–6,45 · y 0,80–3,25): Τ7-01 λεκάνης δυτικά (σταθερή η παρειά Υπν.1 4,55), Τ2Α-01 ανατολικά 6,45–6,60 (Α-10-GF), ντους 1,65×0,80 βόρεια (y 0,80–1,60) με γυάλινο διαχωριστικό 0,70 στο y 1,60 από τον Τ7-01, λεκάνη στον Τ7-01 (y 2,10), πάγκος 0,50 στον ανατολικό τοίχο (5,95–6,45 × 1,75–3,25), πόρτα 0,70 στο 4,80–5,50 (μεντεσές 5,50). W0.07 0,60×0,90 μέσα στο τοιχείο Κ2 (x 5,50–6,10): κενό στον ξυλότυπο από τώρα (ποδιά +1,50).

• Υπν.2 (6,60–9,40 × 0,805–4,45): ντουλάπα 6,60–9,40 × 4,45–5,05 (2,80), πόρτα 0,80 από το χωλ στο y 3,45–4,25 (Τ2Α-01 / Τ2Α-02, μεντεσές 4,25), W0.06 1,00×2,40 μπαλκονόπορτα προς τη ΒΑ βεράντα (9,80–11,45 × 0,45–2,70, +0,45).

• WC 1,55 × 0,95 (x 6,55–8,10 · y 5,15–6,10, όπως Α-10-GF): λεκάνη στον ανατολικό τοίχο Τ7-02 (25 cm, 8,10–8,35 – ο αρχιτέκτονας 10 cm), πάγκος 0,50 νότια, πόρτα 0,70 γωνιακή 5,15–5,85 στον δυτικό τοίχο (μεντεσές 5,15, διπλώνει στον βόρειο τοίχο, όπως Α-10-GF). Τ2-04 πεσσός 6,45–6,55 × 5,85–6,20.

• ΚΟΥΖΙΝΑ: πάγκος 0,60 × 3,95 στον Τ6-01 (x 8,80–9,40, y 5,15–9,075) κατά Α-10-GF, με εστίες και νεροχύτη. Πίσω από τον πάγκο χωρίς επένδυση (ο Τ6-01 είναι γυψοσανίδα, το Ν υποστύλωμα γυμνό – Τ9-04 καταργήθηκε).

• ΚΑΘΙΣΤΙΚΟ: δυτικός τοίχος Τ1-07 1,40–1,65 + Τ3-07 (R01, ο αρχιτέκτονας 1,40–1,70) περασιά με το ΝΔ τοιχείο (1,40–3,40) και την ανατολική παρειά του Δ υποστυλώματος (1,70). W0.01 3,50×2,40 στο 5,65–9,15. Η δυτική όψη κάνει σκαλοπάτι 0,60 στο y 5,15 (από 0,80 σε 1,40) – θερμοπρόσοψη 10 στη νότια παρειά του υποστυλώματος.

• ΠΥΡΗΝΑΣ: Τ5-01 10 cm σε όλο το μήκος 9,70–13,35 (Α-10-GF) με επιστροφή Τ5-02 στο φρεάτιο· shaft Η/Μ εκτός Σ.Δ. στο y 2,85–3,15 × 9,70–11,05 (βάθος 0,30 όπως Β1, συνεχές καθ' ύψος – ο αρχιτέκτονας δείχνει μέτωπο 25 στο 3,00–3,25) και 2,85–3,00 μπροστά στο φρεάτιο. Μέτωπο ανελκυστήρα Τ10-01/Τ10-02 25 cm, πόρτα 0,90 στο y 3,60–4,50. Κύκλος περιστροφής ΑΜΕΑ R0,75 (1,50) στο 9,70–11,20. Σκάλα 16 ριχτιών όπως Β1.

• ΚΟΥΦΩΜΑΤΑ (πίνακας κουφωμάτων Α-10-GF): W0.08 1,60×2,40 (2,00–3,60) · W0.07 0,60×0,90 · W0.06 1,00×2,40 (1,45–2,45) · W0.01 3,50×2,40 (5,65–9,15) · W0.02 1,50 (3,50–5,00) · Θ0.03 πόρτα 1,10 (5,00–6,10) · W0.03 2,40 = 1,50 + ανοιγόμενο 0,90 (6,30–8,70) · είσοδος 1,00 + W0.04 1,20 · W0.05 0,70×1,35. Πεσσοί 0,10 (3,40–3,50 και 9,70–9,80), 0,20 (6,10–6,30), 0,30 (8,70–9,00) όπως ο αρχιτέκτονας – ΠΡΟΣ ΑΠΟΦΑΣΗ αν οι 0,10 ενσωματωθούν στα κουφώματα. Τ3 και στις δύο παραστάδες.

• ΘΕΡΜΟΠΡΟΣΟΨΗ: 10 cm στο διαμέρισμα (Β, Δ, Ν όψεις και Α του Υπν.2), 5 cm στον πυρήνα / είσοδο κτιρίου (Τ5-01, φρεάτιο, Τ1-13, πεσσοί νότιου τοίχου lobby). ΥΨΟΣ ισογείου 3,00 (πλάκα οροφής +3,65 κατά Σ3) – οι επιφάνειες του Τ-03 με Η = 3,00.