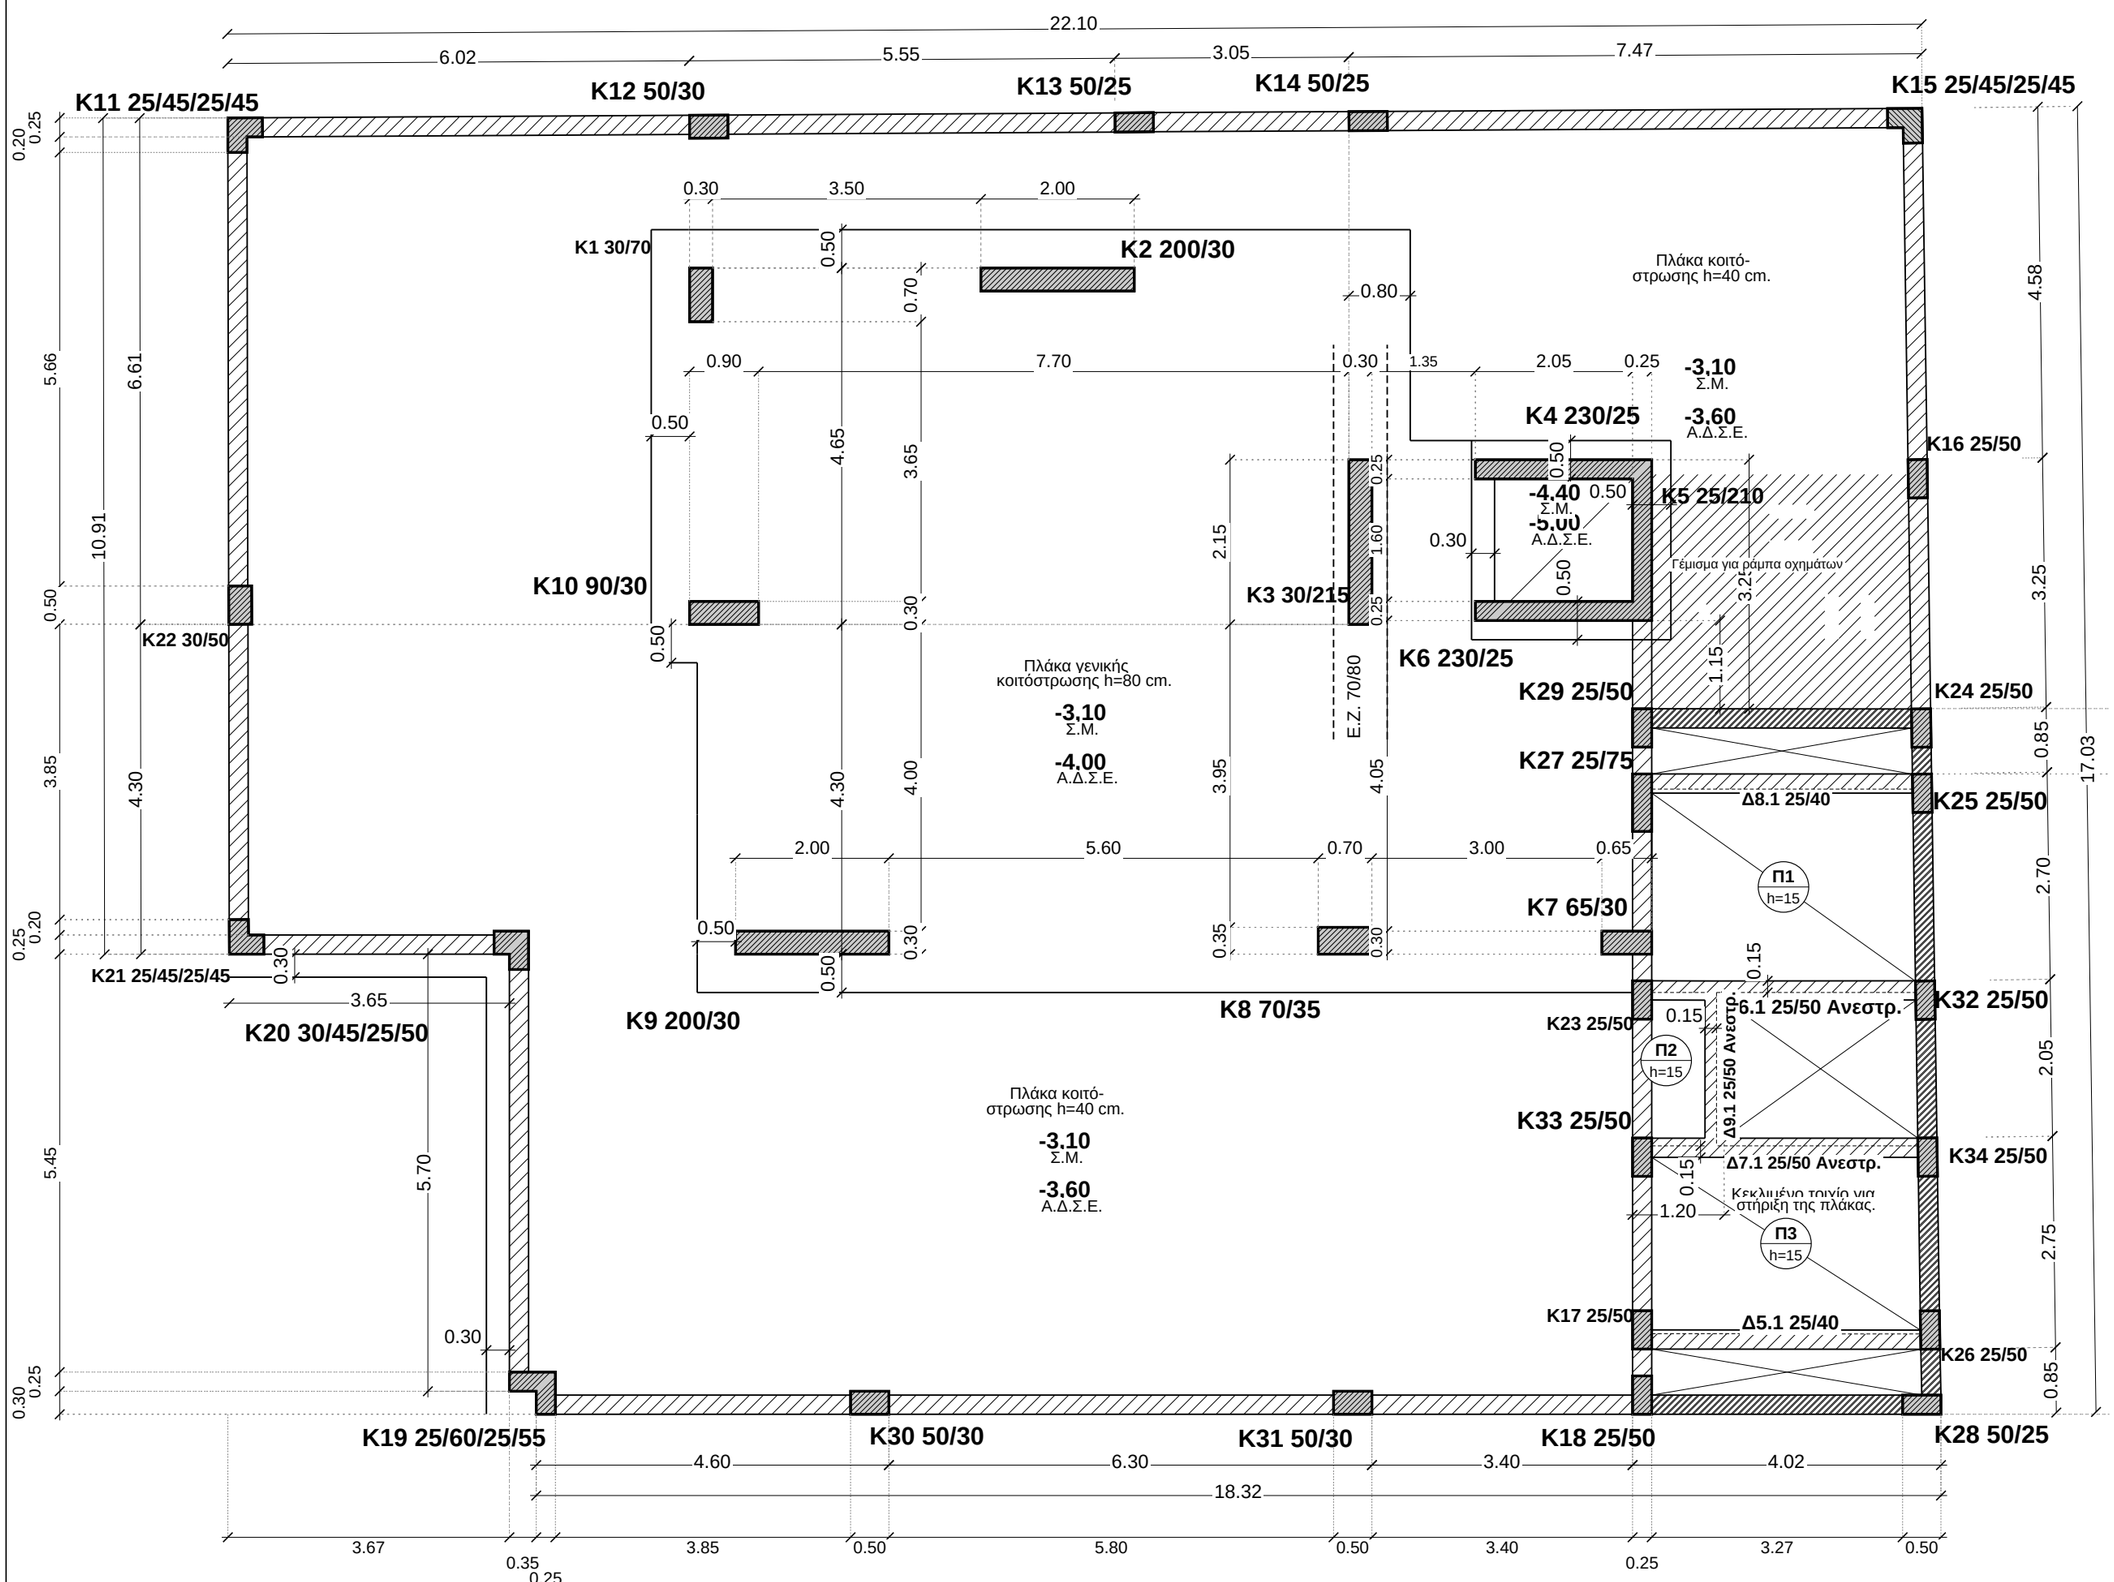


ΕΡΓΟ

ΚΩΝΣΤΑΝΤΙΝΟΥΠΟΛΕΩΣ 12 & ΑΓ. ΒΑΡΒΑΡΑΣ
ΑΡΓΥΡΟΥΠΟΛΗ – ARKAD Ι.Κ.Ε.

ΣΧΕΔΙΟ ΕΡΓΟΤΑΞΙΟΥ – ΞΥΛΟΤΥΠΟΣ ΧΩΡΙΣ ΟΠΛΙΣΜΟΥΣ

ΞΥΛΟΤΥΠΟΣ ΘΕΜΕΛΙΩΣΗΣ

Σ1

ΣΤΑΘΜΗ ΑΝΩ ΠΛΑΚΑΣ (ΜΠΕΤΟ)

-4,00 / -3,60

ΚΛΙΜΑΚΑ

1:80 (Α3 – εκτύπωση 100 %)

0 1 2 3 4 m

ΥΠΟΜΝΗΜΑ

K1 30/70	υποστύλωμα / τοιχείο – διατομή σε cm
Δ1.1 30/40	δοκός – πλάτος / ύψος σε cm
Π1 h=15	πλάκα – πάχος σε cm
Σ.Μ.	στάθμη μπετόν (m)
Α.Δ.Σ.Ε.	ανώτατη δυνατή στάθμη εκσκαφής (m)
- - -	κρυφή ακμή / στοιχείο από κάτω

Διαστάσεις σε m.
Οι αλυσίδες παρειών υποστυλωμάτων (εξωτερική σειρά κάθε πλευράς και οι εσωτερικές, γωνία με γωνία) μετρήθηκαν από τη γεωμετρία του σχεδίου· οι υπόλοιπες διαστάσεις είναι του μελετητή.

ΣΗΜΕΙΩΣΕΙΣ

Η θεμελίωση του υποσταθμού (-6,69) στο φύλλο Σ1α.

Βόρεια και ανατολική πλευρά λοξές (όριο οικοπέδου): ισχύουν οι διαστάσεις του μελετητή κατά μήκος τους.

ΒΑΣΗ

Σ1_ΕΦ.pdf – ξυλότυπος θεμελίωσης, Γ. Κόγιας (Drive 19/10/2026).
Οι οπλισμοί ΜΟΝΟ από το σχέδιο του μελετητή.

Έκδοση R00 – 10/11/2026