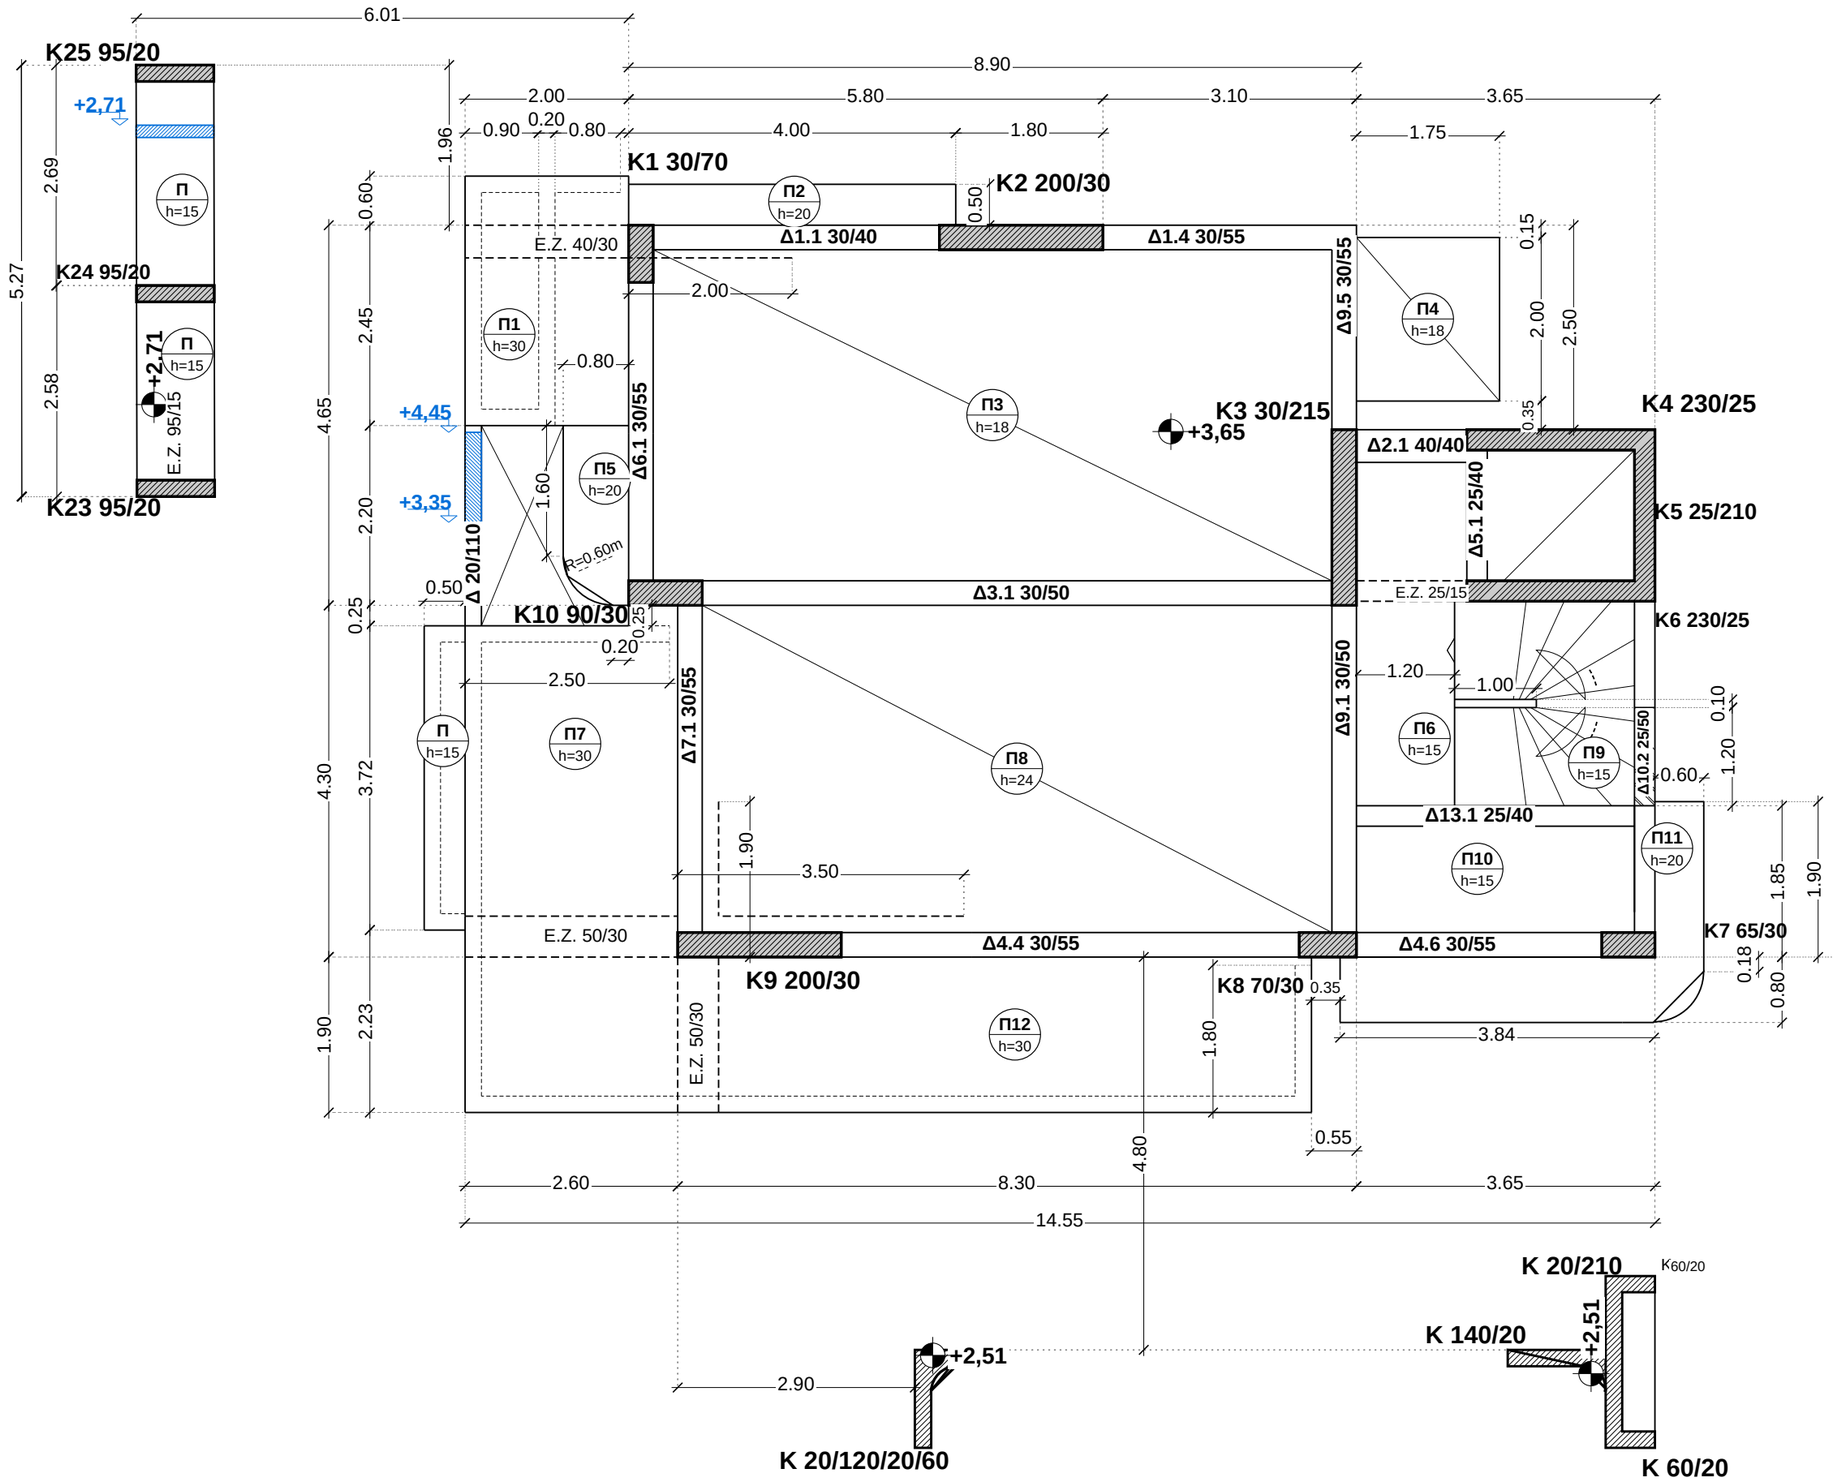


ΕΡΓΟ

ΚΩΝΣΤΑΝΤΙΝΟΥΠΟΛΕΩΣ 12 & ΑΓ. ΒΑΡΒΑΡΑΣ ΑΡΓΥΡΟΥΠΟΛΗ – ARKAD Ι.Κ.Ε.

ΣΧΕΔΙΟ ΕΡΓΟΤΑΞΙΟΥ – ΞΥΛΟΤΥΠΟΣ ΧΩΡΙΣ ΟΠΛΙΣΜΟΥΣ

ΟΡΟΦΗ ΙΣΟΓΕΙΟΥ – ΓΕΝΙΚΗ ΔΙΑΤΑΞΗ ΜΕ ΤΑ ΦΥΤΕΥΤΑ

Σ3α

ΣΤΑΘΜΗ ΑΝΩ ΠΛΑΚΑΣ (ΜΠΕΤΟ)

+3,65

ΚΛΙΜΑΚΑ

1:75 (Α3 – εκτύπωση 100 %)

0 1 2 3 4 m

ΥΠΟΜΝΗΜΑ

K1 30/70	υποστύλωμα / τοιχείο – διατομή σε cm
Δ1.1 30/40	δοκός – πλάτος / ύψος σε cm (το ύψος ΜΑΖΙ με την πλάκα)
Π3 h=15	πλάκα – πάχος σε cm
E.Z.	ενισχυμένη ζώνη μέσα στο πάχος της πλάκας (χωρίς καλούπι δοκού)
+0,00	στάθμη άνω επιφάνειας σκυροδέματος (m)
μπλε	φυτευτά στοιχεία και οι στάθμες τους
- - -	κρυφή ακμή / στοιχείο από κάτω

Διαστάσεις σε m.

ΣΗΜΕΙΩΣΕΙΣ

Γενική κάτοψη με τα φυτευτά στοιχεία στη θέση τους: Κ23–Κ25 (δυτικά) και τοιχεία εισόδου (νότια). Η κάτοψη σε μεγαλύτερη κλίμακα στο φύλλο Σ3.

ΒΑΣΗ

Σ3_ΕΦ.pdf – ξυλότυπος οροφής ισογείου, Γ. Κόγιας (Drive 19/10/2026).
Οι οπλισμοί ΜΟΝΟ από το σχέδιο του μελετητή.

Έκδοση R00 – 10/11/2026