
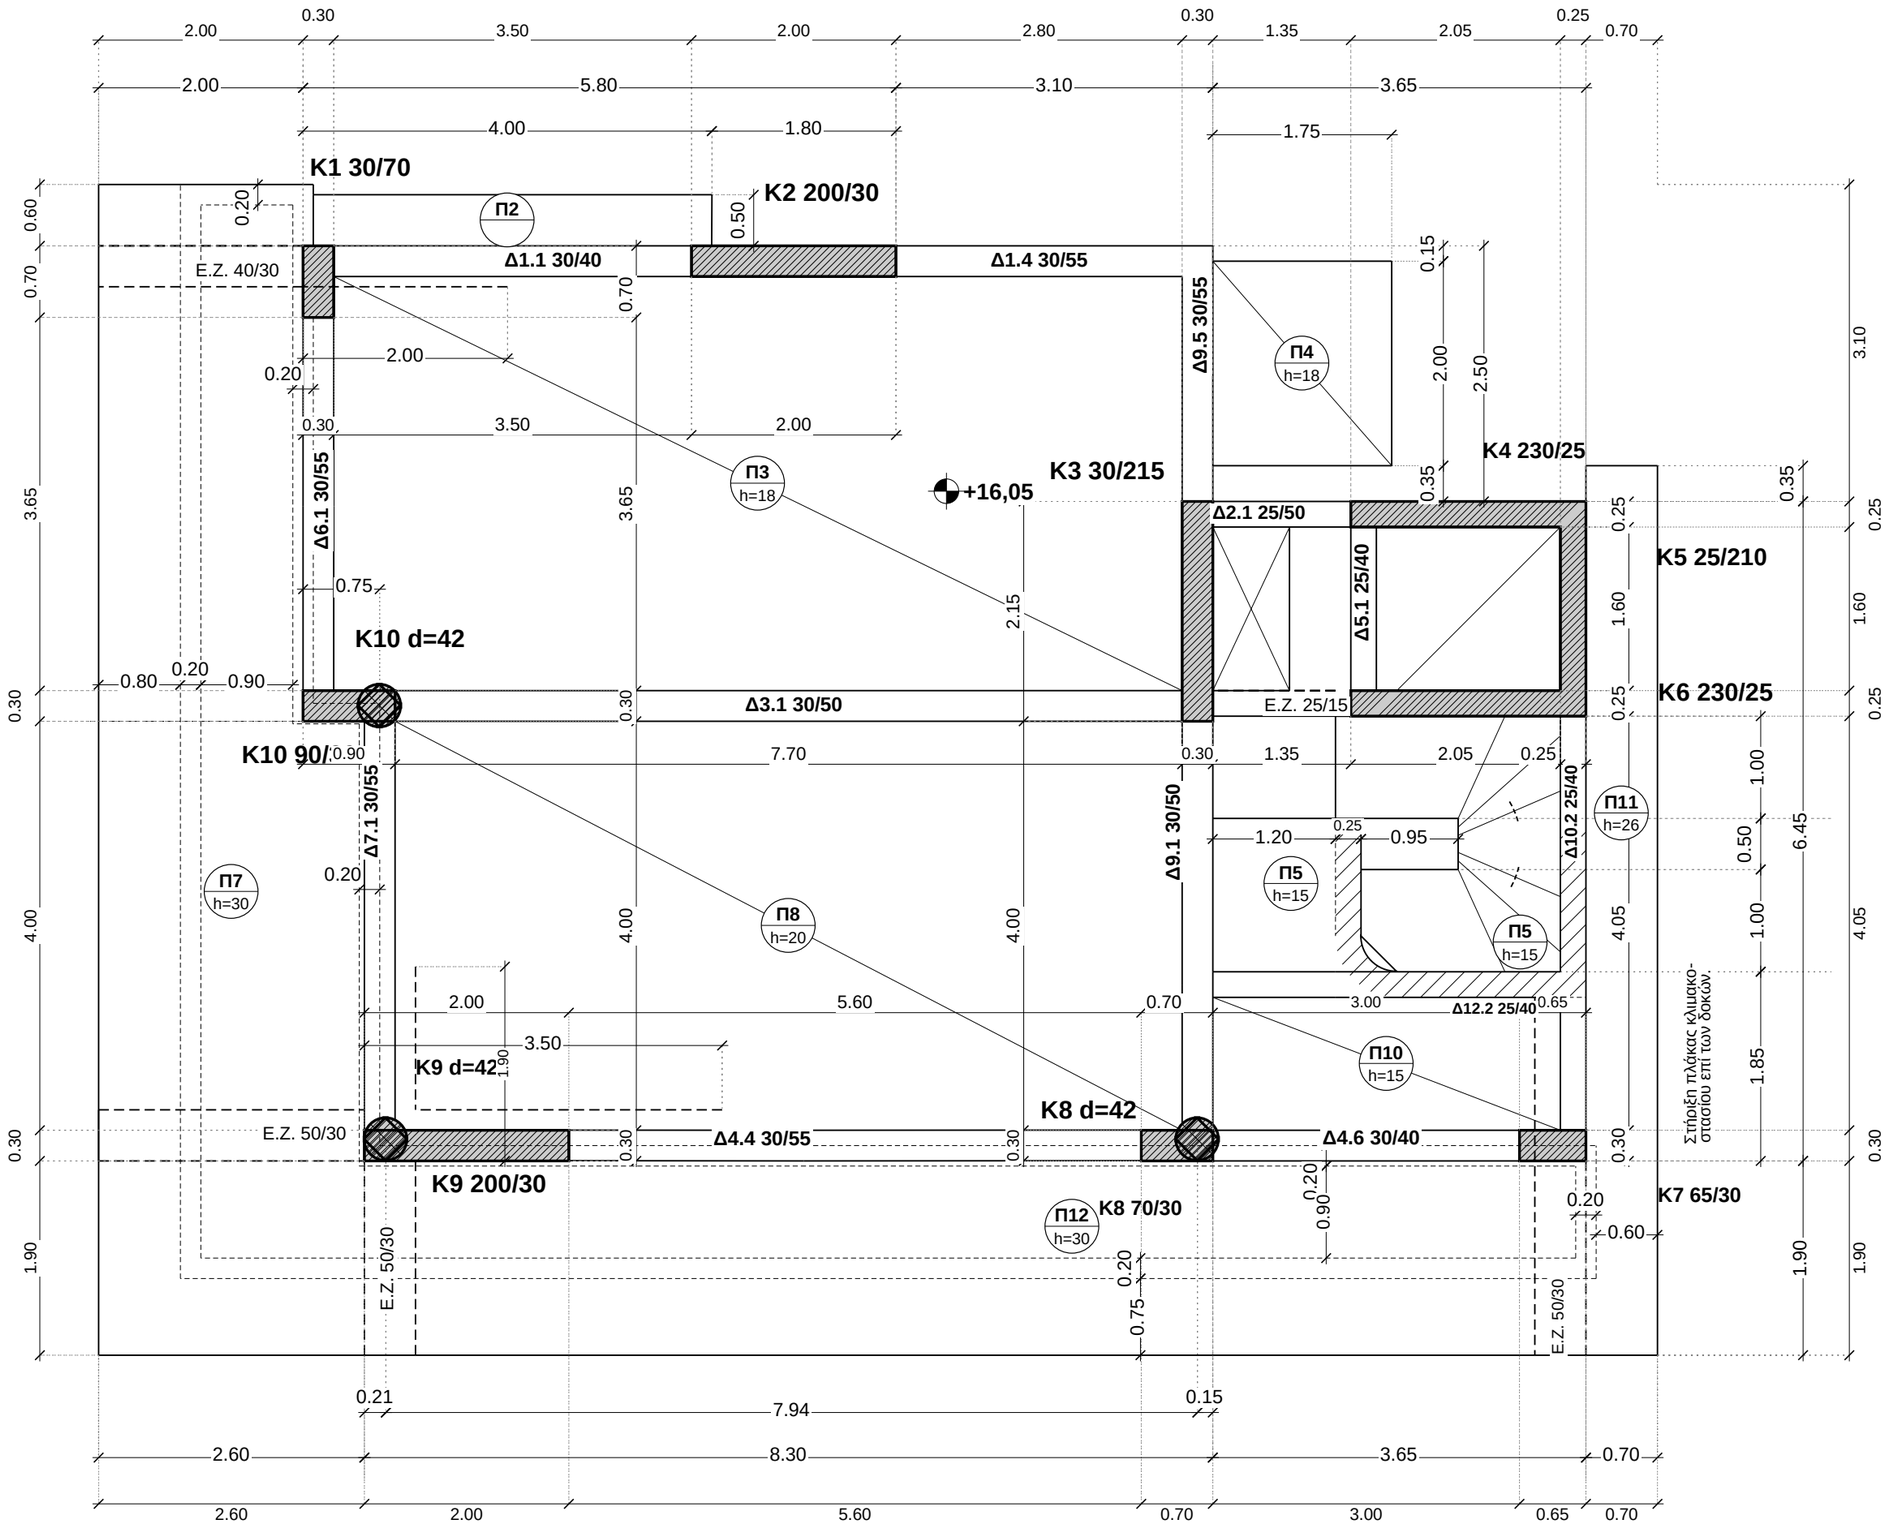


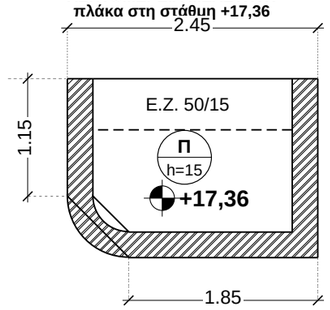

ΕΡΓΟ

ΚΩΝΣΤΑΝΤΙΝΟΥΠΟΛΕΩΣ 12 & ΑΓ. ΒΑΡΒΑΡΑΣ ΑΡΓΥΡΟΥΠΟΛΗ – ARKAD I.K.E.

ΣΧΕΔΙΟ ΕΡΓΟΤΑΞΙΟΥ – ΞΥΛΟΤΥΠΟΣ ΧΩΡΙΣ ΟΠΛΙΣΜΟΥΣ

ΞΥΛΟΤΥΠΟΣ ΟΡΟΦΗΣ Δ΄ ΟΡΟΦΟΥ

Σ7

ΣΤΑΘΜΗ ΑΝΩ ΠΛΑΚΑΣ (ΜΠΕΤΟ)

+16,05

ΚΛΙΜΑΚΑ

1:60 (Α3 – εκτύπωση 100 %)

0 1 2 3 m

ΥΠΟΜΝΗΜΑ

K1 30/70	υποστύλωμα / τοιχείο – διατομή σε cm
Δ1.1 30/40	δοκός – πλάτος / ύψος σε cm (το ύψος ΜΑΖΙ με την πλάκα)
Π3 h=15	πλάκα – πάχος σε cm
E.Z.	ενισχυμένη ζώνη μέσα στο πάχος της πλάκας (χωρίς καλούπι δοκού)
+0,00	στάθμη άνω επιφάνειας σκυροδέματος (m)
μπλε	φυτευτά στοιχεία και οι στάθμες τους
- - -	κρυφή ακμή / στοιχείο από κάτω

Διαστάσεις σε m.
Οι αλυσίδες παρειών υποστυλωμάτων (εξωτερική σειρά κάθε πλευράς και οι εσωτερικές, γωνία με γωνία) μετρήθηκαν από τη γεωμετρία του σχεδίου· οι υπόλοιπες διαστάσεις είναι του μελετητή.

ΥΨΟΜΕΤΡΑ – ΠΑΤΟΙ ΚΑΛΟΥΠΙΩΝ

στοιχείο	πάτος	ύψος*
Πλάκα h=15	**+15,90**	**2,95**
Πλάκα h=18	**+15,87**	**2,92**
Πλάκα h=20	**+15,85**	**2,90**
Πλάκα h=26	**+15,79**	**2,84**
Πλάκα h=30	**+15,75**	**2,80**
Δοκός ύψους 40	**+15,65**	**2,70**
Δοκός ύψους 50	**+15,55**	**2,60**
Δοκός ύψους 55	**+15,50**	**2,55**

Πάτος = στάθμη άνω πλάκας +16,05 μείον το ύψος (υπολογισμένο). * Ύψος πάτου από την πλάκα του κάτω ορόφου (+12,95). Δεν ισχύει για ανεστραμμένες δοκούς και για τα φυτευτά (μπλε στάθμες).

ΣΗΜΕΙΩΣΕΙΣ

Στις Ε.Ζ. των προβόλων: η υποδοχή για το σιφώνι και η υδρορροή να προβλεφθούν ΠΡΙΝ τη σκυροδέτηση, για να μην κόψει ο υδραυλικός τον οπλισμό της Ε.Ζ. (σημείωση μελετητή).

ΒΑΣΗ

Σ7_ΕΦ.pdf – ξυλότυπος οροφής Δ΄ ορόφου, Γ. Κόγιας (Drive 19/10/2026).
Οι οπλισμοί ΜΟΝΟ από το σχέδιο του μελετητή.

Έκδοση R00 – 10/11/2026