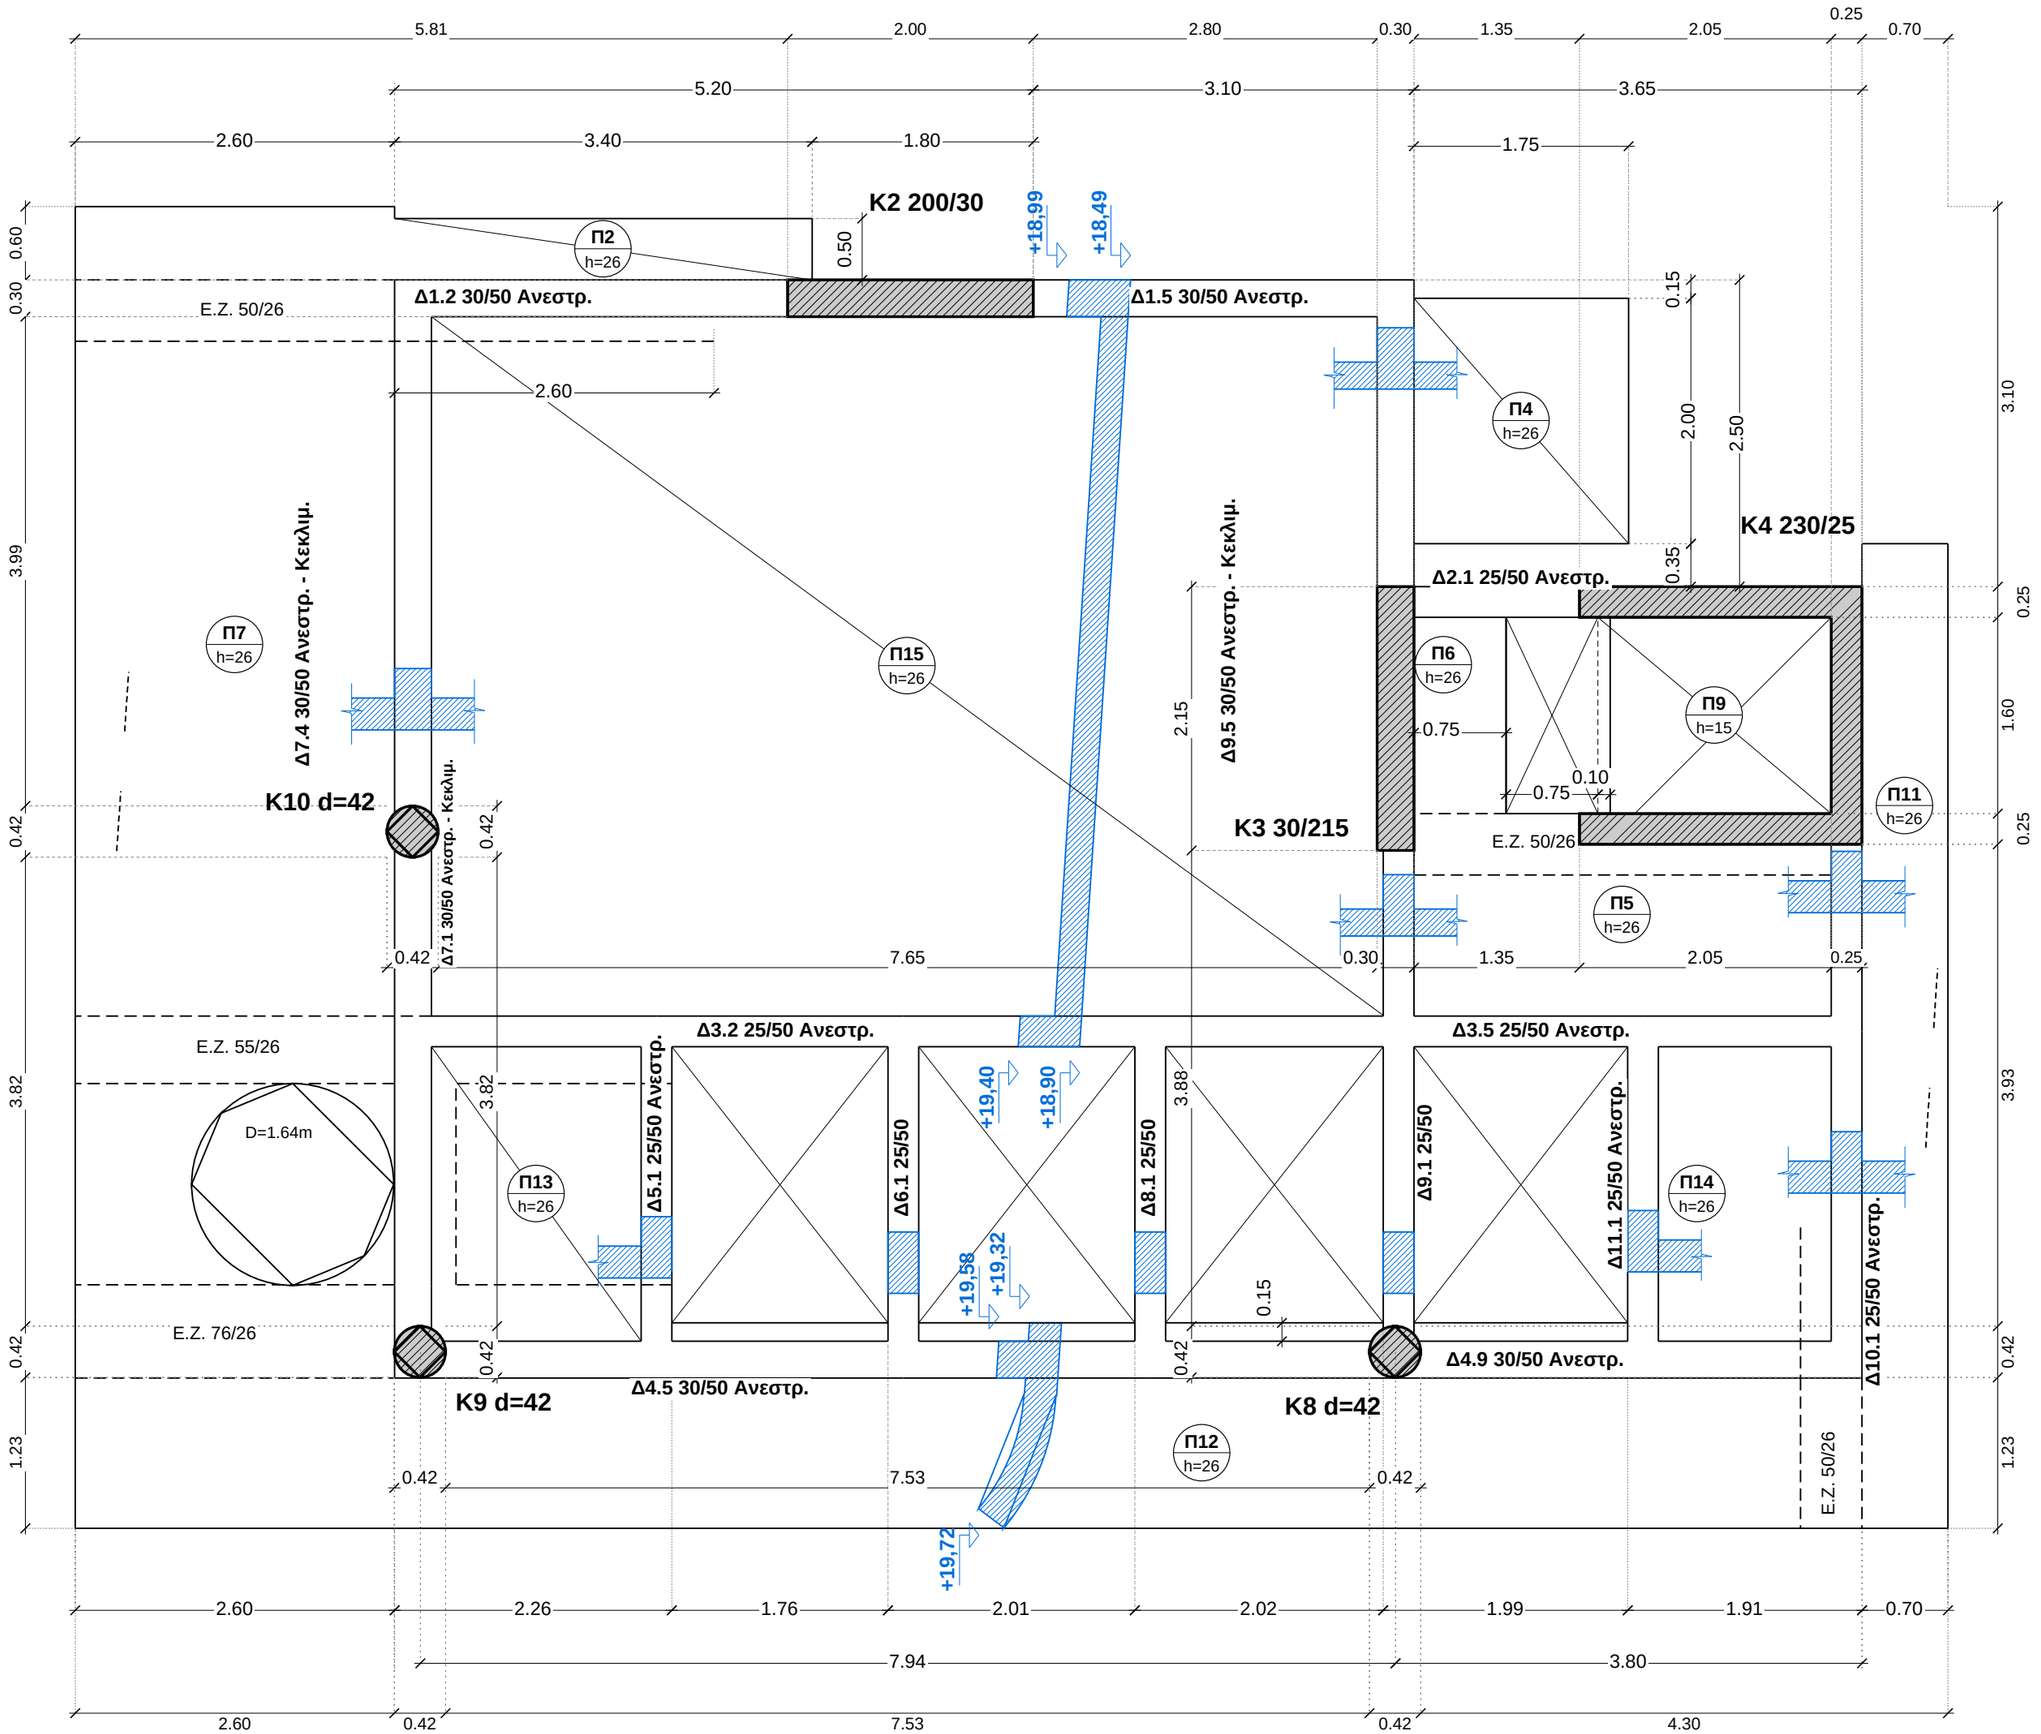


ΕΡΓΟ

ΚΩΝΣΤΑΝΤΙΝΟΥΠΟΛΕΩΣ 12 & ΑΓ. ΒΑΡΒΑΡΑΣ ΑΡΓΥΡΟΥΠΟΛΗ – ARKAD Ι.Κ.Ε.

ΣΧΕΔΙΟ ΕΡΓΟΤΑΞΙΟΥ – ΞΥΛΟΤΥΠΟΣ ΧΩΡΙΣ ΟΠΛΙΣΜΟΥΣ

ΞΥΛΟΤΥΠΟΣ ΣΟΦΙΤΑΣ (ΣΤΕΓΗ) Σ8

ΣΤΑΘΜΗ ΑΝΩ ΠΛΑΚΑΣ (ΜΠΕΤΟ)

+18,49 έως +19,72

ΚΛΙΜΑΚΑ

1:50 (Α3 – εκτύπωση 100 %)

0 1 2 m

ΥΠΟΜΝΗΜΑ

K1 30/70	υποστύλωμα / τοιχείο – διατομή σε cm
Δ1.1 30/40	δοκός – πλάτος / ύψος σε cm (το ύψος ΜΑΖΙ με την πλάκα)
Π3 h=15	πλάκα – πάχος σε cm
Ε.Ζ.	ενισχυμένη ζώνη μέσα στο πάχος της πλάκας (χωρίς καλούπι δοκού)
+0,00	στάθμη άνω επιφάνειας σκυροδέματος (m)
μπλε	φυτευτά στοιχεία και οι στάθμες τους
- - -	κρυφή ακμή / στοιχείο από κάτω

Διαστάσεις σε m.
Οι αλυσίδες παρειών υποστυλωμάτων (εξωτερική σειρά κάθε πλευράς και οι εσωτερικές, γωνία με γωνία) μετρήθηκαν από τη γεωμετρία του σχεδίου· οι υπόλοιπες διαστάσεις είναι του μελετητή.

ΣΗΜΕΙΩΣΕΙΣ

Στις Ε.Ζ. των προβόλων: η υποδοχή για το σιφώνι και η υδρορροή να προβλεφθούν ΠΡΙΝ τη σκυροδέτηση, για να μην κόψει ο υδραυλικός τον οπλισμό της Ε.Ζ. (σημείωση μελετητή).

Στέγη κεκλιμένη: οι στάθμες (μπλε) στις λωρίδες-τομές της κάτοψης. «Ανεστρ.» = ανεστραμμένη δοκός (πάνω από την πλάκα).

ΒΑΣΗ

Σ8.pdf – ξυλότυπος σοφίτας, Γ. Κόγιας (οριστική μελέτη 02/2026, Drive 06/11/2026).
Οι οπλισμοί ΜΟΝΟ από το σχέδιο του μελετητή.

Έκδοση R00 – 10/11/2026